


PART PLAN OF STAIRCASE - 2 (1) A-12-002

(BASEMENT FLOOR LEVEL)


BASEMENT TO GROUND FLOOR
FLOOR HEIGHT -3700
TREAD - 280mm
RISER - 170.00 mm
STAIR WIDTH - 1200mm
NO OF STEP -22 NOS

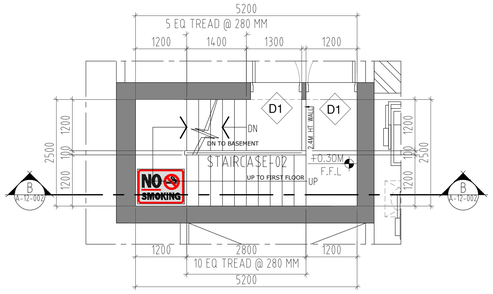

PART PLAN OF STAIRCASE - 2 (2) A-12-002

(GROUND FLOOR LEVEL)


GROUND TO 1ST FLOOR
FLOOR HEIGHT -5150
TREAD - 280mm
RISER - 155.00 mm
STAIR WIDTH - 1200mm
NO OF STEP -33 NOS

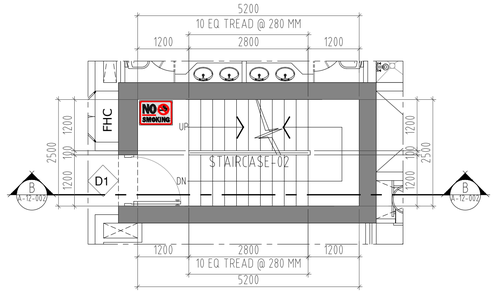

PART PLAN OF STAIRCASE - 2 (3) A-12-002

(1st FLOOR LEVEL)


1ST FLOOR TO 2ND FLOOR
FLOOR HEIGHT -3700
TREAD - 280mm
RISER - 170.00 mm
STAIR WIDTH - 1200mm
NO OF STEP -22 NOS

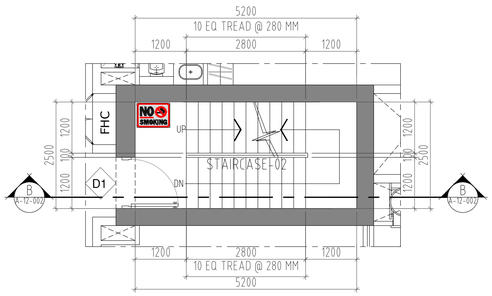

PART PLAN OF STAIRCASE - 2 (4) A-12-002

(2nd-5th FLOOR LEVEL)


2ND FLOOR TO 5TH FLOOR
FLOOR HEIGHT -3700
TREAD - 280mm
RISER - 170.00 mm
STAIR WIDTH - 1200mm
NO OF STEP -22 NOS

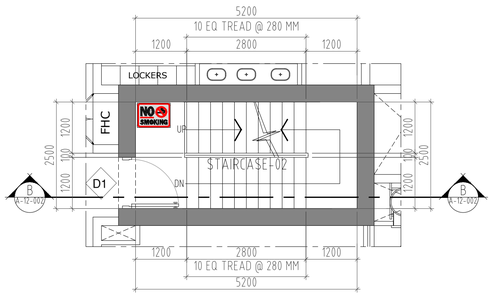

PART PLAN OF STAIRCASE - 2 (5) A-12-002

(LOWER ROOF LEVEL)


5TH FLOOR TO LOWER ROOF
FLOOR HEIGHT -3700
TREAD - 280mm
RISER - 170.00 mm
STAIR WIDTH - 1200mm
NO OF STEP -22 NOS

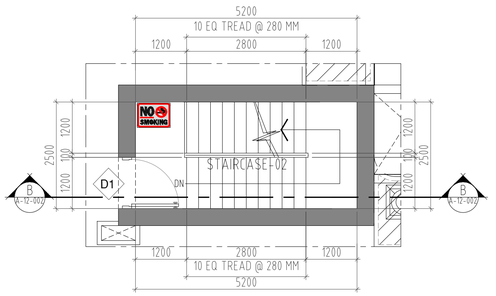

PART PLAN OF STAIRCASE - 2 (6) A-12-002


(UPPER ROOF LEVEL)

UPPER ROOF TO LOWER ROOF
FLOOR HEIGHT -3700
TREAD - 280mm
RISER - 170.00 mm
STAIR WIDTH - 1200mm
NO OF STEP -22 NOS

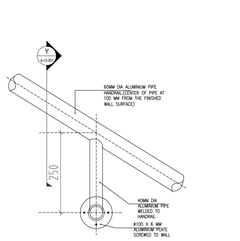


DETAIL -X (7) A-12-002

SCALE-1:50

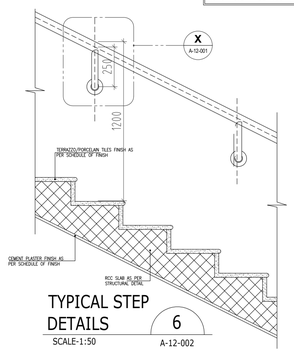


TYPICAL STEP DETAILS (6) A-12-002

SCALE-1:50

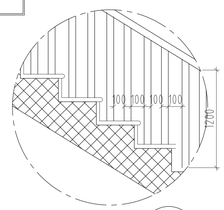


RAILING DETAILS (8) A-12-002

SCALE-1:50

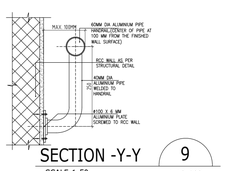

SECTION -Y-Y (9) A-12-002

SCALE-1:50

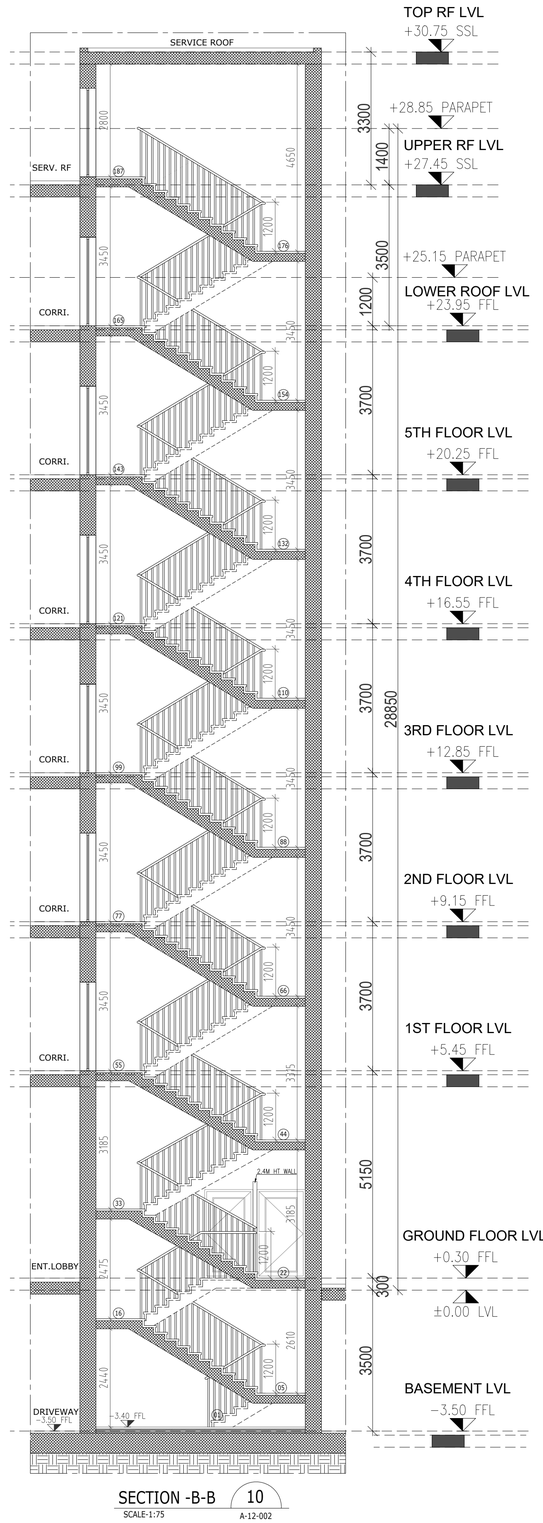

SECTION -B-B (10) A-12-002

SCALE-1:75

NOTES:

1. THIS DRAWING MAY NOT BE REPRODUCED BY ANY MEANS WITHOUT PRIOR APPROVAL FROM EMSQUARE
2. DRAWINGS ARE NOT TO BE SCALED, STATED DIMENSIONS ONLY ARE TO BE TAKEN.
3. ANY INCONSISTENCY OR DISCRIPANCY IS TO BE BROUGHT TO THE ATTENTION OF & RESOLVED BY THE ARCHITECT/ENGINEER BEFORE THE WORK IS PUT IN HAND.

DATE	DESCRIPTION	BY

CONSULTANT :

EMSQUARE
ENGINEERING CONSULTANTS
ARCHITECTS-CIVIL ENGINEERS-INTERIORS
P.O. Box 181903, Tel: +971 4 2729009, Fax: +971 4 2729334
Email: emsquare@emirates.net.ae

OWNER :

G F S REAL ESTATE L.L.C

JOB TITLE :

PROPOSED RESIDENTIAL BUILDING (B+G+5+ROOF)

PLOT NO. / PARCEL ID	BLOCK / COMMUNITY
5310319	SAIH SHUAIB 2

DRAWING TITLE :

STAIRCASE DETAIL-2

ARCHITECT :	STRUCTURAL ENGR. :	DRAWN :
SMITHA		SHAFI
SCALE :	DATE :	CHECKED BY :
1:125	JUN-2025	BABU
JOB NO :	DRAWING NO. :	REVISION NO. :
—	A-12-002	..

: D:\ANJU PROJECTS 2023\PROJECTS\GFS\08. 5310319 - COVENTRY RESIDENCE 3 - G F S REAL ESTATE L.L.C\FINAL SUBMISSION\FINAL AUTHORITY SUB\ARCH\CAD\A-12-001 TO A-12-002 STAIRCASE DETAILS.dwg