

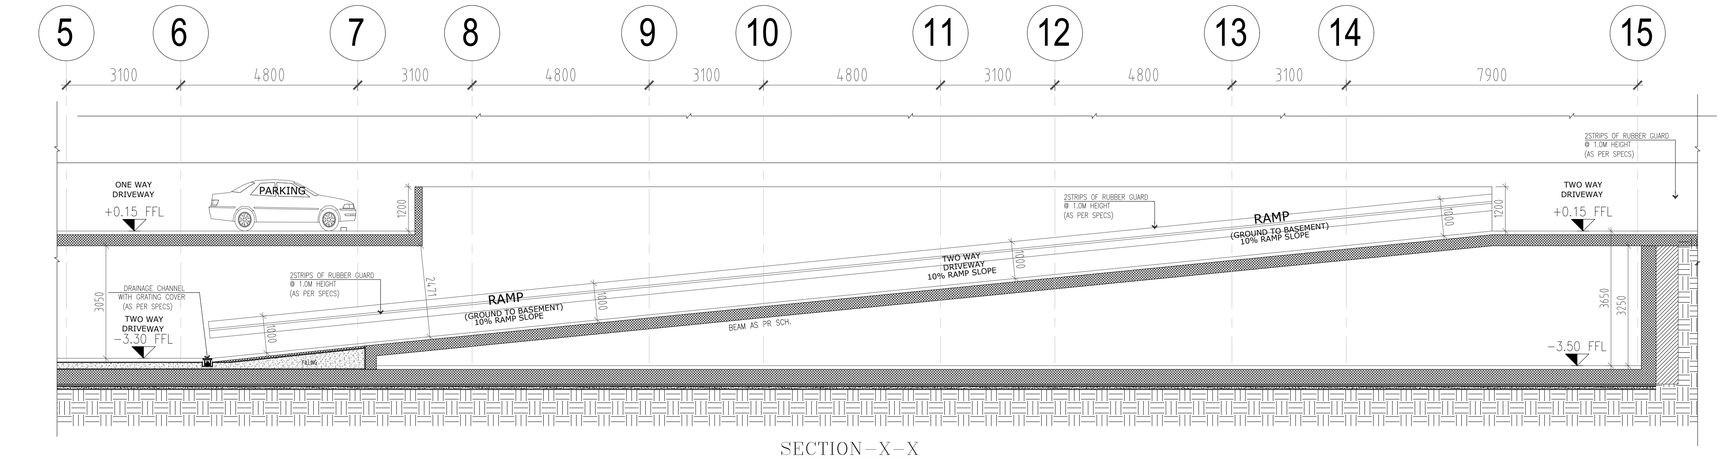



SECTION–X–X

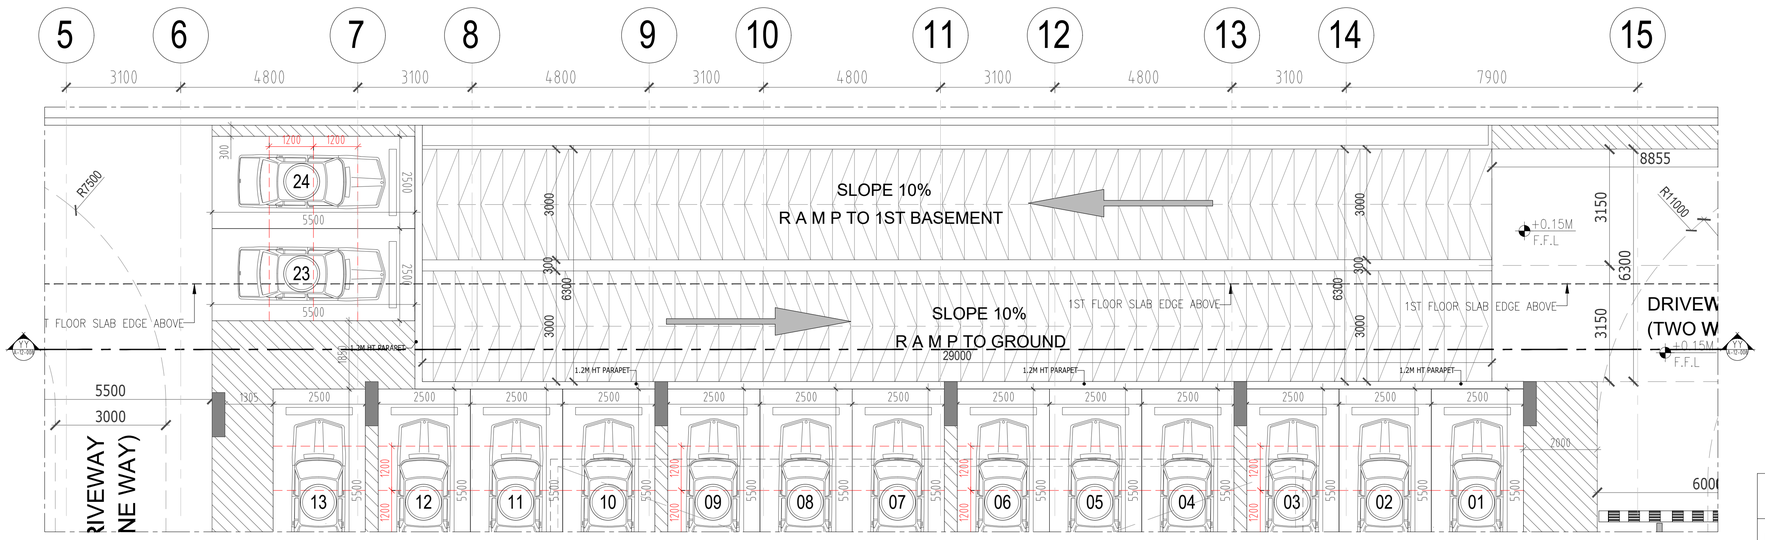


PART PLAN OF RAMP
(GROUND FLOOR LEVEL)

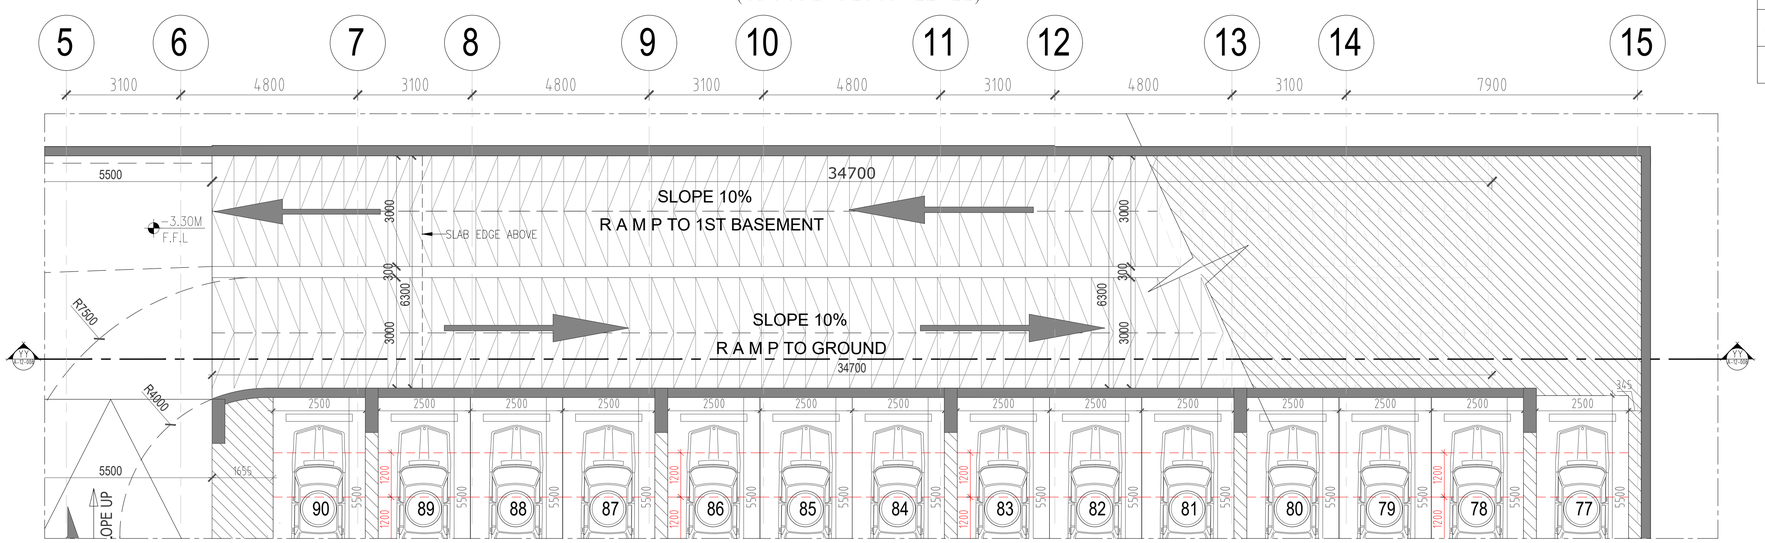


PART PLAN OF RAMP
(BASEMENT FLOOR LEVEL)

| RAMP DETAILS -( GROUND TO BASEMENT ) | |
|---|---|
| RAMP LENGTH - 34.70 M STRAIGHT | |
| RAMP SLOPE - 10% | |
| GROUND LEVEL - +0.15M FFL | =HEIGHT - 3.45M |
| BASEMENT LEVEL - =-3.30M SSL | |

NOTES:

1. THIS DRAWING MAY NOT BE REPRODUCED BY ANY MEANS WITHOUT PRIOR APPROVAL FROM EMSQUARE
2. DRAWINGS ARE NOT TO BE SCALED, STATED DIMENSIONS ONLY ARE TO BE TAKEN.
3. ANY INCONSISTENCY OR DISCRIPANCY IS TO BE BROUGHT TO THE ATTENTION OF & RESOLVED BY THE ARCHITECT/ENGINEER BEFORE THE WORK IS PUT IN HAND.

| DATE | DESCRIPTION | BY |
|---|---|---|
| | | |

CONSULTANT :

EMSQUARE
ENGINEERING CONSULTANTS
ARCHITECTS-CIVIL ENGINEERS-INTERIORS
P.O. Box 181903, Tel: +971 4 2729009, Fax: +971 4 2729334
Email: emsquare@emirates.net.ae

OWNER :

**G F S REAL ESTATE L.L.C**

JOB TITLE :

PROPOSED RESIDENTIAL BUILDING
(B+G+5+ROOF)

| PLOT NO. / PARCEL ID | BLOCK / COMMUNITY |
|---|---|
| 5310319 | SAIH SHUAIB 2 |

DRAWING TITLE :

RAMP DETAILS

| ARCHITECT : | STRUCTURAL ENGR. : | DRAWN : |
|---|---|---|
| SMITHA | | SHAFI |
| SCALE : | DATE : | CHECKED BY : |
| 1:125 | JUN-2025 | BABU |
| JOB NO : | DRAWING NO. : | REVISION NO. : |
| — | A-12-008 | .. |

: D:\ANJU PROJECTS 2023\PROJECTS\GFS\08. 5310319 - COVENTRY RESIDENCE 3 - G F S REAL ESTATE L.L.C\FINAL SUBMISSION\FINAL AUTHORITY SUB\ARCH\CAD\A-12-008 RAMP DETAILS.dwg