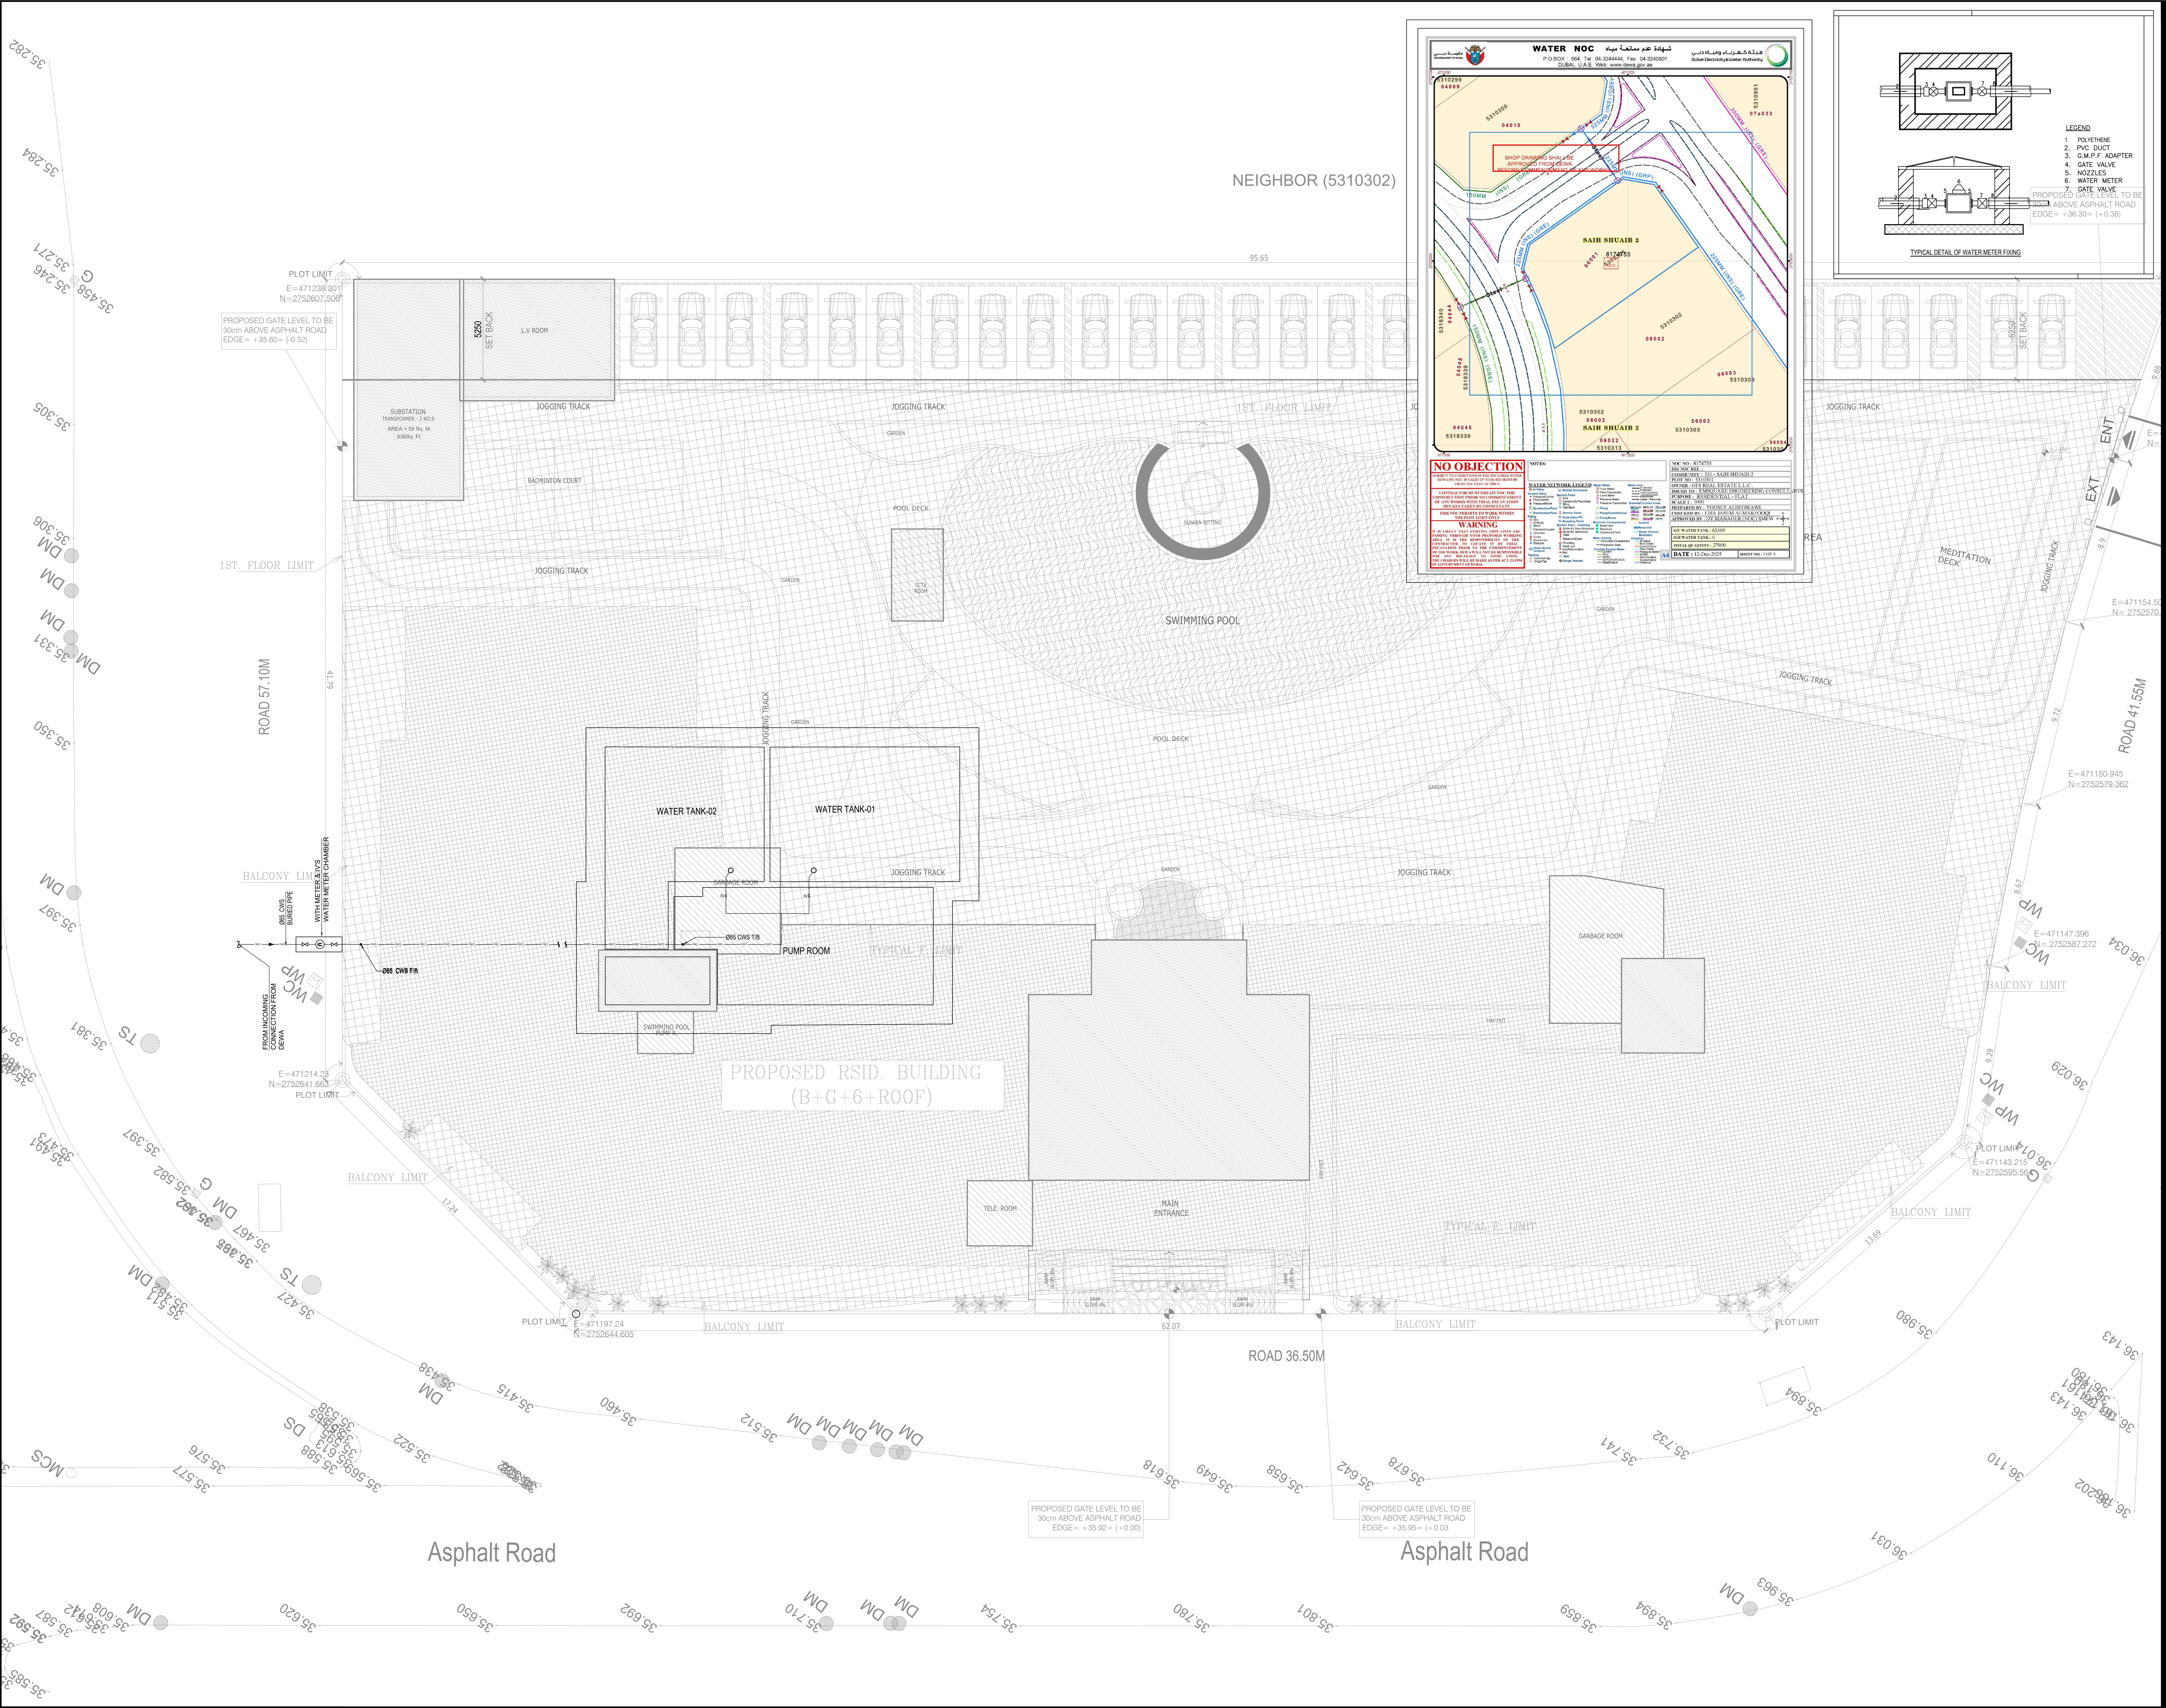

WATER NOC شهادة عدم ممانعة مياه

حكومة دبي
GOVERNMENT OF DUBAI

هيئة كهرباء ومياه دبي
Dubai Electricity & Water Authority

P.O.BOX : 564, Tel: 04-3244444, Fax: 04-3240801
DUBAI, U.A.E. Web: www.dewa.gov.ae

SHOP DRAWING SHALL BE APPROVED FROM DEWA BEFORE COMMENCEMENT OF ANY WORKS

NO OBJECTION

SUBJECT TO CONDITIONS IN THE ENCLOSED NOTES. DEWA (W) NOC IS VALID UP TO (6) SIX MONTHS FROM THE DATE OF ISSUE.

CONTRACTOR MUST OBTAIN NOC FOR CONSTRUCTION PRIOR TO COMMENCEMENT OF ANY WORKS WITH TRIAL EXCAVATION DETAILS TAKEN BY CONSULTANT.

THIS NOC PERMITS TO WORK WITHIN THE PLOT LIMIT ONLY

WARNING

IT IS LIKELY THAT EXISTING LDPE LINES ARE PASSING THROUGH YOUR PROPOSED WORKING AREA. IT IS THE RESPONSIBILITY OF THE CONTRACTOR TO LOCATE IT BY TRIAL EXCAVATION PRIOR TO THE COMMENCEMENT OF THE WORK. DEWA WILL NOT BE RESPONSIBLE FOR ANY BREAKAGE TO THESE LINES. THE CHARGES WILL BE MADE AS PER ACT (2)/1994 OF GOVERNMENT OF DUBAI.

NOTES:

WATER NETWORK LEGEND

NOC NO : 8174755
DM NOC REF. :
COMMUNITY : 531 - SAIH SHUAIB 2
PLOT NO : 5310301
OWNER : GFS REAL ESTATE L.L.C .
ISSUED TO : EMSQUARE ENGINEERING CONSULTANTS
PURPOSE : RESIDENTIAL - FLAT
SCALE 1 : 1000
PREPARED BY : YOUSUF.ALBEDWAWI
CHECKED BY : EISA JASEM ALMARZOOQI
APPROVED BY : DY.MANAGER (NOC) SMEW

G/U WATER TANK : 65369
O.H WATER TANK : 0
TOTAL QUANTITY : 27900

A4 DATE : 12-Dec-2025 SHEET NO : 1 OF 3

LEGEND

1. POLYETHENE
2. PVC DUCT
3. G.M.P.F ADAPTER
4. GATE VALVE
5. NOZZLES
6. WATER METER
7. GATE VALVE

TYPICAL DETAIL OF WATER METER FIXING

LEGEND

HWS	HOT WATER SUPPLY PIPE
BCWS	BOOSTED COLD WATER SUPPLY PIPE
GCWS	GRAVITY COLD WATER SUPPLY PIPE
TCWS	TRANSFER COLD WATER SUPPLY PIPE
NRV	NON RETURN VALVE
IV	ISOLATING VALVE
	WATER CLOSET
	BIB TAP
	HAND SPRAY
	HOT AND COLD WATER TAP POINT
	WATER HAMMER ARRESTOR
F/A	FROM ABOVE
F/B	FROM BELOW
T/A	TO ABOVE
T/B	TO BELOW
H/L	HIGH LEVEL

DATE	DESCRIPTION	BY

CONSULTANT :

EMSQUARE
ENGINEERING CONSULTANTS
ARCHITECTS-CIVIL ENGINEERS-INTERIORS
P.O. Box 181903, Tel: +971 4 2729009, Fax: +971 4 2729334
Email: emsquare@emirates.net.ae

OWNER :

G F S REAL ESTATE L.L.C

JOB TITLE :

PROPOSED RESIDENTIAL BUILDING
(B+G+6+ROOF)

PLOT NO. / PARCEL ID	BLOCK / COMMUNITY
5310301	SAIH SHUAIB 2

DRAWING TITLE :
SETTING OUT PLAN
WATER SUPPLY LAYOUT

ARCHITECT :	STRUCTURAL ENGR. :	DRAWN :
LAYLA	-	**SATHEESH**
SCALE :	DATE :	CHECKED BY :
1:150 @ A1	**AUGUST2025**	**YASEEN**
JOB NO :	DRAWING NO. :	REVISION NO. :
——	WS-00	--