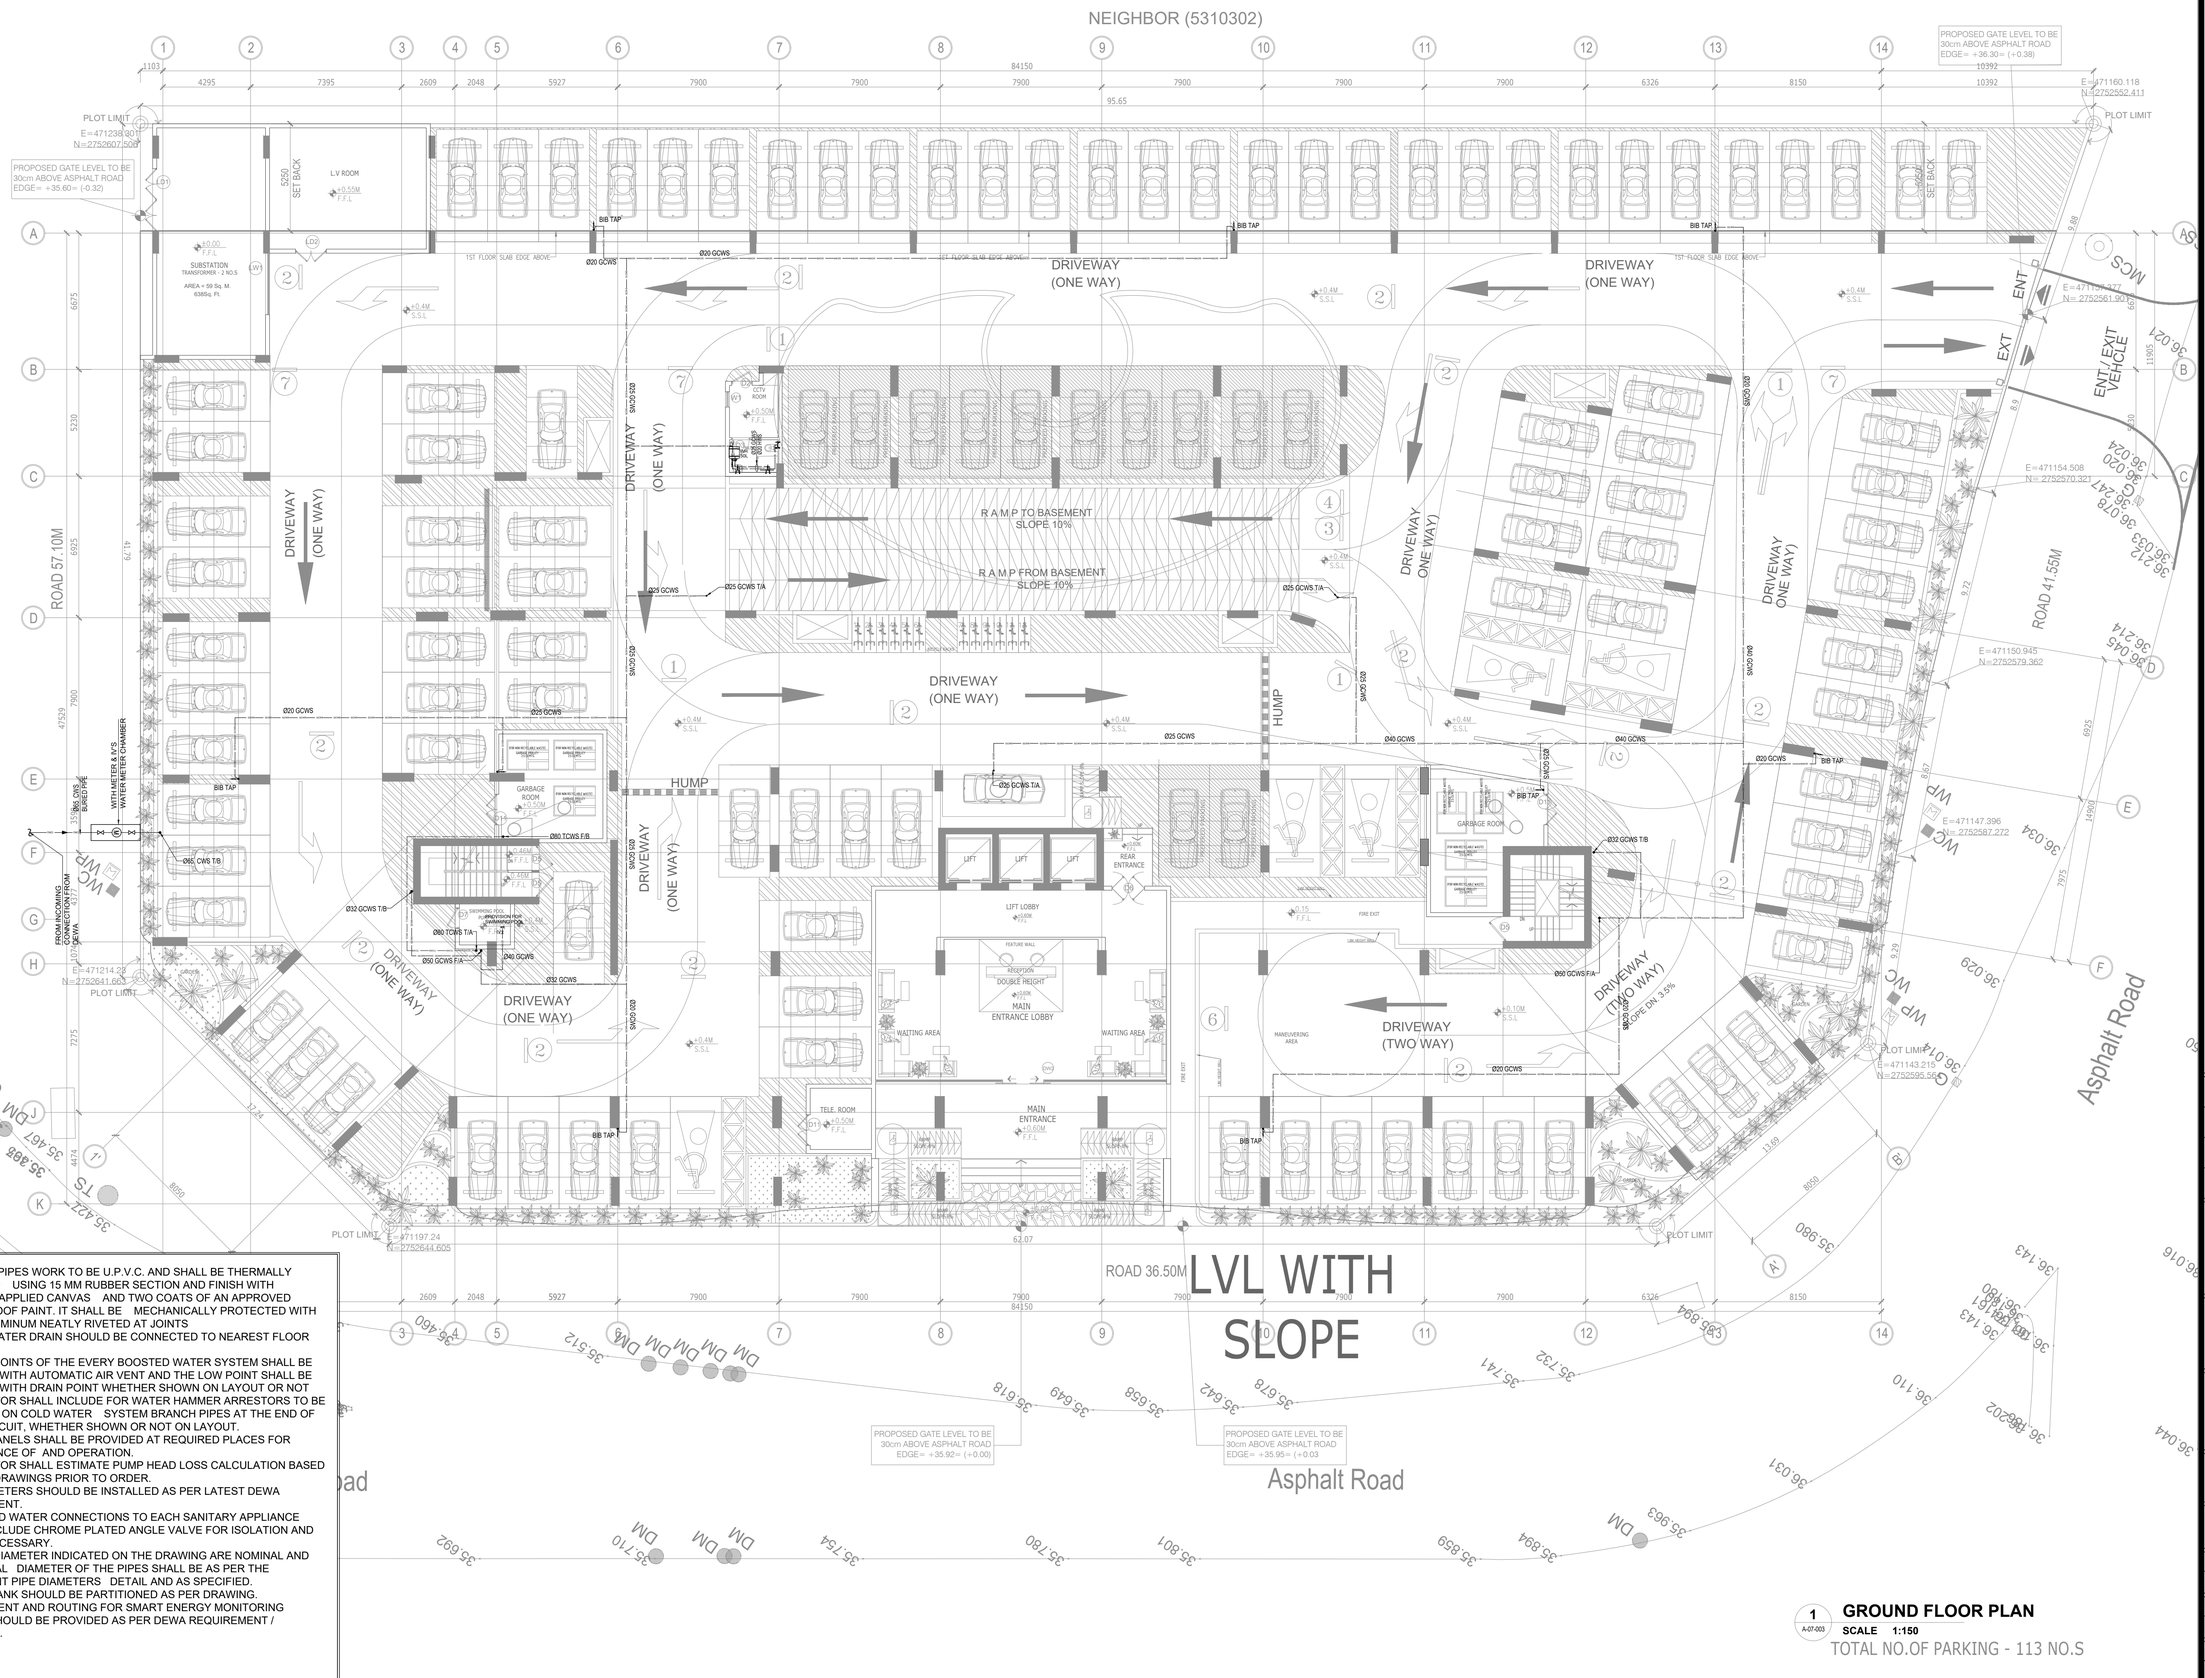


1. ALL ROOF PIPES WORK TO BE U.P.V.C. AND SHALL BE THERMALLY INSULATED USING 15 MM RUBBER SECTION AND FINISH WITH ADHESIVE APPLIED CANVAS AND TWO COATS OF AN APPROVED WATERPROOF PAINT. IT SHALL BE MECHANICALLY PROTECTED WITH SHEET ALUMINUM NEATLY RIVETED AT JOINTS
2. WATER HEATER DRAIN SHOULD BE CONNECTED TO NEAREST FLOOR DRAIN.
3. ALL HIGH POINTS OF THE EVERY BOOSTED WATER SYSTEM SHALL BE PROVIDED WITH AUTOMATIC AIR VENT AND THE LOW POINT SHALL BE PROVIDED WITH DRAIN POINT WHETHER SHOWN ON LAYOUT OR NOT
4. CONTRACTOR SHALL INCLUDE FOR WATER HAMMER ARRESTORS TO BE INSTALLED ON COLD WATER SYSTEM BRANCH PIPES AT THE END OF EVERY CIRCUIT, WHETHER SHOWN OR NOT ON LAYOUT.
5. ACCESS PANELS SHALL BE PROVIDED AT REQUIRED PLACES FOR MAINTENANCE OF AND OPERATION.
6. CONTRACTOR SHALL ESTIMATE PUMP HEAD LOSS CALCULATION BASED ON SHOP DRAWINGS PRIOR TO ORDER.
7. ALL SUB METERS SHOULD BE INSTALLED AS PER LATEST DEWA REQUIREMENT.
8. HOT & COLD WATER CONNECTIONS TO EACH SANITARY APPLIANCE SHALL INCLUDE CHROME PLATED ANGLE VALVE FOR ISOLATION AND WHERE NECESSARY.
9. THE PIPE DIAMETER INDICATED ON THE DRAWING ARE NOMINAL AND THE ACTUAL DIAMETER OF THE PIPES SHALL BE AS PER THE EQUIVALENT PIPE DIAMETERS DETAIL AND AS SPECIFIED.
10. ALL GRP TANK SHOULD BE PARTITIONED AS PER DRAWING.
11. CONTAINMENT AND ROUTING FOR SMART ENERGY MONITORING SYSTEM SHOULD BE PROVIDED AS PER DEWA REQUIREMENT / STANDARD.

1 / A-07-003 GROUND FLOOR PLAN
SCALE 1:150

LEGEND

HWS	HOT WATER SUPPLY PIPE
BCWS	BOOSTED COLD WATER SUPPLY PIPE
GCWS	GRAVITY COLD WATER SUPPLY PIPE
TCWS	TRANSFER COLD WATER SUPPLY PIPE
NRV	NON RETURN VALVE
IV	ISOLATING VALVE
	WATER CLOSET
	BIB TAP
	HAND SPRAY
	HOT AND COLD WATER TAP POINT
	WATER HAMMER ARRESTOR
F/A	FROM ABOVE
F/B	FROM BELOW
T/A	TO ABOVE
T/B	TO BELOW
H/L	HIGH LEVEL

DATE	DESCRIPTION	BY

CONSULTANT :

EMSQUARE
ENGINEERING CONSULTANTS
ARCHITECTS-CIVIL ENGINEERS-INTERIORS
P.O. Box 181903, Tel: +971 4 2729009, Fax: +971 4 2729304
Email: emsquare@emirates.net.ae

OWNER :

G F S REAL ESTATE L.L.C

JOB TITLE :

PROPOSED RESIDENTIAL BUILDING (B+G+6+ROOF)

PLOT NO. / PARCEL ID	BLOCK / COMMUNITY
5310301	SAIH SHUAIB 2

DRAWING TITLE :
GROUND FLOOR PLAN
WATER SUPPLY LAYOUT

ARCHITECT :	STRUCTURAL ENGR. :	DRAWN :
LAYLA	-	SATHEESH
SCALE :	DATE :	CHECKED BY :
1:150 @ A1	AUGUST2025	YASEEN
JOB NO :	DRAWING NO. :	REVISION NO. :
----	WS-03	--