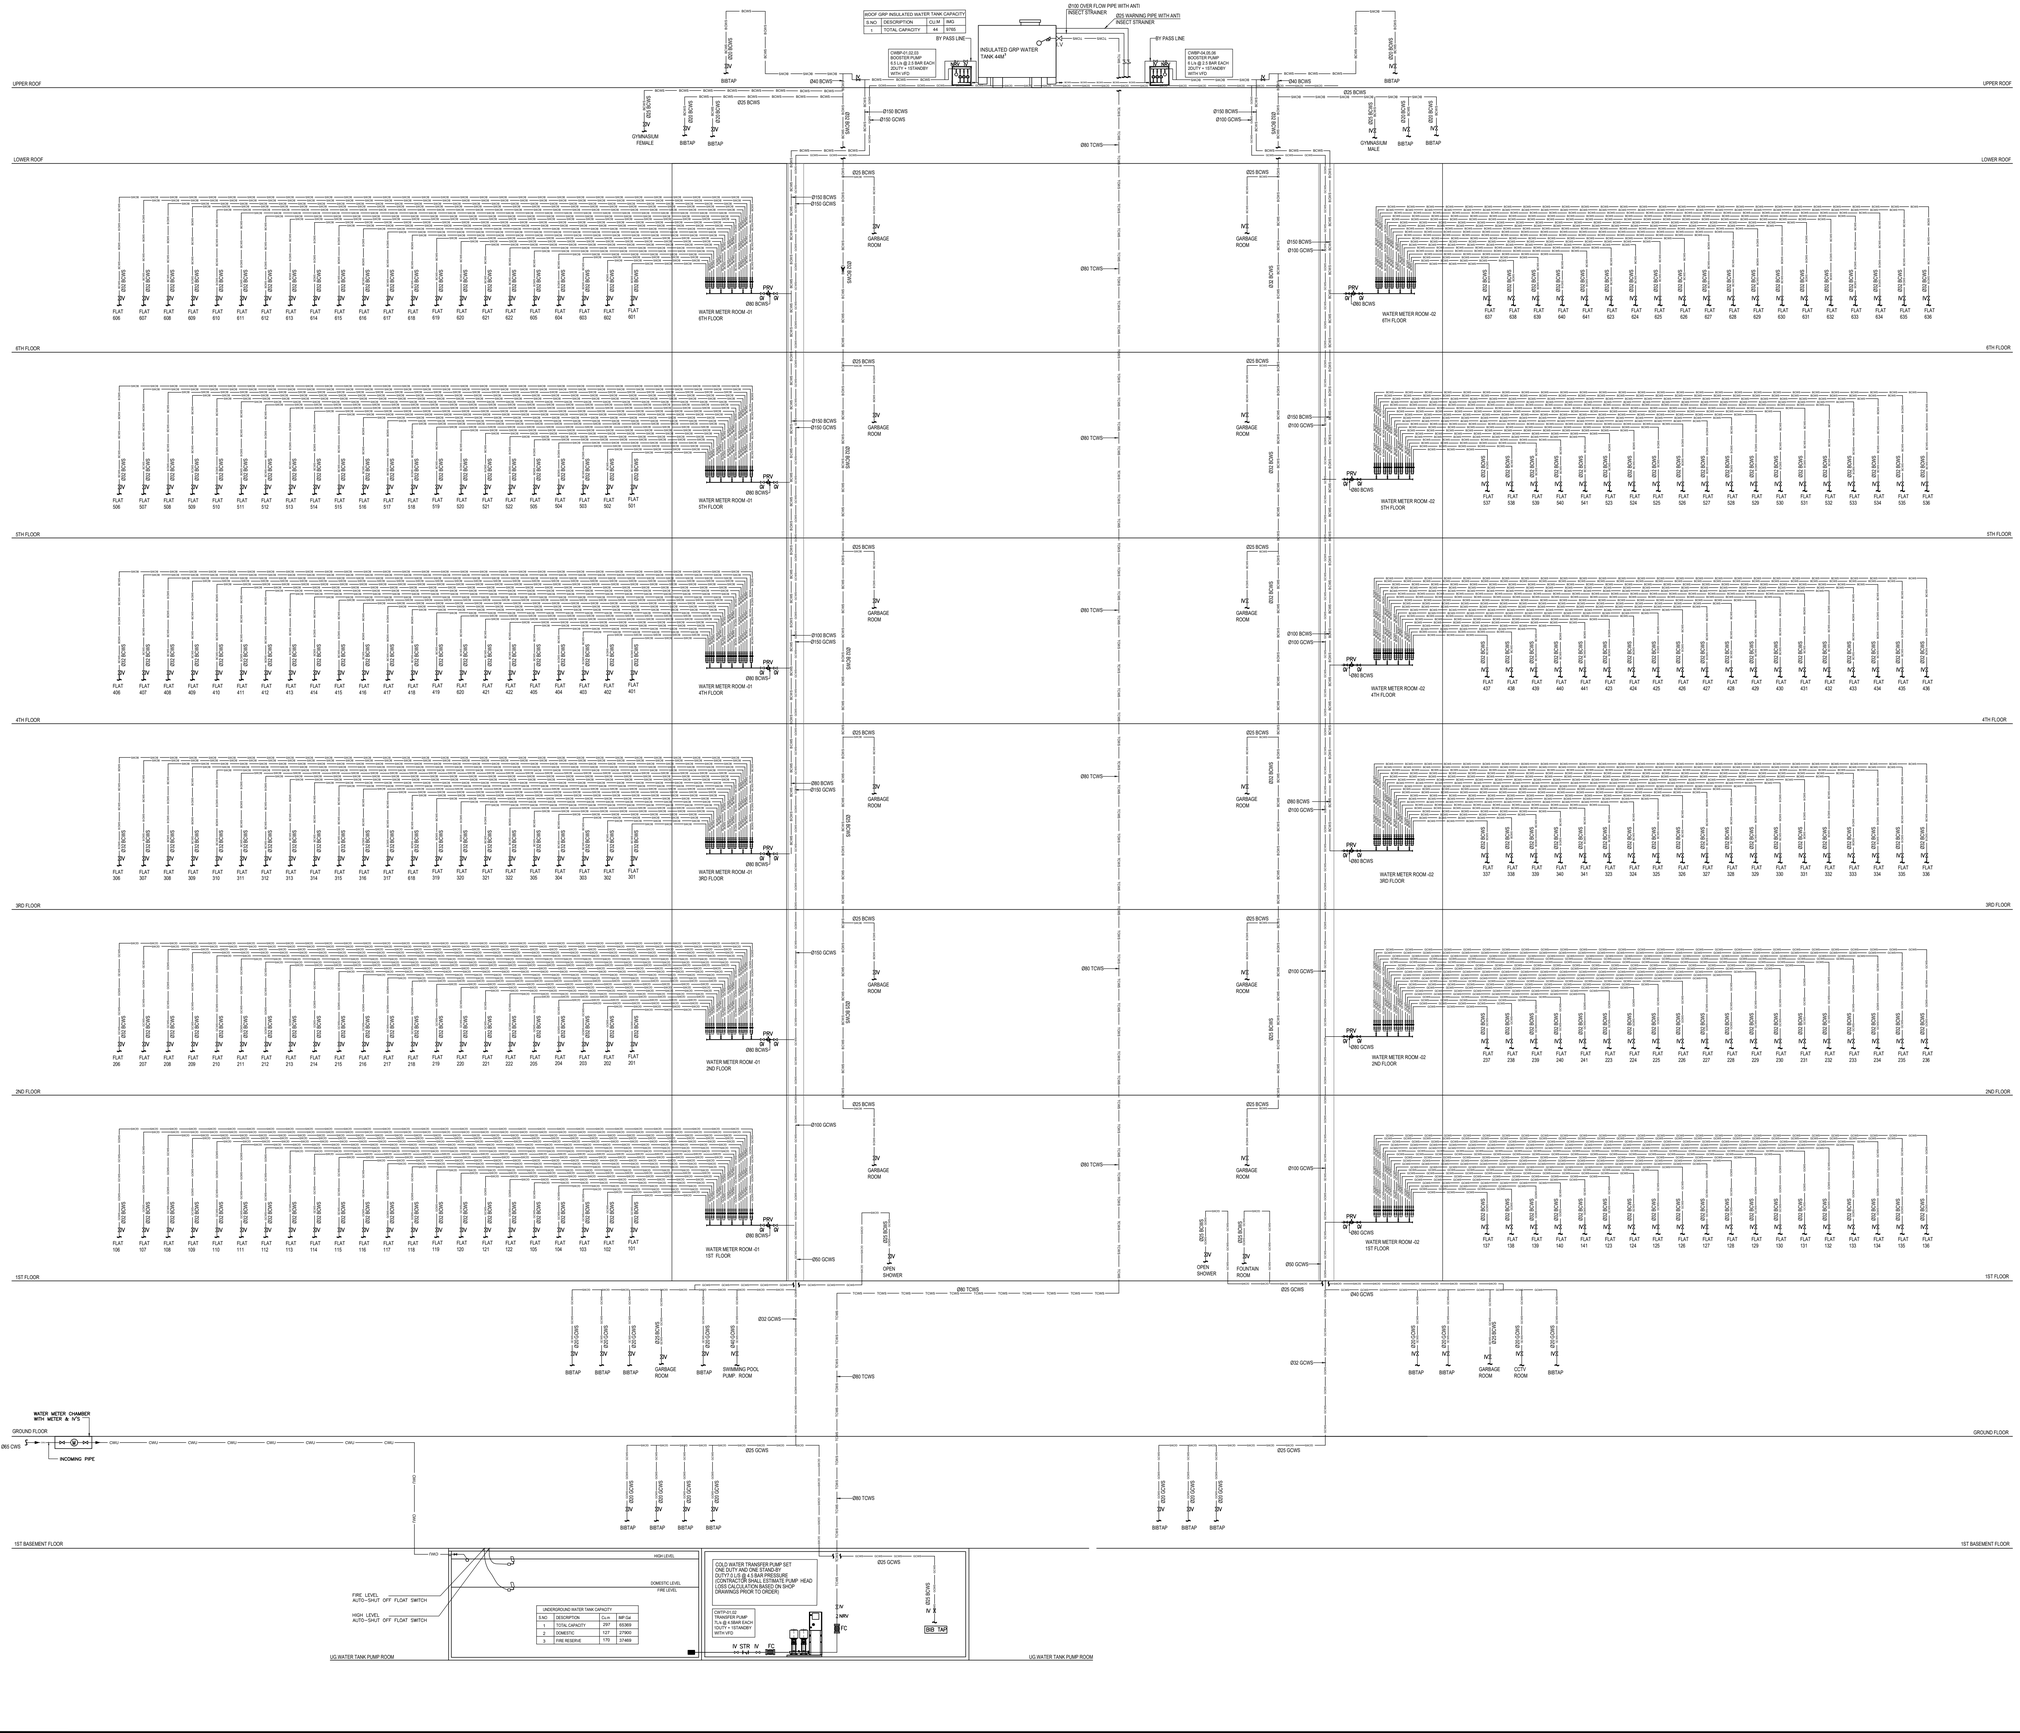


DATE	DESCRIPTION	BY

CONSULTANT :

EMSQUARE
ENGINEERING CONSULTANTS
ARCHITECTS-CIVIL ENGINEERS-INTERIORS
P.O. Box 181903, Tel: +971 4 2729009, Fax: +971 4 2729334
Email: emsquare@emirates.net.ae

OWNER :

G F S REAL ESTATE L.L.C

JOB TITLE :

PROPOSED RESIDENTIAL BUILDING (B+G+6+ROOF)

PLOT NO. / PARCEL ID	BLOCK / COMMUNITY
5310301	SAIH SHUAIB 2

DRAWING TITLE :

SCHEMATIC DIAGRAM WATER SUPPLY LAYOUT

ARCHITECT :	STRUCTURAL ENGR. :	DRAWN :
LAYLA	-	SATHEESH
SCALE :	DATE :	CHECKED BY :
NTS @ A1	AUGUST2025	YASEEN
JOB NO :	DRAWING NO. :	REVISION NO. :
——	WS-10	..