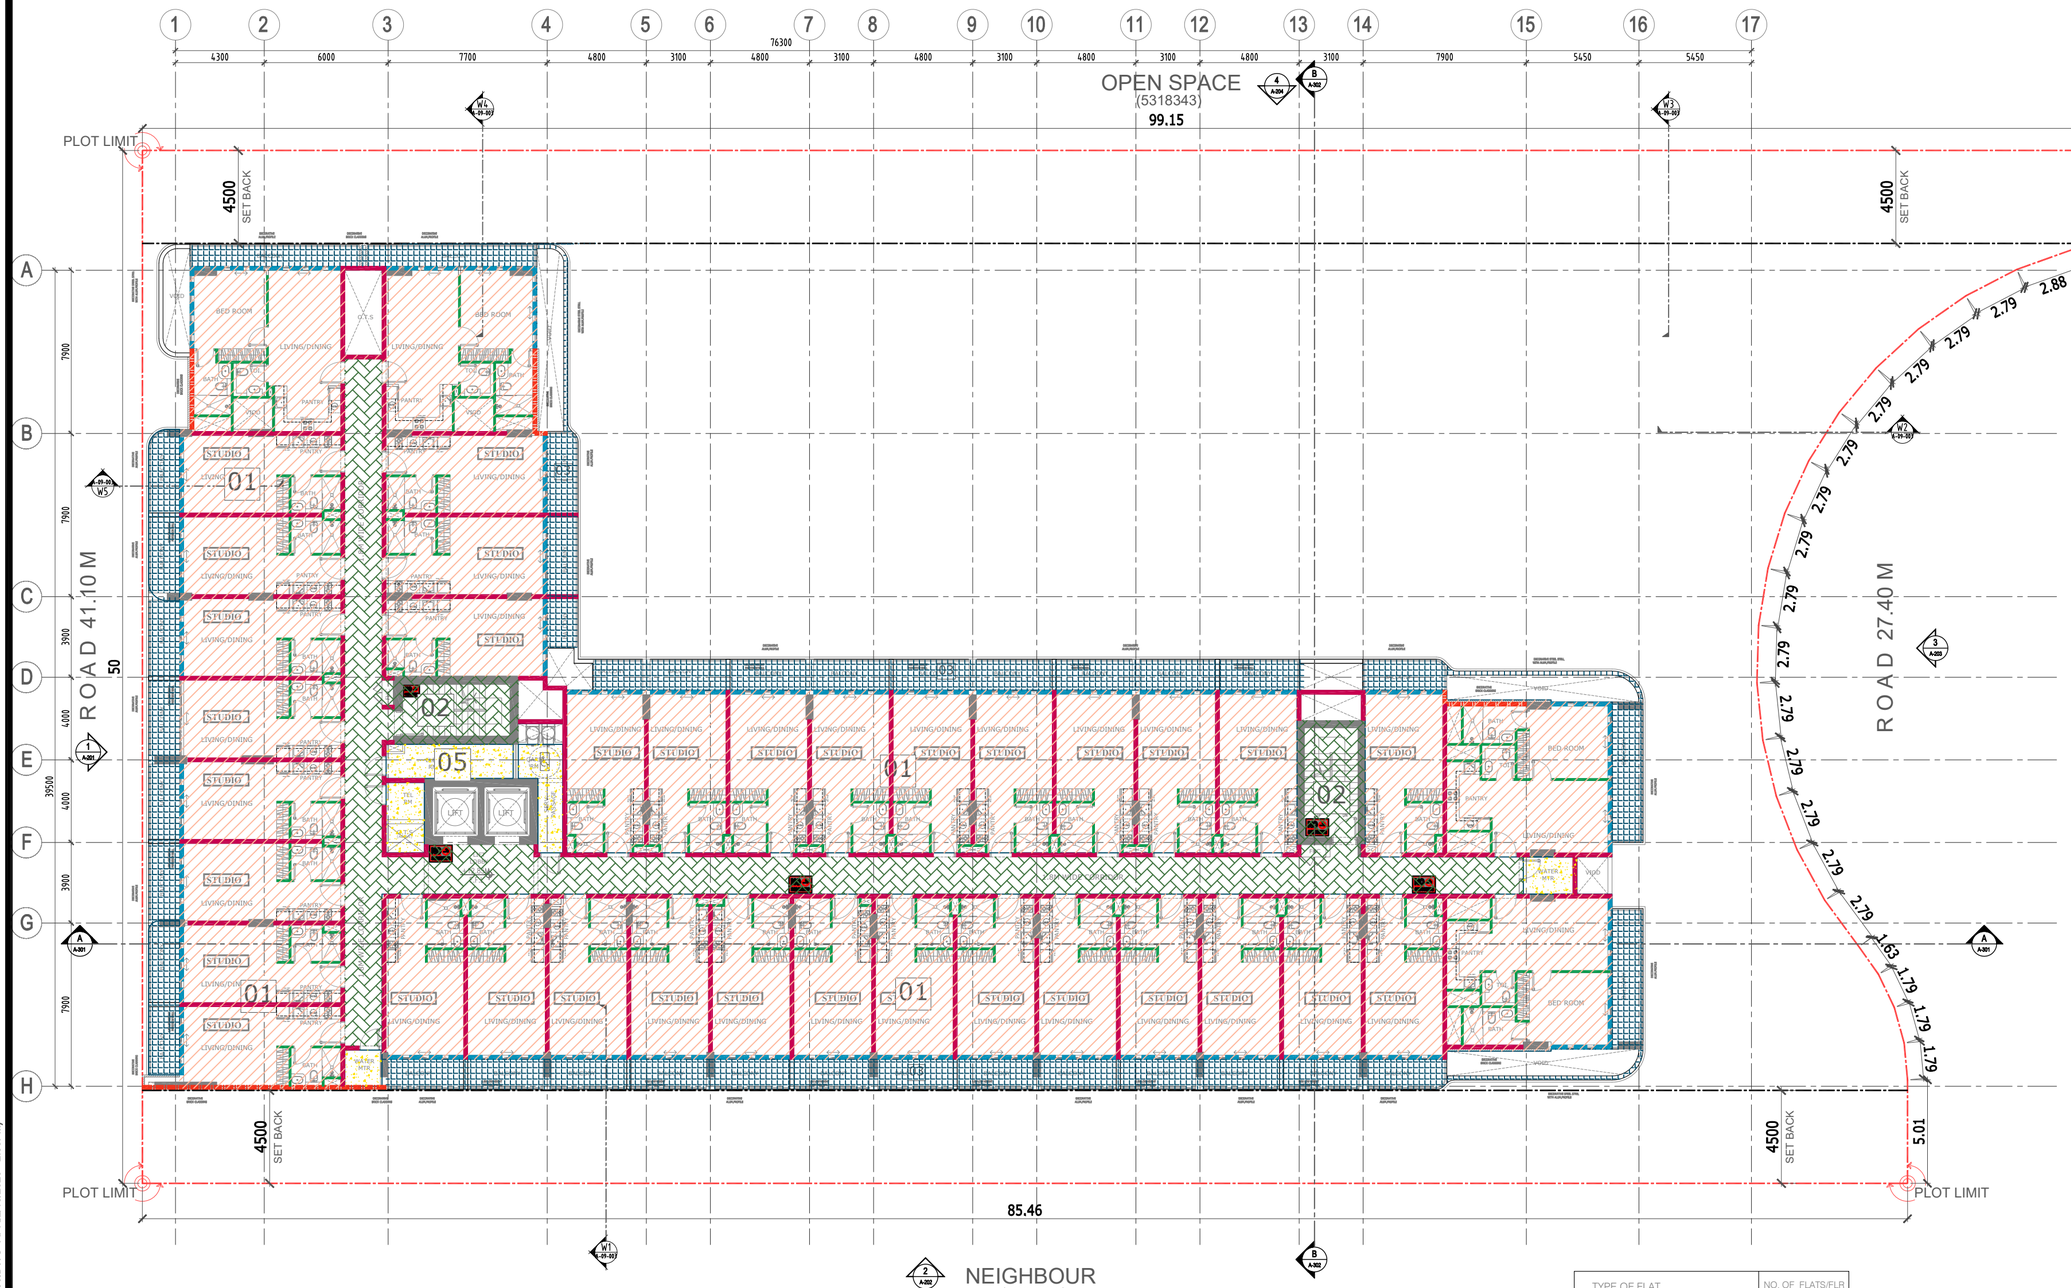


NOTES :

1. THIS DRAWING MAY NOT BE REPRODUCED BY ANY MEANS WITHOUT PRIOR APPROVAL FROM EMSQUARE
2. DRAWINGS ARE NOT TO BE SCALED,STATED DIMENSIONS ONLY ARE TO BE TAKEN.
3. ANY INCONSISTENCY OR DISCRIPANCY IS TO BE BROUGHT TO THE ATTENTION OF & RESOLVED BY THE ARCHITECT/ENGINEER BEFORE THE WORK IS PUT IN HAND.

WALL LEGEND	LENGTH (m)	REMARKS
200 WALL	448.82	AREA 1872.69m²
100 WALL	302.25	
LINE LOAD	4.5 kN/M	GLAZING/PARAPET
LINE LOAD	5 kN/M	BLOCK WORK

AAC* BLOCKS – AUTOCLAVED AERATED BLOCKS WITH DENSITY 500 KG/CUM.

DOOR OPENING (TYPICAL FLOOR)						
NAME	WALL THK.	QUANTITY	LENGTH	HEIGHT	TOTAL m²	SUB TOTAL
D2	0.2	38	1.1	2.4	20.064	20.06
D3	0.1	4	1.0	2.2	0.889	10.45
D4	0.1	42	0.9	2.2	8.455	
D5	0.1	5	1.0	2.2	1.111	
TOTAL AREA OF DOOR						

TYPE OF FLAT	NO. OF FLATS/FLR
TOTAL	38 NOS.

3RD FLOOR PLAN

1

DATE	DESCRIPTION	REV.	BY
13.04.2026	FOR AUTHORITY APPROVAL	00	MS

CONSULTANT :

EMSQUARE ENGINEERING CONSULTANTS
ARCHITECTS-CIVIL ENGINEERS-INTERIORS
P.O. Box 181903, Tel: +971 4 2729009, Fax: +971 4 2729334
Email: emsquare@emirates.net.ae

OWNER :

G F S REAL ESTATE L.L.C

JOB TITLE :

PROPOSED RESIDENTIAL BUILDING (B+G+5+ROOF)

PLOT NO. / PARCEL ID	BLOCK / COMMUNITY
5310319	SAIH SHUAIB 2

DRAWING TITLE : THIRD FLOOR LOADING LAYOUT

ARCHITECT :	STRUCTURAL ENGR. :	DRAWN :
SHAFI	Eng.Vincent	MUFADDAL
SCALE :	DATE :	CHECKED BY :
1:150	13.04.2026	Eng.Vincent
JOB NO :	DRAWING NO. :	REVISION NO. :
—	L-01_6	

PRINTED BY : USER-4,-STRUCTURE GFS B+G+5+ROOF R00.DWG -APRIL/13/2026 - 2:56PM)