
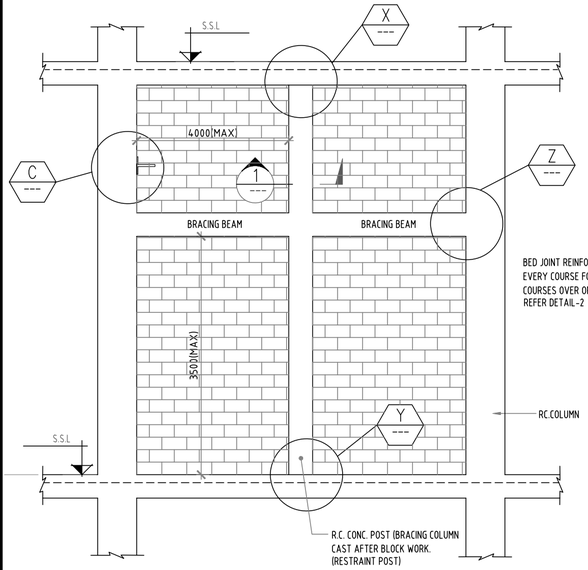



TYP. NON LOAD BEARING WALL PANEL WITHOUT OPENING AND VERTICAL FACES CONFINED BY COLUMNS / BONDED RETAIN WALLS

(SCALE NTS)

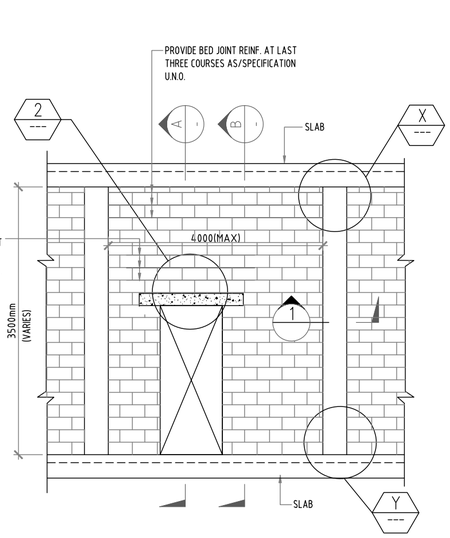


TYP. NON LOAD BEARING WALL NOT CONFINED BY COLUMNS/LONG WALLS

(SCALE NTS)

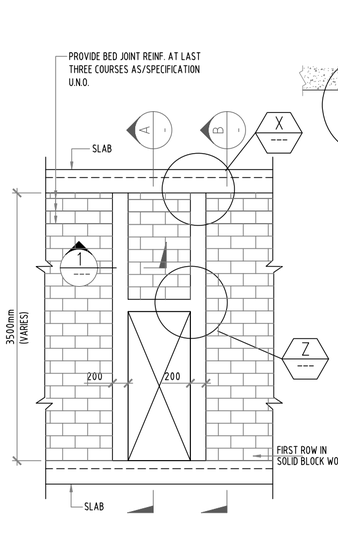

TYP. STIFFENER COLUMN AROUND DOOR OPENINGS FOR AAC BLOCK WORK

(SCALE NTS)

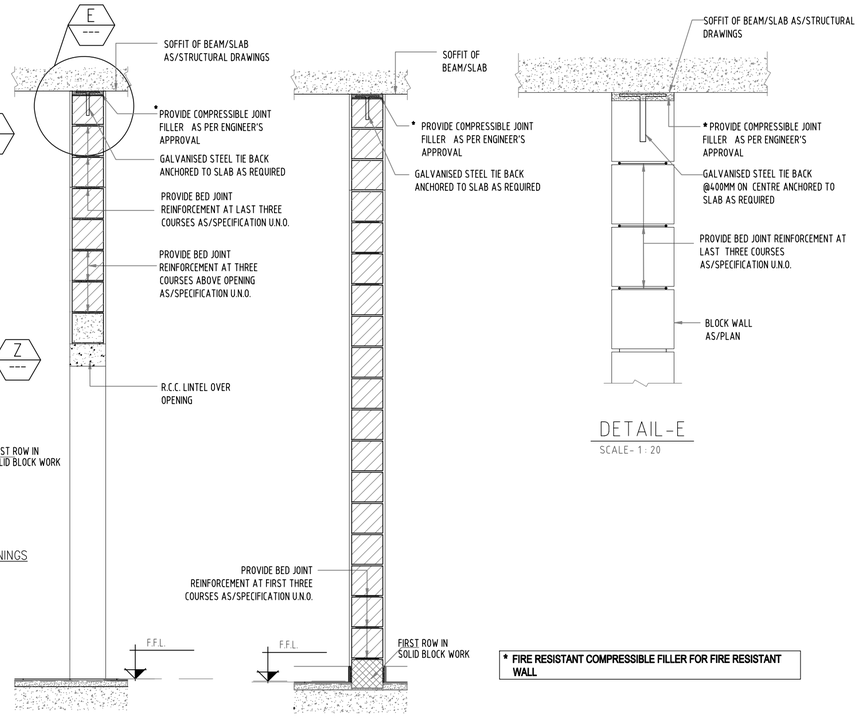

DETAIL-E

SCALE- 1 : 20


A SECTION

SCALE- 1 : 20

B SECTION


SCALE- 1 : 20

*** FIRE RESISTANT COMPRESSIBLE FILLER FOR FIRE RESISTANT WALL**

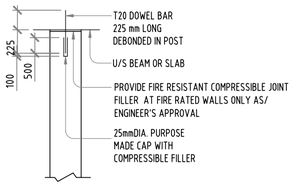


DETAIL-X

(SCALE NTS)

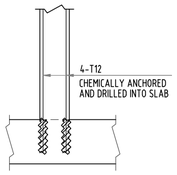

DETAIL-Y


(SCALE NTS)

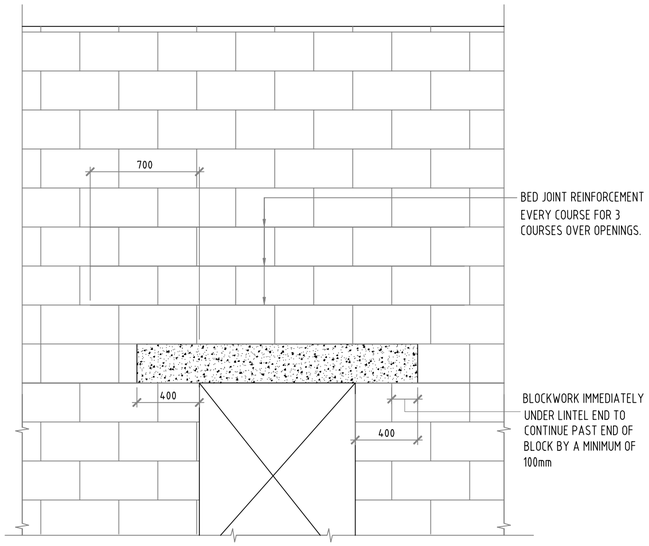

DETAIL-2


(DETAILS OPENING ABOVE)

(SCALE 1:25)

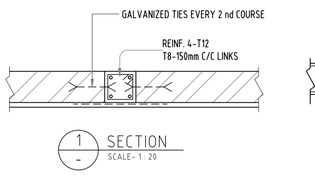


1 SECTION

SCALE- 1 : 20

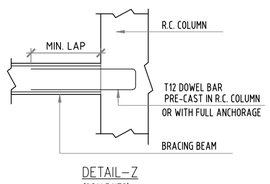

DETAIL-Z


(SCALE NTS)

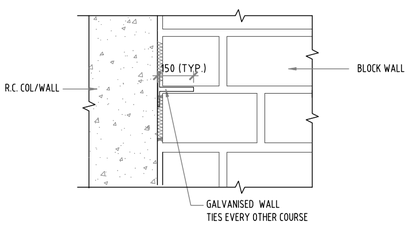


DETAIL AT INTERFACE WITH CONCRETE FRAME

DETAIL-C

SCALE- NTS

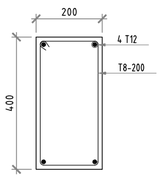


TYPICAL DETAIL OF BRACING BEAM (U.N.O)

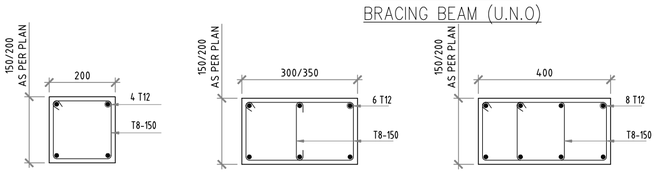


NOTE:
VERTICAL BARS SHALL BE FULLY ANCHORED CHEMICALLY OR BY OTHER MEANS INTO SUPPORTING SLAB

TYPICAL DETAIL OF BRACING COLUMNS (U.N.O)

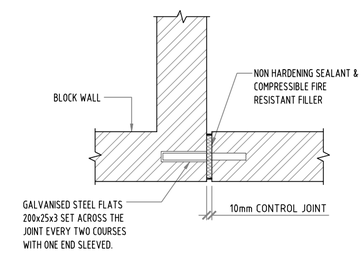


TYP. MOVEMENT JOINT DETAIL

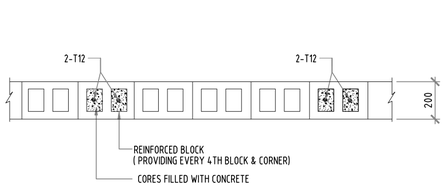


TYPICAL DETAIL OF STRAIGHT REINFORCED BLOCK WALL

SCALE N.T.S.

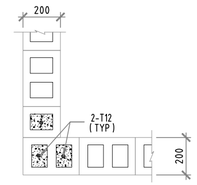


TYPICAL CORNER DETAIL OF REINFORCED BLOCK WALL

SCALE N.T.S.

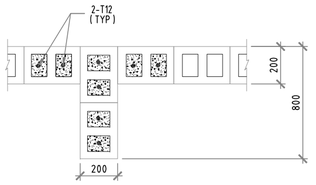


TYPICAL FIN DETAIL OF REINFORCED BLOCK WALL (TYPE-1)

SCALE N.T.S.

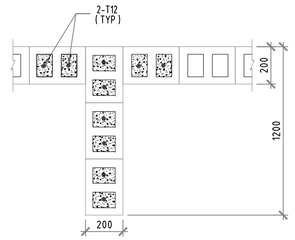

TYPICAL FIN DETAIL OF REINFORCED BLOCK WALL (TYPE-2)

SCALE N.T.S.

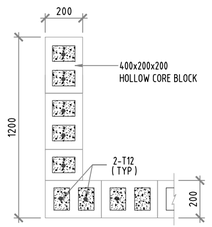

TYPICAL CORNER DETAIL OF REINFORCED BLOCK WALL (TYPE-3)

SCALE N.T.S.

NOTES :

1. THIS DRAWING MAY NOT BE REPRODUCED BY ANY MEANS WITHOUT PRIOR APPROVAL FROM EMSQUARE
2. DRAWINGS ARE NOT TO BE SCALED,STATED DIMENSIONS ONLY ARE TO BE TAKEN.
3. ANY INCONSISTENCY OR DISCRIPANCY IS TO BE BROUGHT TO THE ATTENTION OF & RESOLVED BY THE ARCHITECT/ENGINEER BEFORE THE WORK IS PUT IN HAND.

DATE	DESCRIPTION	REV.	BY
13.04.2026	FOR AUTHORITY APPROVAL	00	MS

CONSULTANT :

EMSQUARE
ENGINEERING CONSULTANTS
ARCHITECTS-CIVIL ENGINEERS-INTERIORS
P.O. Box 181903, Tel: +971 4 2729009, Fax: +971 4 2729334
Email: emsquare@emirates.net.ae

OWNER :

G F S REAL ESTATE L.L.C

JOB TITLE :

PROPOSED RESIDENTIAL BUILDING (B+G+5+ROOF)

PLOT NO. / PARCEL ID	BLOCK / COMMUNITY
5310319	SAIH SHUAIB 2

DRAWING TITLE : STANDARD DETAILS - SHEET-2

ARCHITECT :	STRUCTURAL ENGR. :	DRAWN :
SHAFI	Eng.Vincent	MUFADDAL
SCALE :	DATE :	CHECKED BY :
	13.04.2026	Eng.Vincent
JOB NO :	DRAWING NO. :	REVISION NO. :
—	S-01_2	

PRINTED BY : USER-4.-STRUCTURE GFS B+G+5+ROOF R00.DWG -APRIL/13/2026 - 2:45PM)