

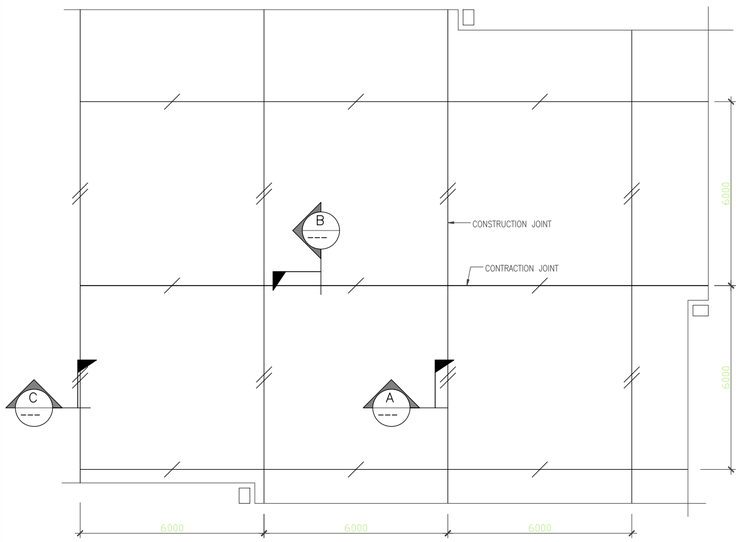



TYPICAL SLAB ON GRADE JOINT DETAIL

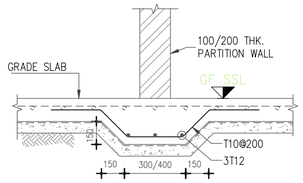


TYP. SLAB THICKENING DETAIL UNDER PARTITION WALL.

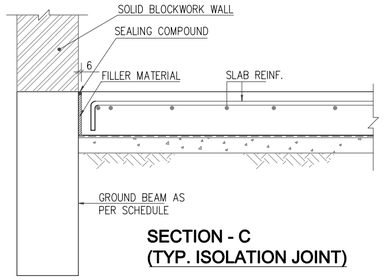

SECTION - C
(TYP. ISOLATION JOINT)

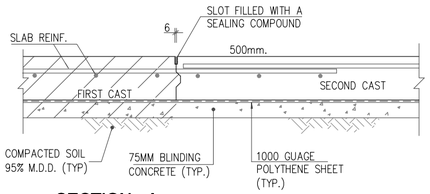


SECTION - A
(TYP. CONSTRUCTION JOINT)

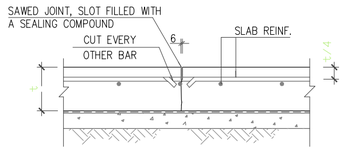


SECTION - B
(TYP. CONTRACTION JOINT)

1 — **TYPICAL SLAB ON GRADE DETAILS**

SCALE: N.T.S

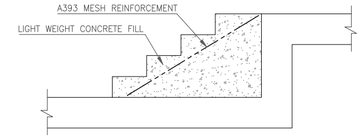

2 — **TYPICAL DETAIL OF STEPS IN FILL**

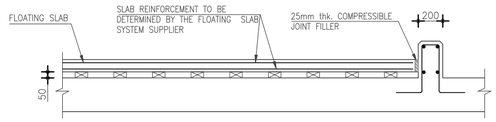

NOTE


1. ALL DETAILS RELATED TO THE FLOATING FLOOR SHALL BE PERFORMED STRICTLY AS PER MANUFACTURES DETAILS
2. SIZE AND LOCATION AS PER ARCHITECTURAL/ MEP DRAWINGS.

3 — **TYPICAL DETAIL OF FLOATING SLAB**

SCALE: N.T.S


NOTES :

1. THIS DRAWING MAY NOT BE REPRODUCED BY ANY MEANS WITHOUT PRIOR APPROVAL FROM EMSQUARE
2. DRAWINGS ARE NOT TO BE SCALED,STATED DIMENSIONS ONLY ARE TO BE TAKEN.
3. ANY INCONSISTENCY OR DISCRIPANCY IS TO BE BROUGHT TO THE ATTENTION OF & RESOLVED BY THE ARCHITECT/ENGINEER BEFORE THE WORK IS PUT IN HAND.

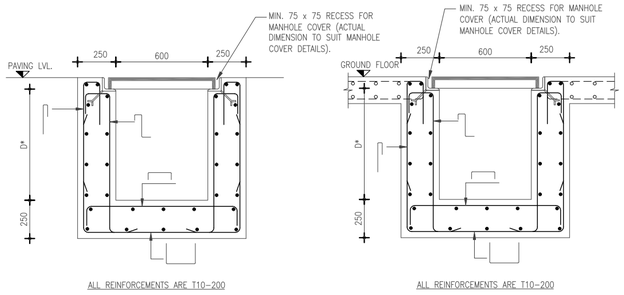


4 — **TYPICAL MANHOLE DETAIL**


NOT:- TO BE CONFIRMED AS PER FINAL

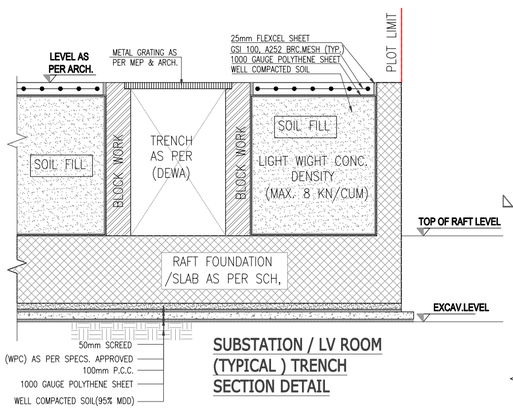

SUBSTATION / LV ROOM
(TYPICAL) TRENCH
SECTION DETAIL

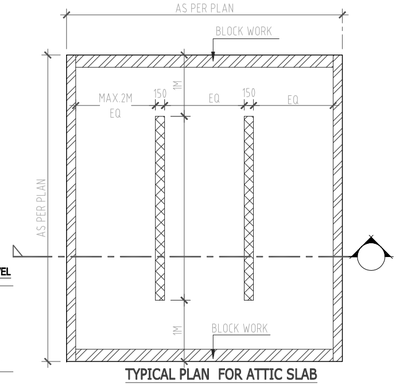


TYPICAL PLAN FOR ATTIC SLAB

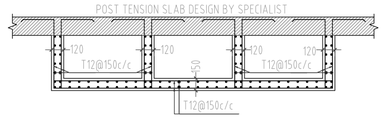


TYPICAL PLAN FOR ATTIC SLAB

NOT:- IN CASE OF SUSPENDED SLAB,TO BE VERIFIED WITH STRUCTURAL ENG. WITH ACTUAL SLAB OPENING AS PER DEWA/AUTHORITY FOR FINAL

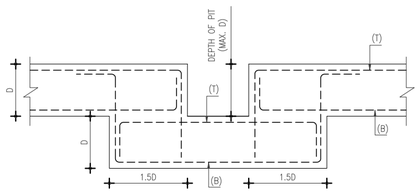

5A — **TYPE - 1**

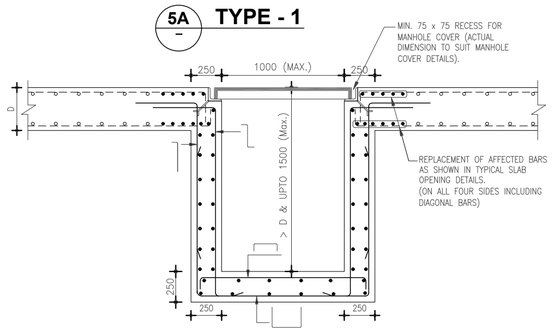

ALL PIT SLAB & WALL REBARS ARE T10-125

5B — **TYPE - 2**

5 — **TYPICAL MANHOLE / SUMP DETAIL IN BASEMENT SLAB**

NOT:- TO BE CONFIRMED AS PER FINAL

13.04.2026	FOR AUTHORITY APPROVAL	00	MS
DATE	DESCRIPTION	REV.	BY

CONSULTANT :

EMSQUARE
ENGINEERING CONSULTANTS
ARCHITECTS-CIVIL ENGINEERS-INTERIORS
P.O. Box 181903, Tel: +971 4 2729009, Fax: +971 4 2729334
Email: emsquare@emirates.net.ae

OWNER :

G F S REAL ESTATE L.L.C

JOB TITLE :

PROPOSED RESIDENTIAL BUILDING (B+G+5+ROOF)

PLOT NO. / PARCEL ID	BLOCK / COMMUNITY
5310319	SAIH SHUAIB 2

DRAWING TITLE : STANDARD DETAILS - SHEET-4

ARCHITECT :	STRUCTURAL ENGR. :	DRAWN :
SHAFI	Eng.Vincent	MUFADDAL
SCALE :	DATE :	CHECKED BY :
NTS	13.04.2026	Eng.Vincent
JOB NO :	DRAWING NO. :	REVISION NO. :
—	S-01_4	

PRINTED BY :USER-4.-STRUCTURE GFS B+G+5+ROOF R00.DWG -APRIL(13/2026 - 2:46PM)