
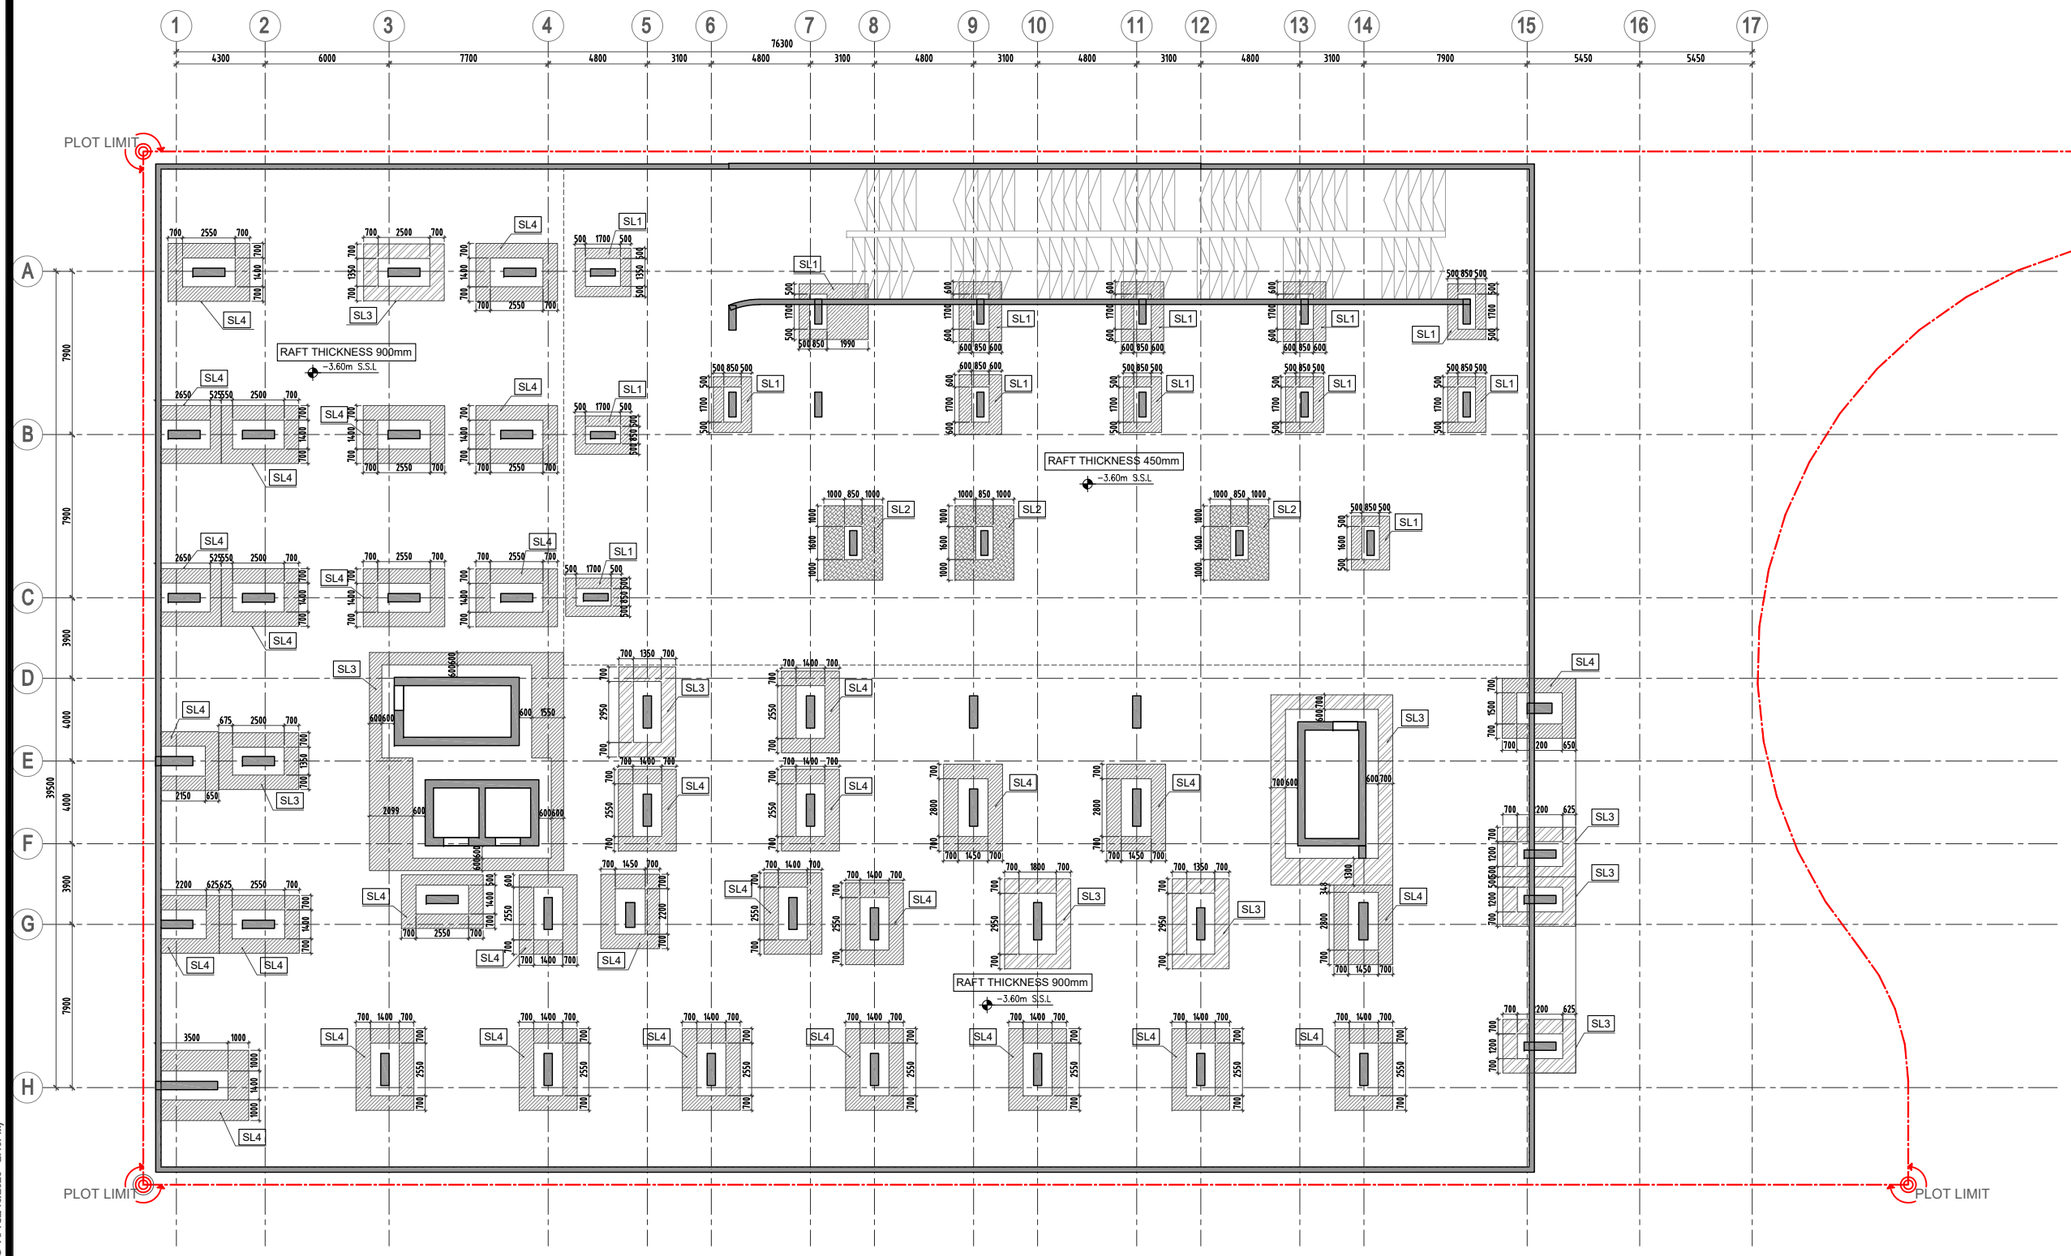


SCHEDULE OF SHEAR LINK			SPACING
MARK	LEGEND	SHEAR LINKS	
SL1		T10@200 B/W	
SL2		T10@200 B/W	
SL3		T12@150 B/W	
SL4		T12@120 B/W	

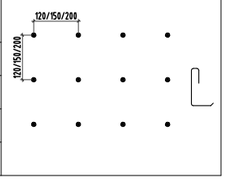

COLUMN LEGEND	
COLUMN CONTINUING	
COLUMN STOPPING	
COLUMN STARTING	

NOTES :
1. THIS DRAWING MAY NOT BE REPRODUCED BY ANY MEANS WITHOUT PRIOR APPROVAL FROM EMSQUARE
2. DRAWINGS ARE NOT TO BE SCALED,STATED DIMENSIONS ONLY ARE TO BE TAKEN.
3. ANY INCONSISTENCY OR DISCRIPANCY IS TO BE BROUGHT TO THE ATTENTION OF & RESOLVED BY THE ARCHITECT/ENGINEER BEFORE THE WORK IS PUT IN HAND.

DATE	DESCRIPTION	REV.	BY
13.04.2026	FOR AUTHORITY APPROVAL	00	MS

CONSULTANT :

EMSQUARE
ENGINEERING CONSULTANTS
ARCHITECTS-CIVIL ENGINEERS-INTERIORS
P.O. Box 182503, Tel: +971 4 2720020, Fax: +971 4 2720204
Email: emsquare@emirates.net.ae

OWNER :

G F S REAL ESTATE L.L.C

JOB TITLE :

PROPOSED RESIDENTIAL BUILDING (B+G+5+ROOF)

PLOT NO. / PARCEL ID	BLOCK / COMMUNITY
5310319	SAIH SHUAIB 2

DRAWING TITLE : FOUNDATION SHEAR LINK LAYOUT

ARCHITECT :	STRUCTURAL ENGR. :	DRAWN :
SHAFI	Eng.Vincent	MUFADDAL
SCALE :	**DATE :**	**CHECKED BY :**
1:150	13.04.2026	Eng.Vincent
JOB NO :	**DRAWING NO. :**	**REVISION NO. :**
—	S-02_8	

PRINTED BY :USER-4.-STRUCTURE GFS B+G+5+ROOF R00.DWG -APRIL/13/2026 - 2:46PM)