

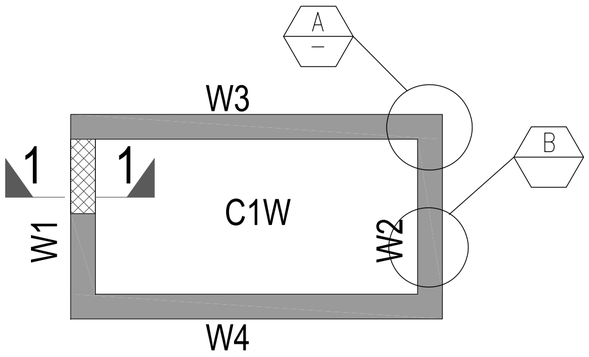


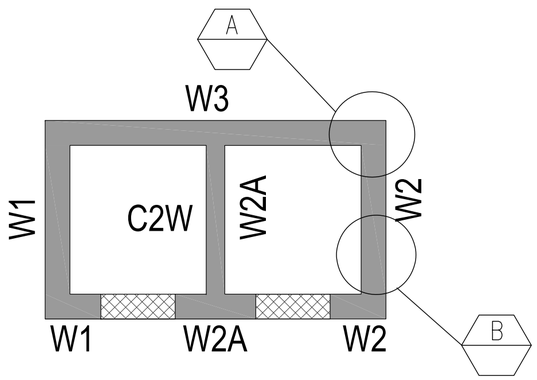

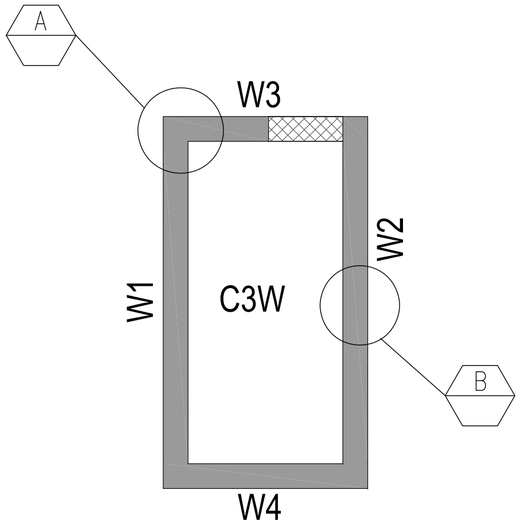

TYPICAL RC WALL DETAILS


SCALE 1:100


L ROOF TO U ROOF FL.	50	400	T16@70	T12@150	400	T16@70	T12@120	400	T16@100	T12@150	400	T20@100	T12@150
4TH TO L ROOF FL.	50	400	T20@70	T12@150	400	T16@70	T12@120	400	T16@100	T12@150	400	T20@100	T12@150
2ND TO 4TH FL.	50	450	T20@70	T12@100	400	T16@70	T12@100	400	T20@100	T12@120	400	T20@100	T12@150
1ST TO 2ND FL.	50	450	T25@70	T12@100	400	T20@70	T12@100	400	T25@100	T12@120	400	T20@100	T12@150
GROUND TO 1ST FL.	50	450	T25@70	T12@80	400	T25@70	T12@120	400	T25@100	T12@100	400	T20@100	T12@120
RAFT TO GROUND FL.	50	450	T25@70	T12@80	400	T25@70	T12@100	400	T25@100	T12@100	400	T20@100	T12@100
FLOOR LEVEL	CONC. GRADE (MPa)	THICKNESS (mm)	VERTICAL BARS	HORIZONTAL BARS	THICKNESS(mm)	VERTICAL BARS	HORIZONTAL BARS	THICKNESS(mm)	VERTICAL BARS	HORIZONTAL BARS	THICKNESS(mm)	VERTICAL BARS	HORIZONTAL BARS
C1W		W1			W2			W3			W4		

L ROOF TO U ROOF FL.	50	400	T16@140	T16@80	400	T16@100	T16@100	400	T16@100	T12@150	300/400	T16@100	T12@150
4TH TO L ROOF FL.	50	400	T16@70	T12@110	400	T16@100	T12@120	400	T16@100	T12@150	300/400	T16@100	T12@150
2ND TO 4TH FL.	50	400	T20@70	T12@110	400	T16@100	T12@120	400	T16@100	T12@150	300/400	T20@100	T12@150
1ST TO 2ND FL.	50	400	T25@70	T12@110	400	T20@100	T12@120	400	T20@100	T12@150	300/400	T25@100	T12@120
GROUND TO 1ST FL.	50	400	T25@70	T12@80	400	T25@100	T12@100	400	T20@100	T12@150	300/400	T25@100	T12@120
RAFT TO GROUND FL.	50	400	T25@70	T12@80	400	T25@100	T12@100	400	T20@100	T12@150	300/400	T25@100	T12@120
FLOOR LEVEL	CONC. GRADE (MPa)	THICKNESS (mm)	VERTICAL BARS	HORIZONTAL BARS	THICKNESS (mm)	VERTICAL BARS	HORIZONTAL BARS	THICKNESS (mm)	VERTICAL BARS	HORIZONTAL BARS	THICKNESS (mm)	VERTICAL BARS	HORIZONTAL BARS
C2W		W1			W2			W3			W2A		

L ROOF TO U ROOF FL.	50	250	T16@150	T12@200	350	T16@100	T12@200	350	T16@160	T12@80	350	T16@100	T12@200
4TH TO L ROOF FL.	50	350	T16@100	T12@200	350	T16@100	T12@150	350	T16@80	T12@80	350	T16@100	T12@150
2ND TO 4TH FL.	50	350	T16@100	T12@150	350	T16@100	T12@150	350	T20@80	T12@80	350	T20@100	T12@150
1ST TO 2ND FL.	50	350	T20@100	T12@150	350	T20@100	T12@150	350	T25@80	T12@80	350	T25@100	T12@120
GROUND TO 1ST FL.	50	350	T25@100	T12@120	350	T20@100	T12@120	400	T25@80	T12@100	350	T25@100	T12@120
RAFT TO GROUND FL.	50	350	T25@100	T12@120	350	T20@100	T12@120	400	T25@80	T16@100	350	T25@100	T12@120
FLOOR LEVEL	CONC. GRADE (MPa)	THICKNESS (mm)	VERTICAL BARS	HORIZONTAL BARS	THICKNESS (mm)	VERTICAL BARS	HORIZONTAL BARS	THICKNESS (mm)	VERTICAL BARS	HORIZONTAL BARS	THICKNESS (mm)	VERTICAL BARS	HORIZONTAL BARS
C3W		W1			W2			W3			W4		


L ROOF TO U ROOF FL.	50	----	----	----	300	T16@50	T12@120
4TH TO L ROOF FL.	50	300	T20@100	T12@200	----	----	----
2ND TO 4TH FL.	50	300	T20@100	T12@150	----	----	----
1ST TO 2ND FL.	50	300	T20@100	T12@150	----	----	----
GROUND TO 1ST FL.	50	400	T20@100	T12@120	----	----	----
RAFT TO GROUND FL.	50	400	T20@100	T12@120	----	----	----
FLOOR LEVEL	CONC. GRADE (MPa)	THICKNESS (mm)	VERTICAL BARS	HORIZONTAL BARS	THICKNESS (mm)	VERTICAL BARS	HORIZONTAL BARS
		W1			PW1		

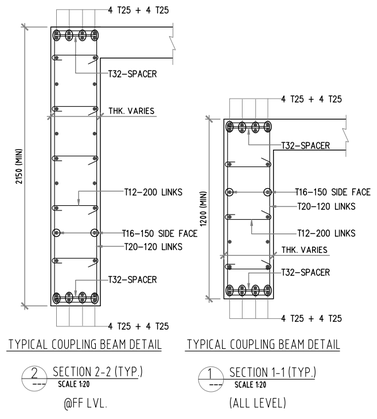


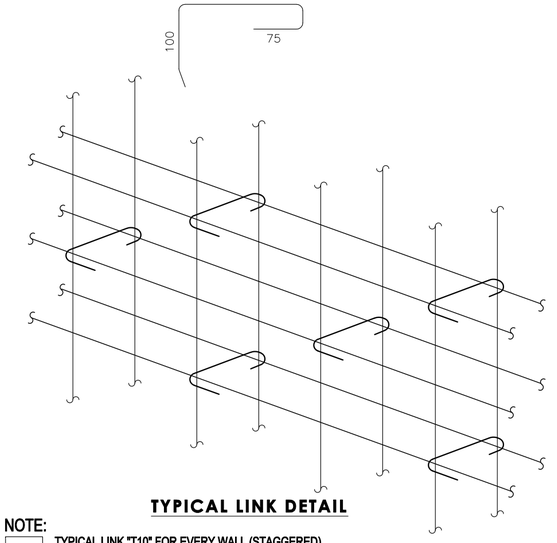

NOTE:

TYPICAL LINK "T10" FOR EVERY WALL (STAGGERED)
THE SPACING BETWEEN LINKS WILL FOLLOW THE SPACING BETWEEN VERTICAL AND HORIZONTAL REINFORCEMENT, THE LINKS ARE ARRANGED EVERY OTHER BARS.

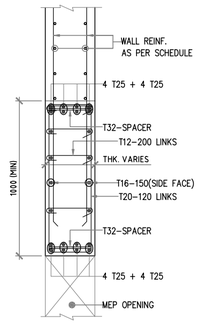

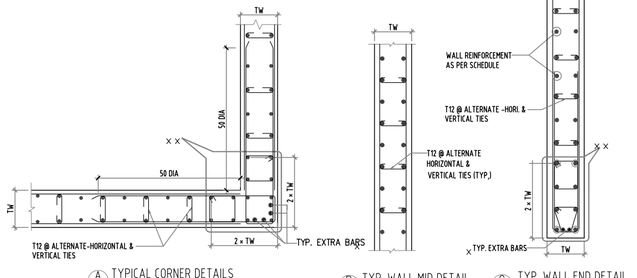

x DIA OF EXTRA BARS~~S~~ HIGHER DIA OF EITHER WALL
NO. OF EXTRA BARS~~S~~ 1 No. FOR UPTO 300mm THK. WALL.
2 Nos. FOR WALL MORE THAN 300mm THICK.

x x NEXT LARGER DIA OF VERT. REINF. AS PER SCHEDULE

NOTES :
1. THIS DRAWING MAY NOT BE REPRODUCED BY ANY MEANS WITHOUT PRIOR APPROVAL FROM EMSQUARE
2. DRAWINGS ARE NOT TO BE SCALED,STATED DIMENSIONS ONLY ARE TO BE TAKEN.
3. ANY INCONSISTENCY OR DISCRIPANCY IS TO BE BROUGHT TO THE ATTENTION OF & RESOLVED BY THE ARCHITECT/ENGINEER BEFORE THE WORK IS PUT IN HAND.

DATE	DESCRIPTION	REV.	BY
13.04.2026	FOR AUTHORITY APPROVAL	00	MS

CONSULTANT :

EMSQUARE
ENGINEERING CONSULTANTS
ARCHITECTS-CIVIL ENGINEERS-INTERIORS
P.O. Box 181903, Tel: +971 4 2729009, Fax: +971 4 2729334
Email: emsquare@emirates.net.ae

OWNER :

G F S REAL ESTATE L.L.C

JOB TITLE :

PROPOSED RESIDENTIAL BUILDING (B+G+5+ROOF)

PLOT NO. / PARCEL ID	BLOCK / COMMUNITY
5310319	SAIH SHUAIB 2

DRAWING TITLE :

CORE WALL DETAILS

ARCHITECT :	STRUCTURAL ENGR. :	DRAWN :
SHAFI	Eng.Vincent	MUFADDAL
SCALE :	**DATE :**	**CHECKED BY :**
1:50	13.04.2026	Eng.Vincent
JOB NO :	**DRAWING NO. :**	**REVISION NO. :**
—	S-04_3	

PRINTED BY :USER-4-:STRUCTURE GFS B+G+5+ROOF R00.DWG -APRIL/13/2026 - 2:52PM)