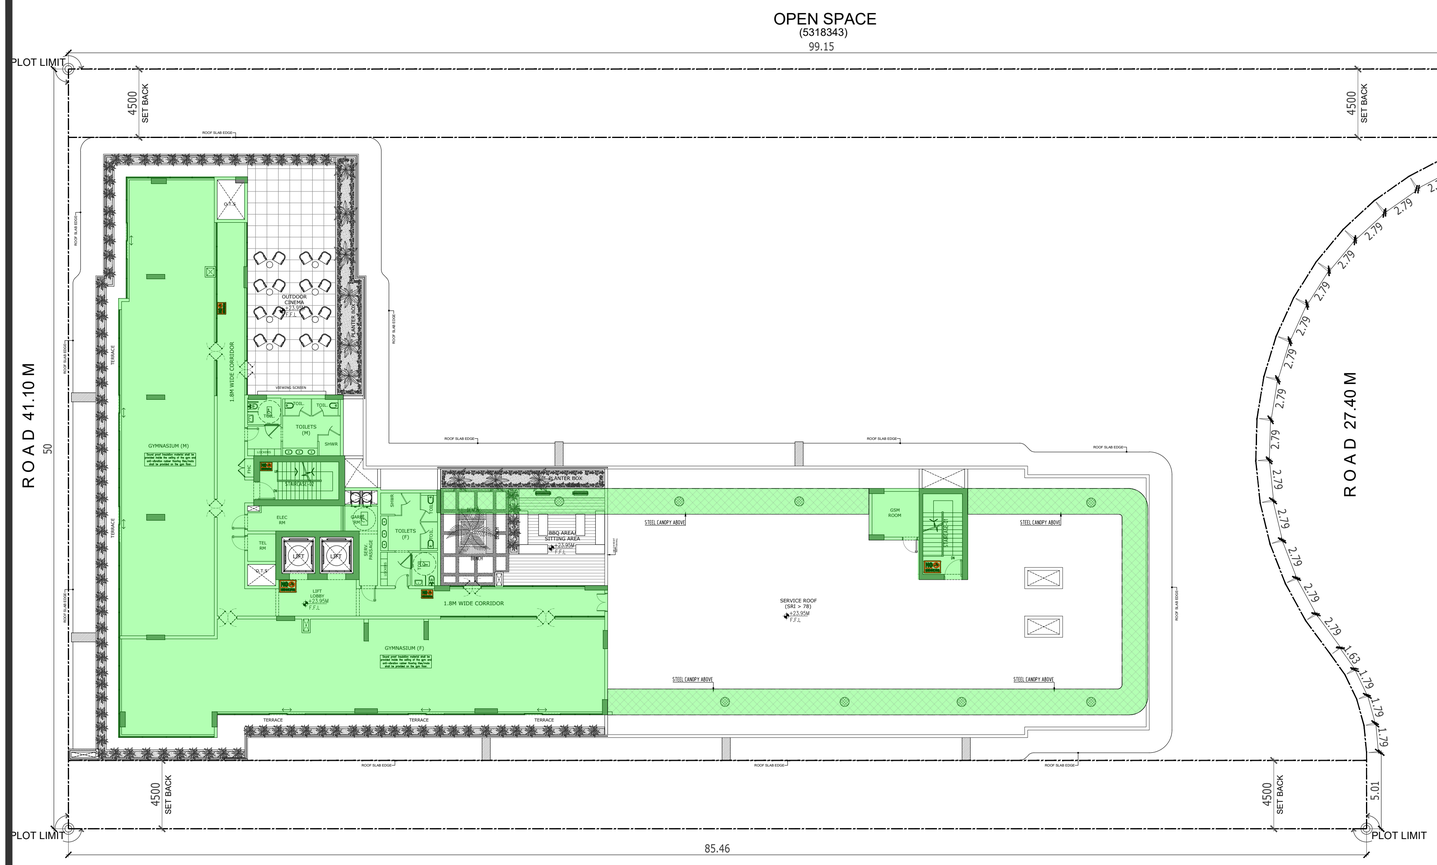


LOWER ROOF COVERAGE CALCULATION

TOTAL AREA OF COVERAGE (INCLUDING CANOPY AREA)	**786.17 SQMT**	**8,462.22SQ.FT.**

SUMMARY OF CALCULATION

FLOOR PLATE AREA = 1,791.68 SQ.M (19,285.47 SQ.FT)

ALLOWED GYMNASIUM AREA = 50% OF ROOF AREA
= 50% OF 1,791.68 SQ.M (19,285.47 SQ.FT)
= 894.45 SQ.M (9627.83 SQ.FT)

PROPOSED GYMNASIUM AREA	=786.17 SQ.M (8,462.22 SQ.FT) **= 43.92% OF FLOOR PLATE AREA**

LIFT CALCULATION (RESIDENTIAL)

POPULATION ESTIMATION (RESIDENTIAL)

APARTMENT TYPE	OCCUPANCY RATE (PERSONS)	POPULATION
STUDIO FLAT	1.5	1.5 X 165 = 247.5
1BED ROOM FLAT	1.8	1.8 X 20 = 36
2BED ROOM FLAT	--	--
TOTAL POPULATION		283.50

A - NUMBER OF LIFT REQUIRED (POPULATION ≤283.50 OCCUPIED FLOORS 1- 5) = 1 NO.S
B - NUMBER OF LIFT REQUIRED (WITH BOARDING FLOORS 2 & OCCUPIED FLOORS 1- 5) = 0 NO.S
TOTAL NUMBER OF LIFT REQUIRED = A+B = 1 + 0 = 1NO.S
TOTAL NUMBER OF LIFT PROPOSED = 02NO.S (PASSENGER LIFT)

MAXIMUM TRAVEL DISTANCE - 35.30 M
LIFT LOBBY WIDTH -7.40, 2.40 M

A- NO. OF LIFTS BASED ON POPULATION

D.8.8.2 Passenger elevator selection charts

The minimum number of passenger elevators shall be determined from Figure D.13.

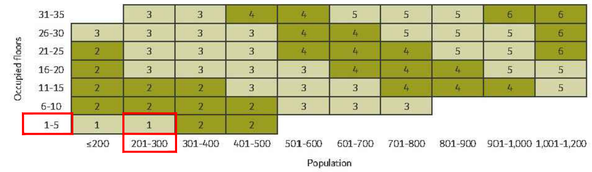


Figure D.13 Elevator chart for population – residential apartments

B - NO. OF LIFTS BASED ON BOARDING FLOORS



(b) for population ≤700

NOTES:

1. THIS DRAWING MAY NOT BE REPRODUCED BY ANY MEANS WITHOUT PRIOR APPROVAL FROM EMSQUARE
2. DRAWINGS ARE NOT TO BE SCALED, STATED DIMENSIONS ONLY ARE TO BE TAKEN.
3. ANY INCONSISTENCY OR DISCRIPANCY IS TO BE BROUGHT TO THE ATTENTION OF & RESOLVED BY THE ARCHITECT/ENGINEER BEFORE THE WORK IS PUT IN HAND.

DATE	DESCRIPTION	BY

CONSULTANT :
EMSQUARE
ENGINEERING CONSULTANTS
ARCHITECTS-CIVIL ENGINEERS-INTERIORS
P.O. Box 181903, Tel: +971 4 2729009, Fax: +971 4 2729334
Email: emsquare@emirates.net.ae

OWNER :
G F S REAL ESTATE L.L.C

JOB TITLE :
PROPOSED RESIDENTIAL BUILDING (B+G+5+ROOF)

PLOT NO. / PARCEL ID	BLOCK / COMMUNITY
5310319	SAIH SHUAIB 2

DRAWING TITLE :
AREA CALCULATION-4

ARCHITECT :	STRUCTURAL ENGR. :	DRAWN :
SMITHA		SHAFI
SCALE :	DATE :	CHECKED BY :
	JUN-2025	BABU
JOB NO :	DRAWING NO. :	REVISION NO. :
—	A-03-004	--

: D:\ANJU PROJECTS 2023\PROJECTS\GFS\08. 5310319 - COVENTRY RESIDENCE 3 - G F S REAL ESTATE L.L.C\FINAL SUBMISSION\FINAL AUTHORITY SUB\ARCH\CAD\A-03-001TOA-03-004 AREA CALCULATION.dwg