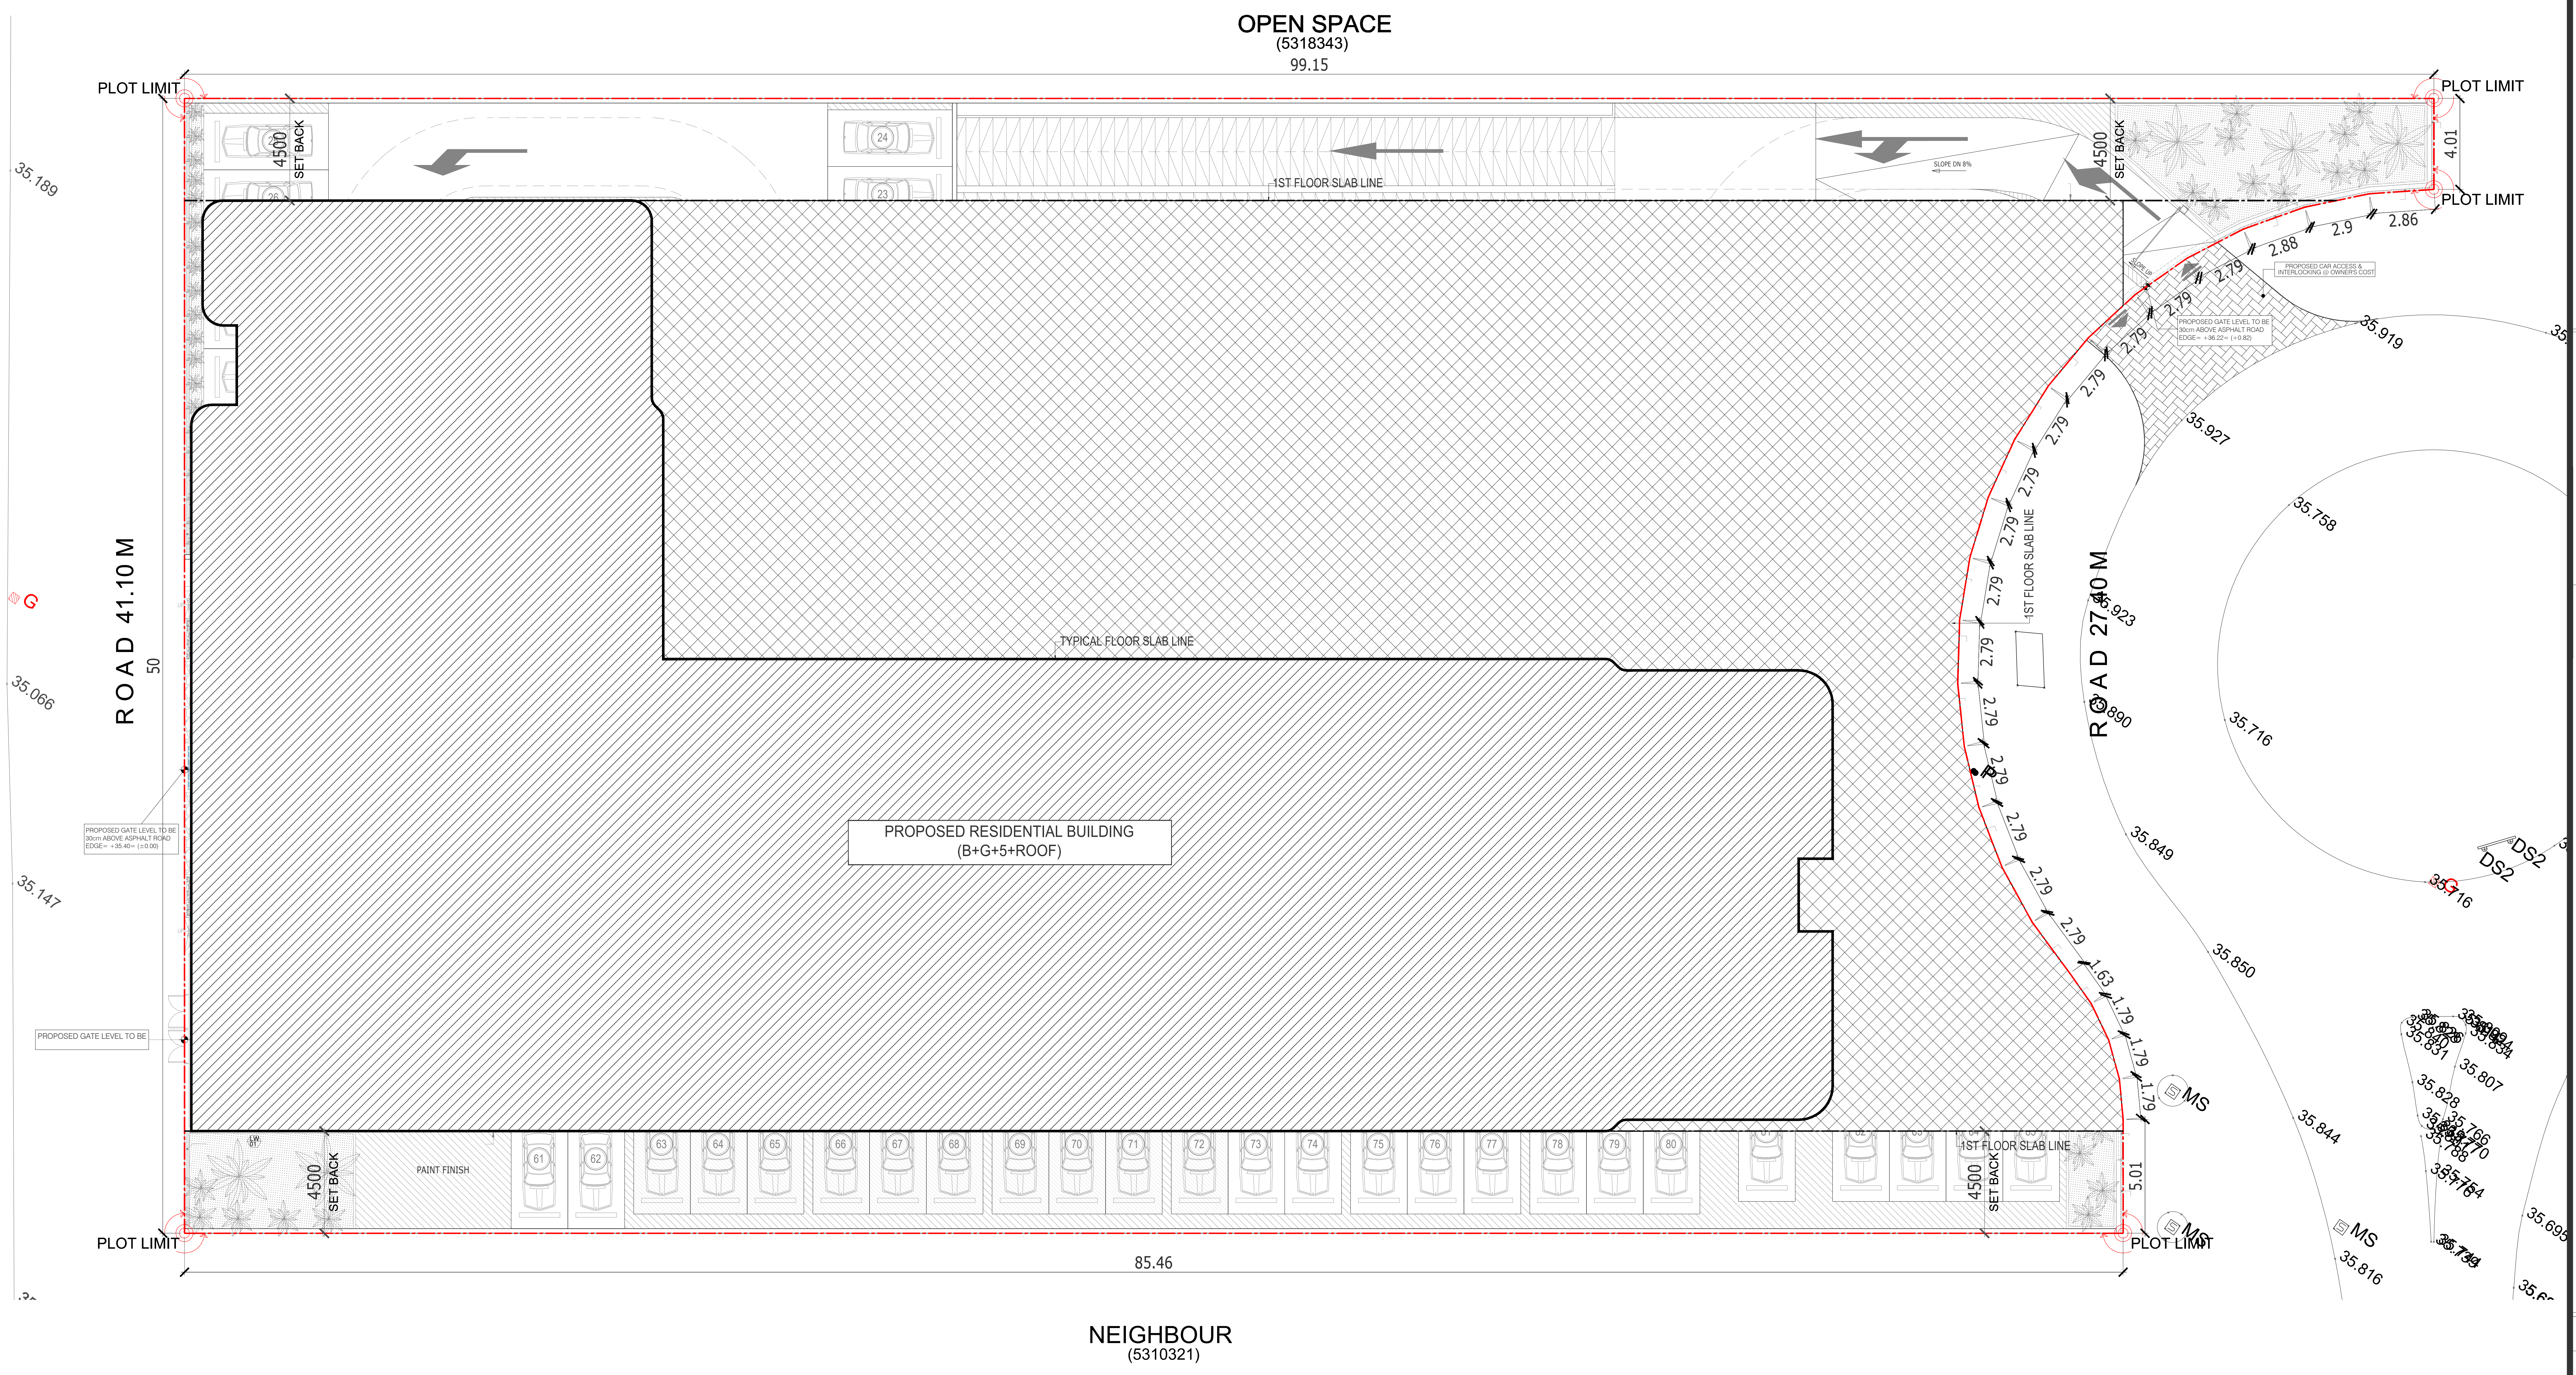

NOTES:

1. THIS DRAWING MAY NOT BE REPRODUCED BY ANY MEANS WITHOUT PRIOR APPROVAL FROM EMSQUARE
2. DRAWINGS ARE NOT TO BE SCALED, STATED DIMENSIONS ONLY ARE TO BE TAKEN.
3. ANY INCONSISTENCY OR DISCRIPANCY IS TO BE BROUGHT TO THE ATTENTION OF & RESOLVED BY THE ARCHITECT/ENGINEER BEFORE THE WORK IS PUT IN HAND.

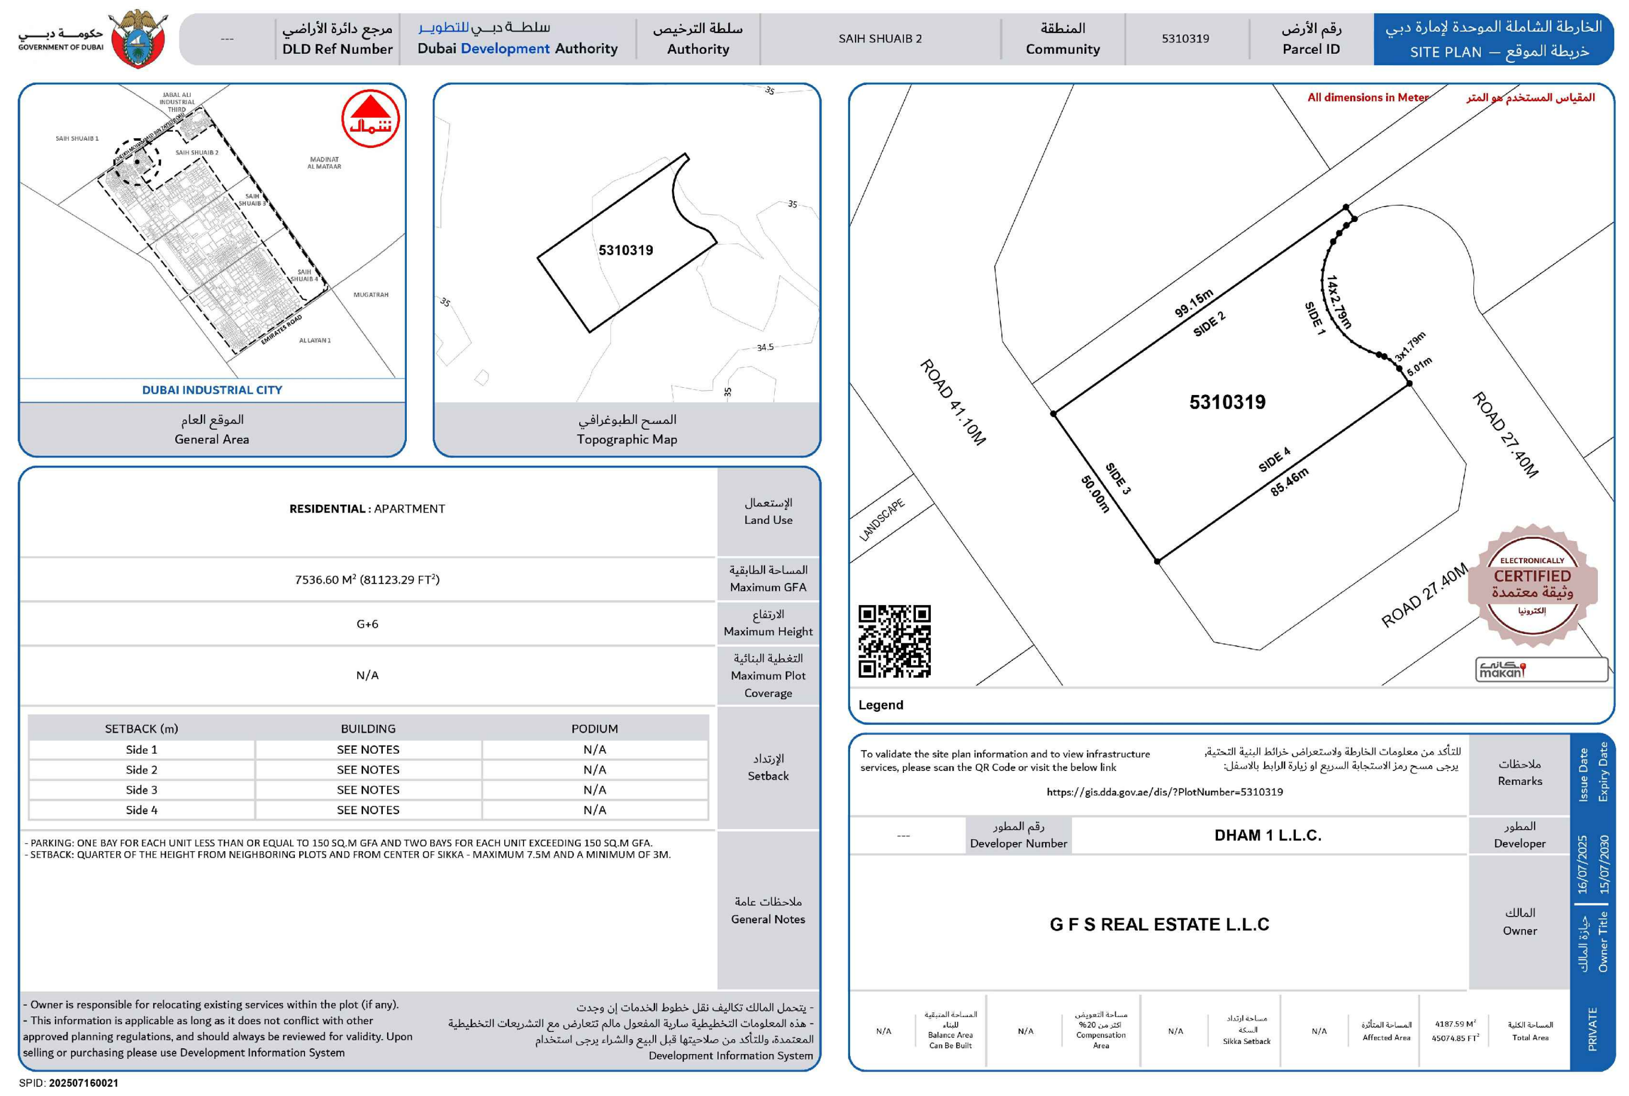

حكومــة دبــي
GOVERNMENT OF DUBAI

---	مرجع دائرة الأراضي DLD Ref Number	سلطـة دبـي للتطويـر Dubai Development Authority	سلطة الترخيص Authority	SAIH SHUAIB 2	المنطقة Community	5310319	رقم الأرض Parcel ID	الخارطة الشاملة الموحدة لإمارة دبي SITE PLAN – خريطة الموقع

DUBAI INDUSTRIAL CITY

الموقع العام
General Area

المسح الطبوغرافي
Topographic Map

All dimensions in Meter
المقياس المستخدم هو المتر

5310319
SIDE 1
14x2.79m
3x1.79m
5.01m
SIDE 2
99.15m
SIDE 3
50.00m
SIDE 4
85.46m
ROAD 41.10M
ROAD 27.40M
ROAD 27.40M
LANDSCAPE

ELECTRONICALLY CERTIFIED وثيقة معتمدة إلكترونيا

Legend

RESIDENTIAL : APARTMENT	الإستعمال Land Use
7536.60 M² (81123.29 FT²)	المساحة الطابقية Maximum GFA
G+6	الارتفاع Maximum Height
N/A	التغطية البنائية Maximum Plot Coverage

الإرتداد
Setback

SETBACK (m)	BUILDING	PODIUM
Side 1	SEE NOTES	N/A
Side 2	SEE NOTES	N/A
Side 3	SEE NOTES	N/A
Side 4	SEE NOTES	N/A

ملاحظات عامة
General Notes

- PARKING: ONE BAY FOR EACH UNIT LESS THAN OR EQUAL TO 150 SQ.M GFA AND TWO BAYS FOR EACH UNIT EXCEEDING 150 SQ.M GFA.
- SETBACK: QUARTER OF THE HEIGHT FROM NEIGHBORING PLOTS AND FROM CENTER OF SIKKA - MAXIMUM 7.5M AND A MINIMUM OF 3M.

- Owner is responsible for relocating existing services within the plot (if any).
- This information is applicable as long as it does not conflict with other approved planning regulations, and should always be reviewed for validity. Upon selling or purchasing please use Development Information System

- يتحمل المالك تكاليف نقل خطوط الخدمات إن وجدت
- هذه المعلومات التخطيطية سارية المفعول مالم تتعارض مع التشريعات التخطيطية المعتمدة، وللتأكد من صلاحيتها قبل البيع والشراء يرجى استخدام Development Information System

To validate the site plan information and to view infrastructure services, please scan the QR Code or visit the below link

للتأكد من معلومات الخارطة واستعراض خرائط البنية التحتية، يرجى مسح رمز الاستجابة السريع او زيارة الرابط بالاسفل:

https://gis.dda.gov.ae/dis/?PlotNumber=5310319

ملاحظات
Remarks

---	رقم المطور Developer Number	DHAM 1 L.L.C.	المطور Developer
		G F S REAL ESTATE L.L.C	المالك Owner

Issue Date 16/07/2025
Expiry Date 15/07/2030
حيازة المالك Owner Title
PRIVATE

N/A	المساحة المتبقية للبناء Balance Area Can Be Built	N/A	مساحة التعويض أكثر من 20% Compensation Area	N/A	مساحة ارتداد السكة Sikka Setback	N/A	المساحة المتأثرة Affected Area	4187.59 M² 45074.85 FT²	المساحة الكلية Total Area

SPID: 202507160021

AFFECTION PLAN

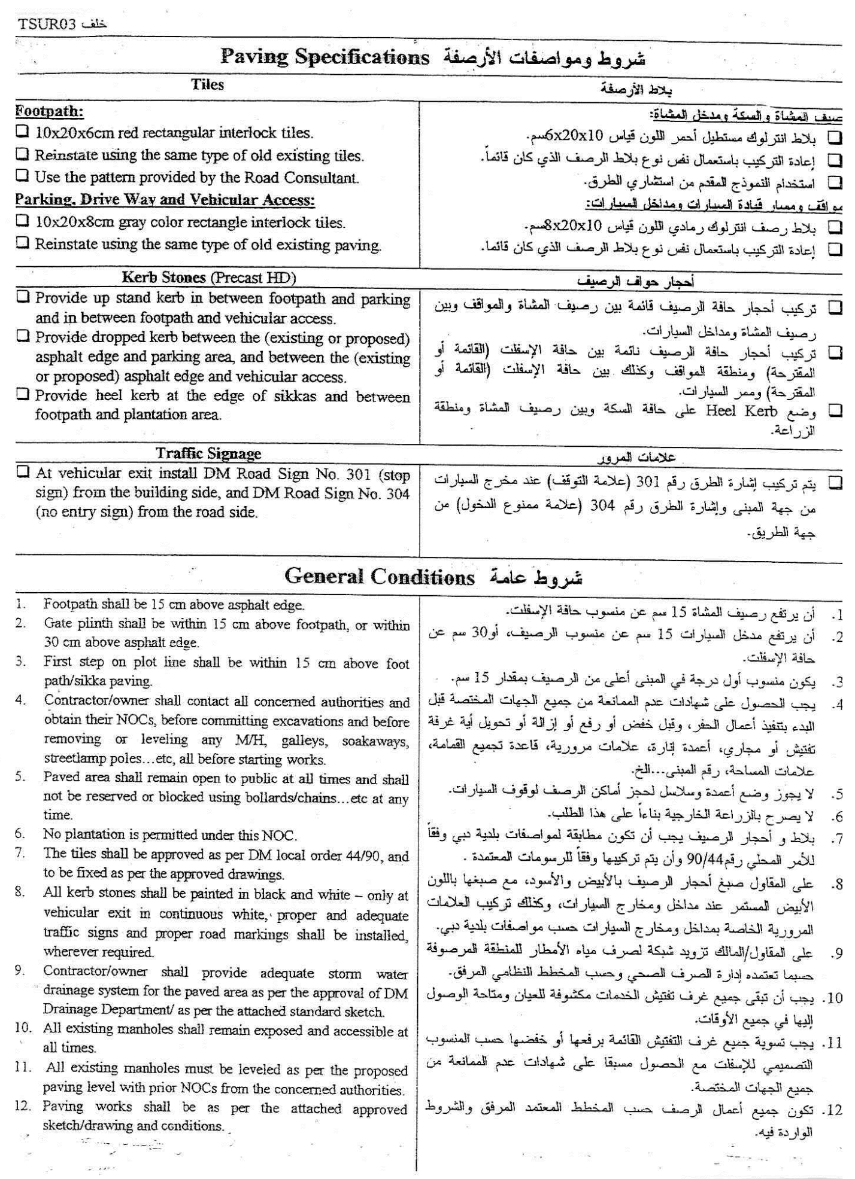

TSUR03 خلف

Paving Specifications شروط ومواصفات الأرصفة

Tiles	بلاط الأرصفة
Footpath:	رصيف المشاة والسكة ومدخل المشاة:
☐ 10x20x6cm red rectangular interlock tiles.	☐ بلاط انترلوك مستطيل أحمر اللون قياس 10x20x6سم.
☐ Reinstate using the same type of old existing tiles.	☐ إعادة التركيب باستعمال نفس نوع بلاط الرصف الذي كان قائماً.
☐ Use the pattern provided by the Road Consultant.	☐ استخدام النموذج المقدم من استشاري الطرق.
Parking, Drive Way and Vehicular Access:	مواقف وممار قيادة السيارات ومداخل السيارات:
☐ 10x20x8cm gray color rectangle interlock tiles.	☐ بلاط رصف انترلوك رمادي اللون قياس 10x20x8سم.
☐ Reinstate using the same type of old existing paving.	☐ إعادة التركيب باستعمال نفس نوع بلاط الرصف الذي كان قائما.

Kerb Stones (Precast HD)	أحجار حواف الرصيف
☐ Provide up stand kerb in between footpath and parking and in between footpath and vehicular access.	☐ تركيب أحجار حافة الرصيف قائمة بين رصيف المشاة والمواقف وبين رصيف المشاة ومداخل السيارات.
☐ Provide dropped kerb between the (existing or proposed) asphalt edge and parking area, and between the (existing or proposed) asphalt edge and vehicular access.	☐ تركيب أحجار حافة الرصيف نائمة بين حافة الإسفلت (القائمة أو المقترحة) ومنطقة المواقف وكذلك بين حافة الإسفلت (القائمة أو المقترحة) وممر السيارات.
☐ Provide heel kerb at the edge of sikkas and between footpath and plantation area.	☐ وضع Heel Kerb على حافة السكة وبين رصيف المشاة ومنطقة الزراعة.

Traffic Signage	علامات المرور
☐ At vehicular exit install DM Road Sign No. 301 (stop sign) from the building side, and DM Road Sign No. 304 (no entry sign) from the road side.	☐ يتم تركيب إشارة الطرق رقم 301 (علامة التوقف) عند مخرج السيارات من جهة المبنى وإشارة الطرق رقم 304 (علامة ممنوع الدخول) من جهة الطريق.

General Conditions شروط عامة

1. Footpath shall be 15 cm above asphalt edge.	1. أن يرتفع رصيف المشاة 15 سم عن منسوب حافة الإسفلت.
2. Gate plinth shall be within 15 cm above footpath, or within 30 cm above asphalt edge.	2. أن يرتفع مدخل السيارات 15 سم عن منسوب الرصيف، أو30 سم عن حافة الإسفلت.
3. First step on plot line shall be within 15 cm above foot path/sikka paving.	3. يكون منسوب أول درجة في المبنى أعلى من الرصيف بمقدار 15 سم.
4. Contractor/owner shall contact all concerned authorities and obtain their NOCs, before committing excavations and before removing or leveling any M/H, galleys, soakaways, streetlamp poles…etc, all before starting works.	4. يجب الحصول على شهادات عدم الممانعة من جميع الجهات المختصة قبل البدء بتنفيذ أعمال الحفر، وقبل خفض أو رفع أو إزالة أو تحويل أية غرفة تفتيش أو مجاري، أعمدة إنارة، علامات مرورية، قاعدة تجميع القمامة، علامات المساحة، رقم المبنى...الخ.
5. Paved area shall remain open to public at all times and shall not be reserved or blocked using bollards/chains…etc at any time.	5. لا يجوز وضع أعمدة وسلاسل لحجز أماكن الرصف لوقوف السيارات.
6. No plantation is permitted under this NOC.	6. لا يصرح بالزراعة الخارجية بناءاً على هذا الطلب.
7. The tiles shall be approved as per DM local order 44/90, and to be fixed as per the approved drawings.	7. بلاط و أحجار الرصيف يجب أن تكون مطابقة لمواصفات بلدية دبي وفقاً للأمر المحلي رقم44/90 وأن يتم تركيبها وفقاً للرسومات المعتمدة.
8. All kerb stones shall be painted in black and white – only at vehicular exit in continuous white, proper and adequate traffic signs and proper road markings shall be installed, wherever required.	8. على المقاول صبغ أحجار الرصيف بالأبيض والأسود، مع صبغها باللون الأبيض المستمر عند مداخل ومخارج السيارات، وكذلك تركيب العلامات المرورية الخاصة بمداخل ومخارج السيارات حسب مواصفات بلدية دبي.
9. Contractor/owner shall provide adequate storm water drainage system for the paved area as per the approval of DM Drainage Department/ as per the attached standard sketch.	9. على المقاول/المالك تزويد شبكة لصرف مياه الأمطار للمنطقة المرصوفة حسبما تعتمده إدارة الصرف الصحي وحسب المخطط النظامي المرفق.
10. All existing manholes shall remain exposed and accessible at all times.	10. يجب أن تبقى جميع غرف تفتيش الخدمات مكشوفة للعيان ومتاحة الوصول إليها في جميع الأوقات.
11. All existing manholes must be leveled as per the proposed paving level with prior NOCs from the concerned authorities.	11. يجب تسوية جميع غرف التفتيش القائمة برفعها أو خفضها حسب المنسوب التصميمي للإسفلت مع الحصول مسبقا على شهادات عدم الممانعة من جميع الجهات المختصة.
12. Paving works shall be as per the attached approved sketch/drawing and conditions.	12. تكون جميع أعمال الرصف حسب المخطط المعتمد المرفق والشروط الواردة فيه.

PAVING SPECIFICATION

REQUIRED
GARBAGE ROOM CALCULATION
- SQ.M. +15% = 31.40 SQ.M.
PROPOSED GARBAGE ROOM AREA
31.40SQ.M.

BULK WASTE AREA PROPOSED 10 SQ.M

PROPOSED GATE
(SOWTH WEST) GATE LEVEL :
GATE LEVEL IS 30 CM ABOVE
THE ASPHALT ROAD LEVEL = (±0.00)

GARBAGE ROOM CALCULATION AS PER GREEN BUILDING REGULATION

HARDSCAPE

ALL INTERLOCK & PAVEMENT MATERIAL ARE WITH SRI 29>

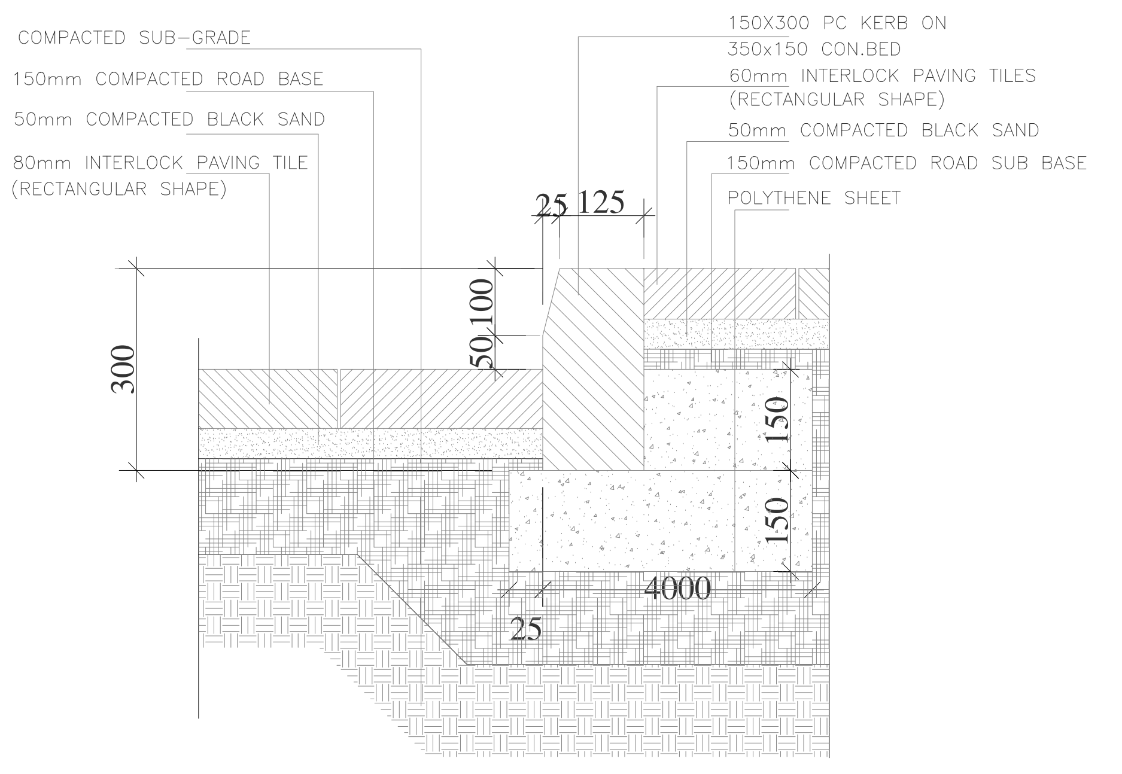
COMPACTED SUB–GRADE
150mm COMPACTED ROAD BASE
50mm COMPACTED BLACK SAND
80mm INTERLOCK PAVING TILE (RECTANGULAR SHAPE)
150X300 PC KERB ON 350x150 CON.BED
60mm INTERLOCK PAVING TILES (RECTANGULAR SHAPE)
50mm COMPACTED BLACK SAND
150mm COMPACTED ROAD SUB BASE
POLYTHENE SHEET
25
125
300
100
50
150
150
4000
25

TYPICAL DETAIL OF KERB STONE

2 A-06-001 TYP.KERB STONE DET.

SCALE -

DATE	DESCRIPTION	BY

CONSULTANT :

EMSQUARE
ENGINEERING CONSULTANTS
ARCHITECTS-CIVIL ENGINEERS-INTERIORS
P.O. Box 181903, Tel: +971 4 2729009, Fax: +971 4 2729334
Email: emsquare@emirates.net.ae

OWNER :

G F S REAL ESTATE L.L.C

JOB TITLE :

PROPOSED RESIDENTIAL BUILDING
(B+G+5+ROOF)

PLOT NO. / PARCEL ID	BLOCK / COMMUNITY
5310319	SAIH SHUAIB 2

DRAWING TITLE :

SETTING OUT PLAN

ARCHITECT :	STRUCTURAL ENGR. :	DRAWN :
SMITHA		**SHAFI**
SCALE :	DATE :	CHECKED BY :
1:100	**JUN-2025**	**BABU**
JOB NO :	DRAWING NO. :	REVISION NO. :
—	A-06-001	--