A-07-001 UNDER GROUND WATER TANK & PUMP ROOM - take-off markup. 23 grid bays matched by label to dimensions stated on other sheets, spread 0.19%; effective scale 1:152.4 (title block 1:125)

TAKE-OFF ON THIS SHEET (trade colours)
H-H D-1: 1 tag(s) here - count OPEN

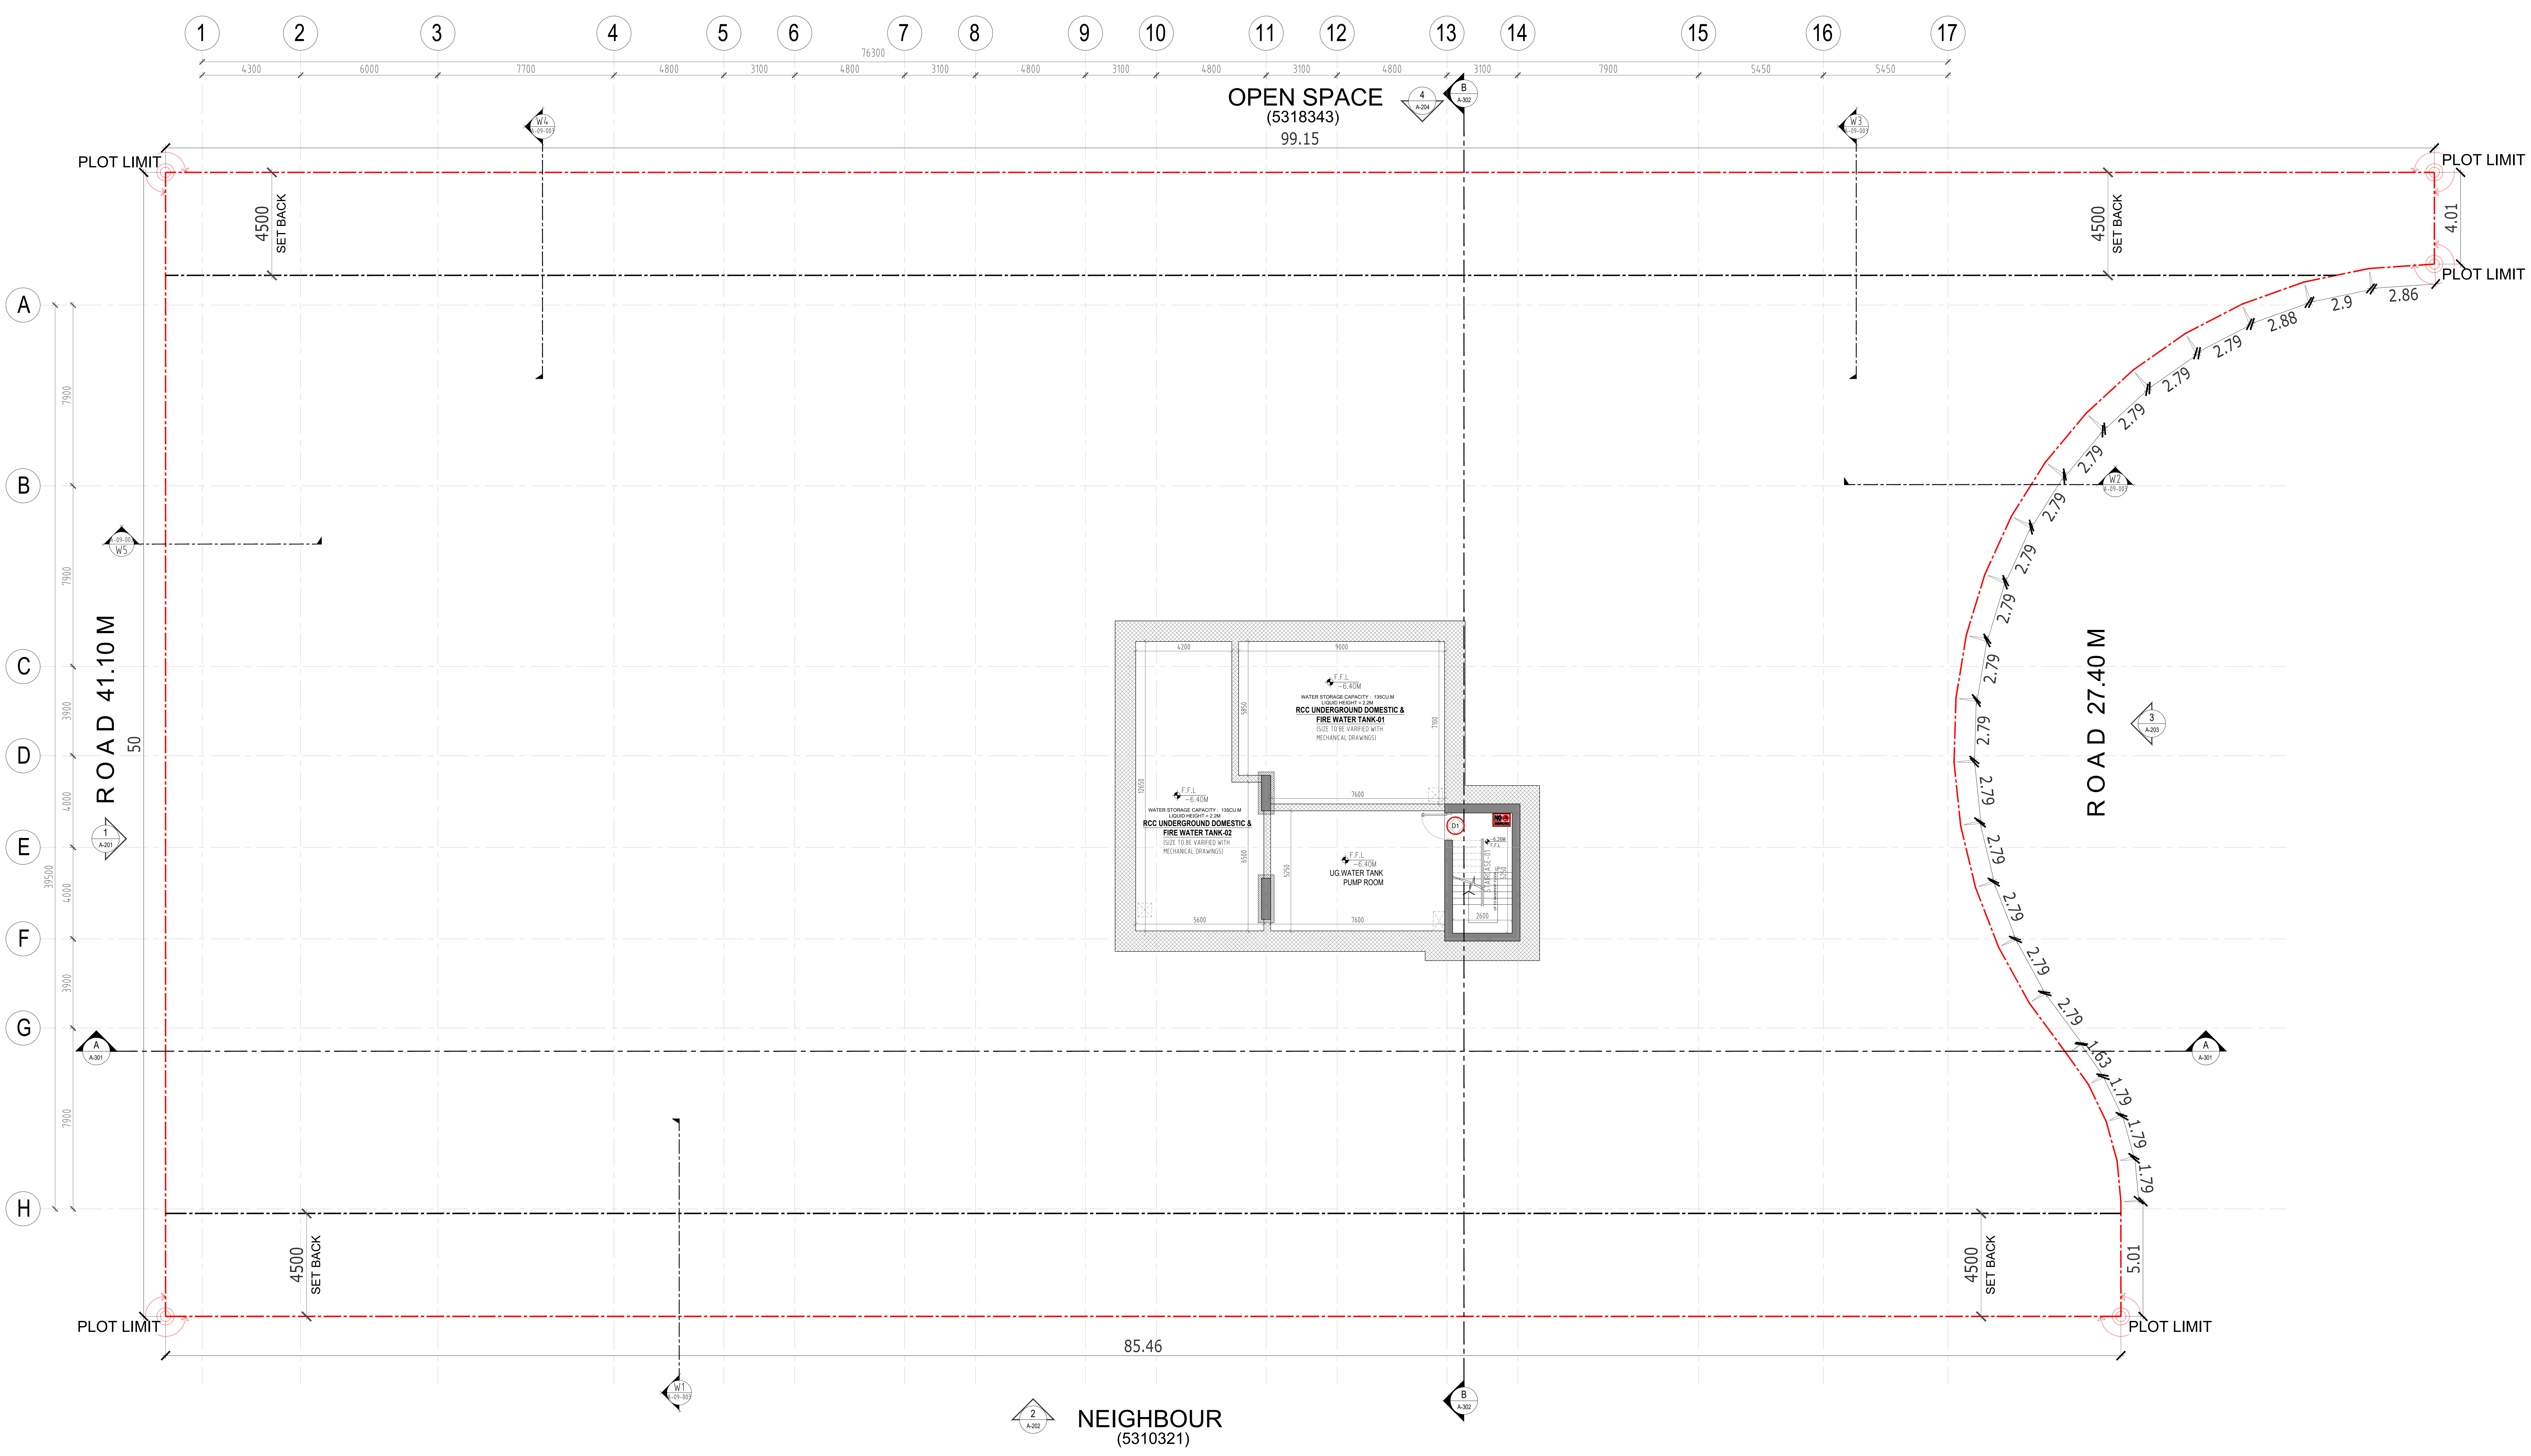
1
2
3
4
5
6
7
8
9
10
11
12
13
14
15
16
17
76300
4300
6000
7700
4800
3100
4800
3100
4800
3100
4800
3100
4800
3100
7900
5450
5450
OPEN SPACE
(5318343)
99.15
PLOT LIMIT
4500
SET BACK
4.01
2.86
2.9
2.88
2.79
1.63
1.79
5.01
A
B
C
D
E
F
G
H
7900
3900
4000
39500
ROAD 41.10 M
50
ROAD 27.40 M
W1
W2
W3
W4
W5
A-301
A-302
A-202
A-203
A-204
A-201
F.F.L
−6.40M
WATER STORAGE CAPACITY : 135CU.M
LIQUID HEIGHT = 2.2M
RCC UNDERGROUND DOMESTIC & FIRE WATER TANK-01
(SIZE TO BE VARIFIED WITH MECHANICAL DRAWINGS)
RCC UNDERGROUND DOMESTIC & FIRE WATER TANK-02
UG.WATER TANK PUMP ROOM
4200
9000
5850
7100
12650
7600
6500
5250
5600
2600
D1
NO SMOKING
−6.26M
STAIRCASE-01
UP
UP TO BASEMENT FLOOR
85.46
NEIGHBOUR
(5310321)

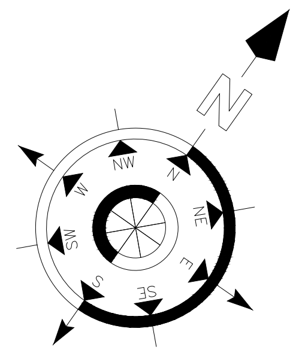

NOTES:

1. THIS DRAWING MAY NOT BE REPRODUCED BY ANY MEANS WITHOUT PRIOR APPROVAL FROM EMSQUARE.
2. DRAWINGS ARE NOT TO BE SCALED, STATED DIMENSIONS ONLY ARE TO BE TAKEN.
3. ANY INCONSISTENCY OR DISCRIPANCY IS TO BE BROUGHT TO THE ATTENTION OF & RESOLVED BY THE ARCHITECT/ENGINEER BEFORE THE WORK IS PUT IN HAND.

DATE	DESCRIPTION	BY

CONSULTANT :

EMSQUARE
ENGINEERING CONSULTANTS
ARCHITECTS-CIVIL ENGINEERS-INTERIORS
P.O. Box 181903, Tel: +971 4 2729009, Fax: +971 4 2729334
Email: emsquare@emirates.net.ae

OWNER :

G F S REAL ESTATE L.L.C

JOB TITLE :

PROPOSED RESIDENTIAL BUILDING
(B+G+5+ROOF)

PLOT NO. / PARCEL ID	BLOCK / COMMUNITY
5310319	SAIH SHUAIB 2

DRAWING TITLE :

UNDER GROUND WATER TANK & PUMP ROOM

ARCHITECT :	STRUCTURAL ENGR. :	DRAWN :
SMITHA		**SHAFI**
SCALE :	DATE :	CHECKED BY :
1:125	**JUN-2025**	**BABU**
JOB NO :	DRAWING NO. :	REVISION NO. :
—	A-07-001	--

: D:\ANJU PROJECTS 2023\PROJECTS\GFS\08. 5310319 - COVENTRY RESIDENCE 3 - G F S REAL ESTATE L.L.C\FINAL SUBMISSION\FINAL AUTHORITY SUB\ARCH\CAD\A-07-001 UNDERGROUND WATER TANK.dwg