A-07-009 UPPER ROOF PLAN - take-off markup. 23 grid bays matched by label to dimensions stated on other sheets, spread 0.19%; effective scale 1:152.4 (title block 1:150)

TAKE-OFF ON THIS SHEET (trade colours)
H-H D-1: 1 tag(s) here - count OPEN
H-Y DW 11: 3 tag(s) here - count CLOSED
H-Z DW 12: 1 tag(s) here - count CLOSED

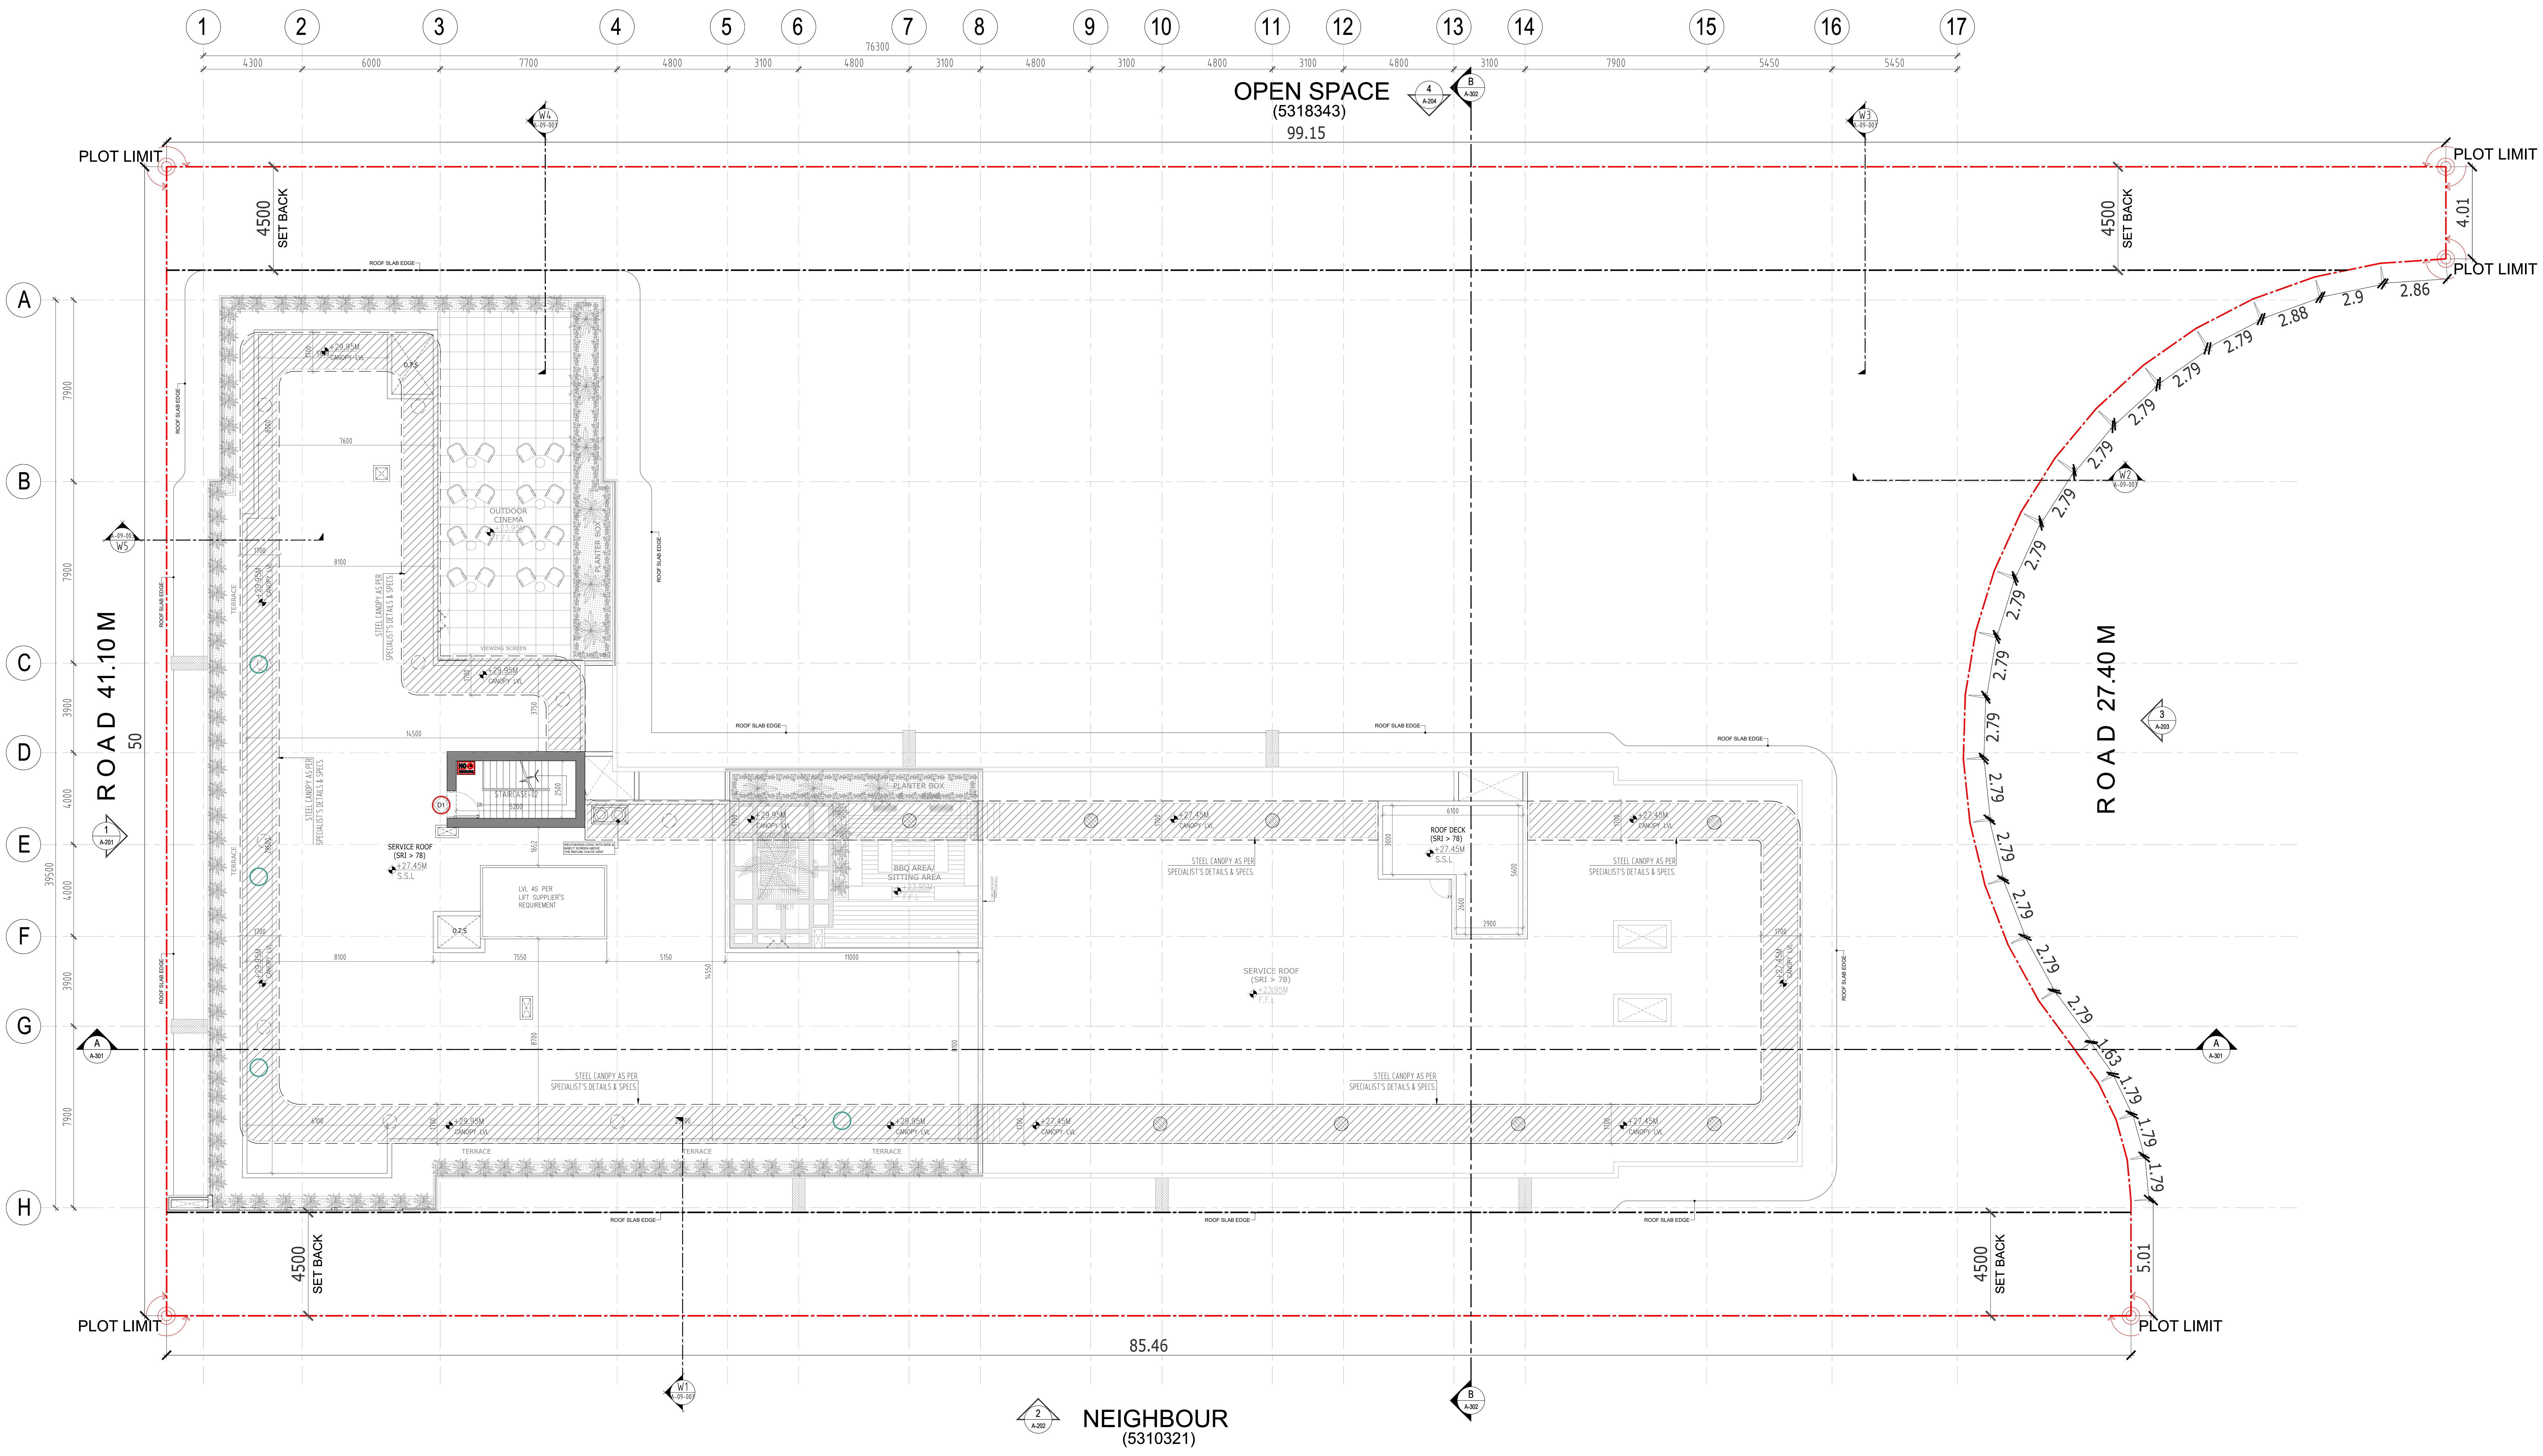
1
2
3
4
5
6
7
8
9
10
11
12
13
14
15
16
17
76300
4300
6000
7700
4800
3100
4800
3100
4800
3100
4800
3100
4800
3100
7900
5450
5450
OPEN SPACE
(5318343)
99.15
PLOT LIMIT
PLOT LIMIT
PLOT LIMIT
PLOT LIMIT
PLOT LIMIT
4500
SET BACK
4500
SET BACK
4500
SET BACK
4500
SET BACK
4.01
2.86
2.9
2.88
2.79
1.63
1.79
5.01
A
B
C
D
E
F
G
H
7900
7900
3900
4000
4000
3900
7900
39500
ROAD 41.10 M
50
ROAD 27.40 M
OUTDOOR CINEMA
PLANTER BOX
STAIRCASE
SERVICE ROOF
BBQ AREA/ SITTING AREA
ROOF DECK
SERVICE ROOF
TERRACE
STEEL CANOPY AS PER SPECIALIST'S DETAILS & SPECS
ROOF SLAB EDGE
85.46
NEIGHBOUR
(5310321)

NOTES:

1. THIS DRAWING MAY NOT BE REPRODUCED BY ANY MEANS WITHOUT PRIOR APPROVAL FROM EMSQUARE
2. DRAWINGS ARE NOT TO BE SCALED, STATED DIMENSIONS ONLY ARE TO BE TAKEN.
3. ANY INCONSISTENCY OR DISCRIPANCY IS TO BE BROUGHT TO THE ATTENTION OF & RESOLVED BY THE ARCHITECT/ENGINEER BEFORE THE WORK IS PUT IN HAND.

DATE	DESCRIPTION	BY

CONSULTANT :

EMSQUARE
ENGINEERING CONSULTANTS
ARCHITECTS-CIVIL ENGINEERS-INTERIORS
P.O. Box 181903, Tel: +971 4 2729009, Fax: +971 4 2729334
Email: emsquare@emirates.net.ae

OWNER :

G F S REAL ESTATE L.L.C

JOB TITLE :
PROPOSED RESIDENTIAL BUILDING
(B+G+5+ROOF)

PLOT NO. / PARCEL ID	BLOCK / COMMUNITY
5310319	SAIH SHUAIB 2

DRAWING TITLE :
UPPER ROOF PLAN

ARCHITECT :	STRUCTURAL ENGR. :	DRAWN :
SMITHA		**SHAFI**
SCALE :	DATE :	CHECKED BY :
1:150	**JUN-2025**	**BABU**
JOB NO :	DRAWING NO. :	REVISION NO. :
—	A-07-009	--

: D:\ANJU PROJECTS 2023\PROJECTS\GFS\08. 5310319 - COVENTRY RESIDENCE 3 - G F S REAL ESTATE L.L.C\FINAL SUBMISSION\FINAL AUTHORITY SUB\ARCH\CAD\A-07-009 UPPER ROOF PLAN.dwg