A-07-009 UPPER ROOF PLAN - take-off markup. 23 grid bays matched by label to dimensions stated on other sheets, spread 0.19%; effective scale 1:152.4 (title block 1:150)

TAKE-OFF ON THIS SHEET (trade colours)
H-H  D-1: 1 tag(s) here - count OPEN
H-Y  DW 11: 3 tag(s) here - count CLOSED
H-Z  DW 12: 1 tag(s) here - count CLOSED
+ added since previous revision: 5
x removed since previous revision: 0
-> moved since previous revision: 0

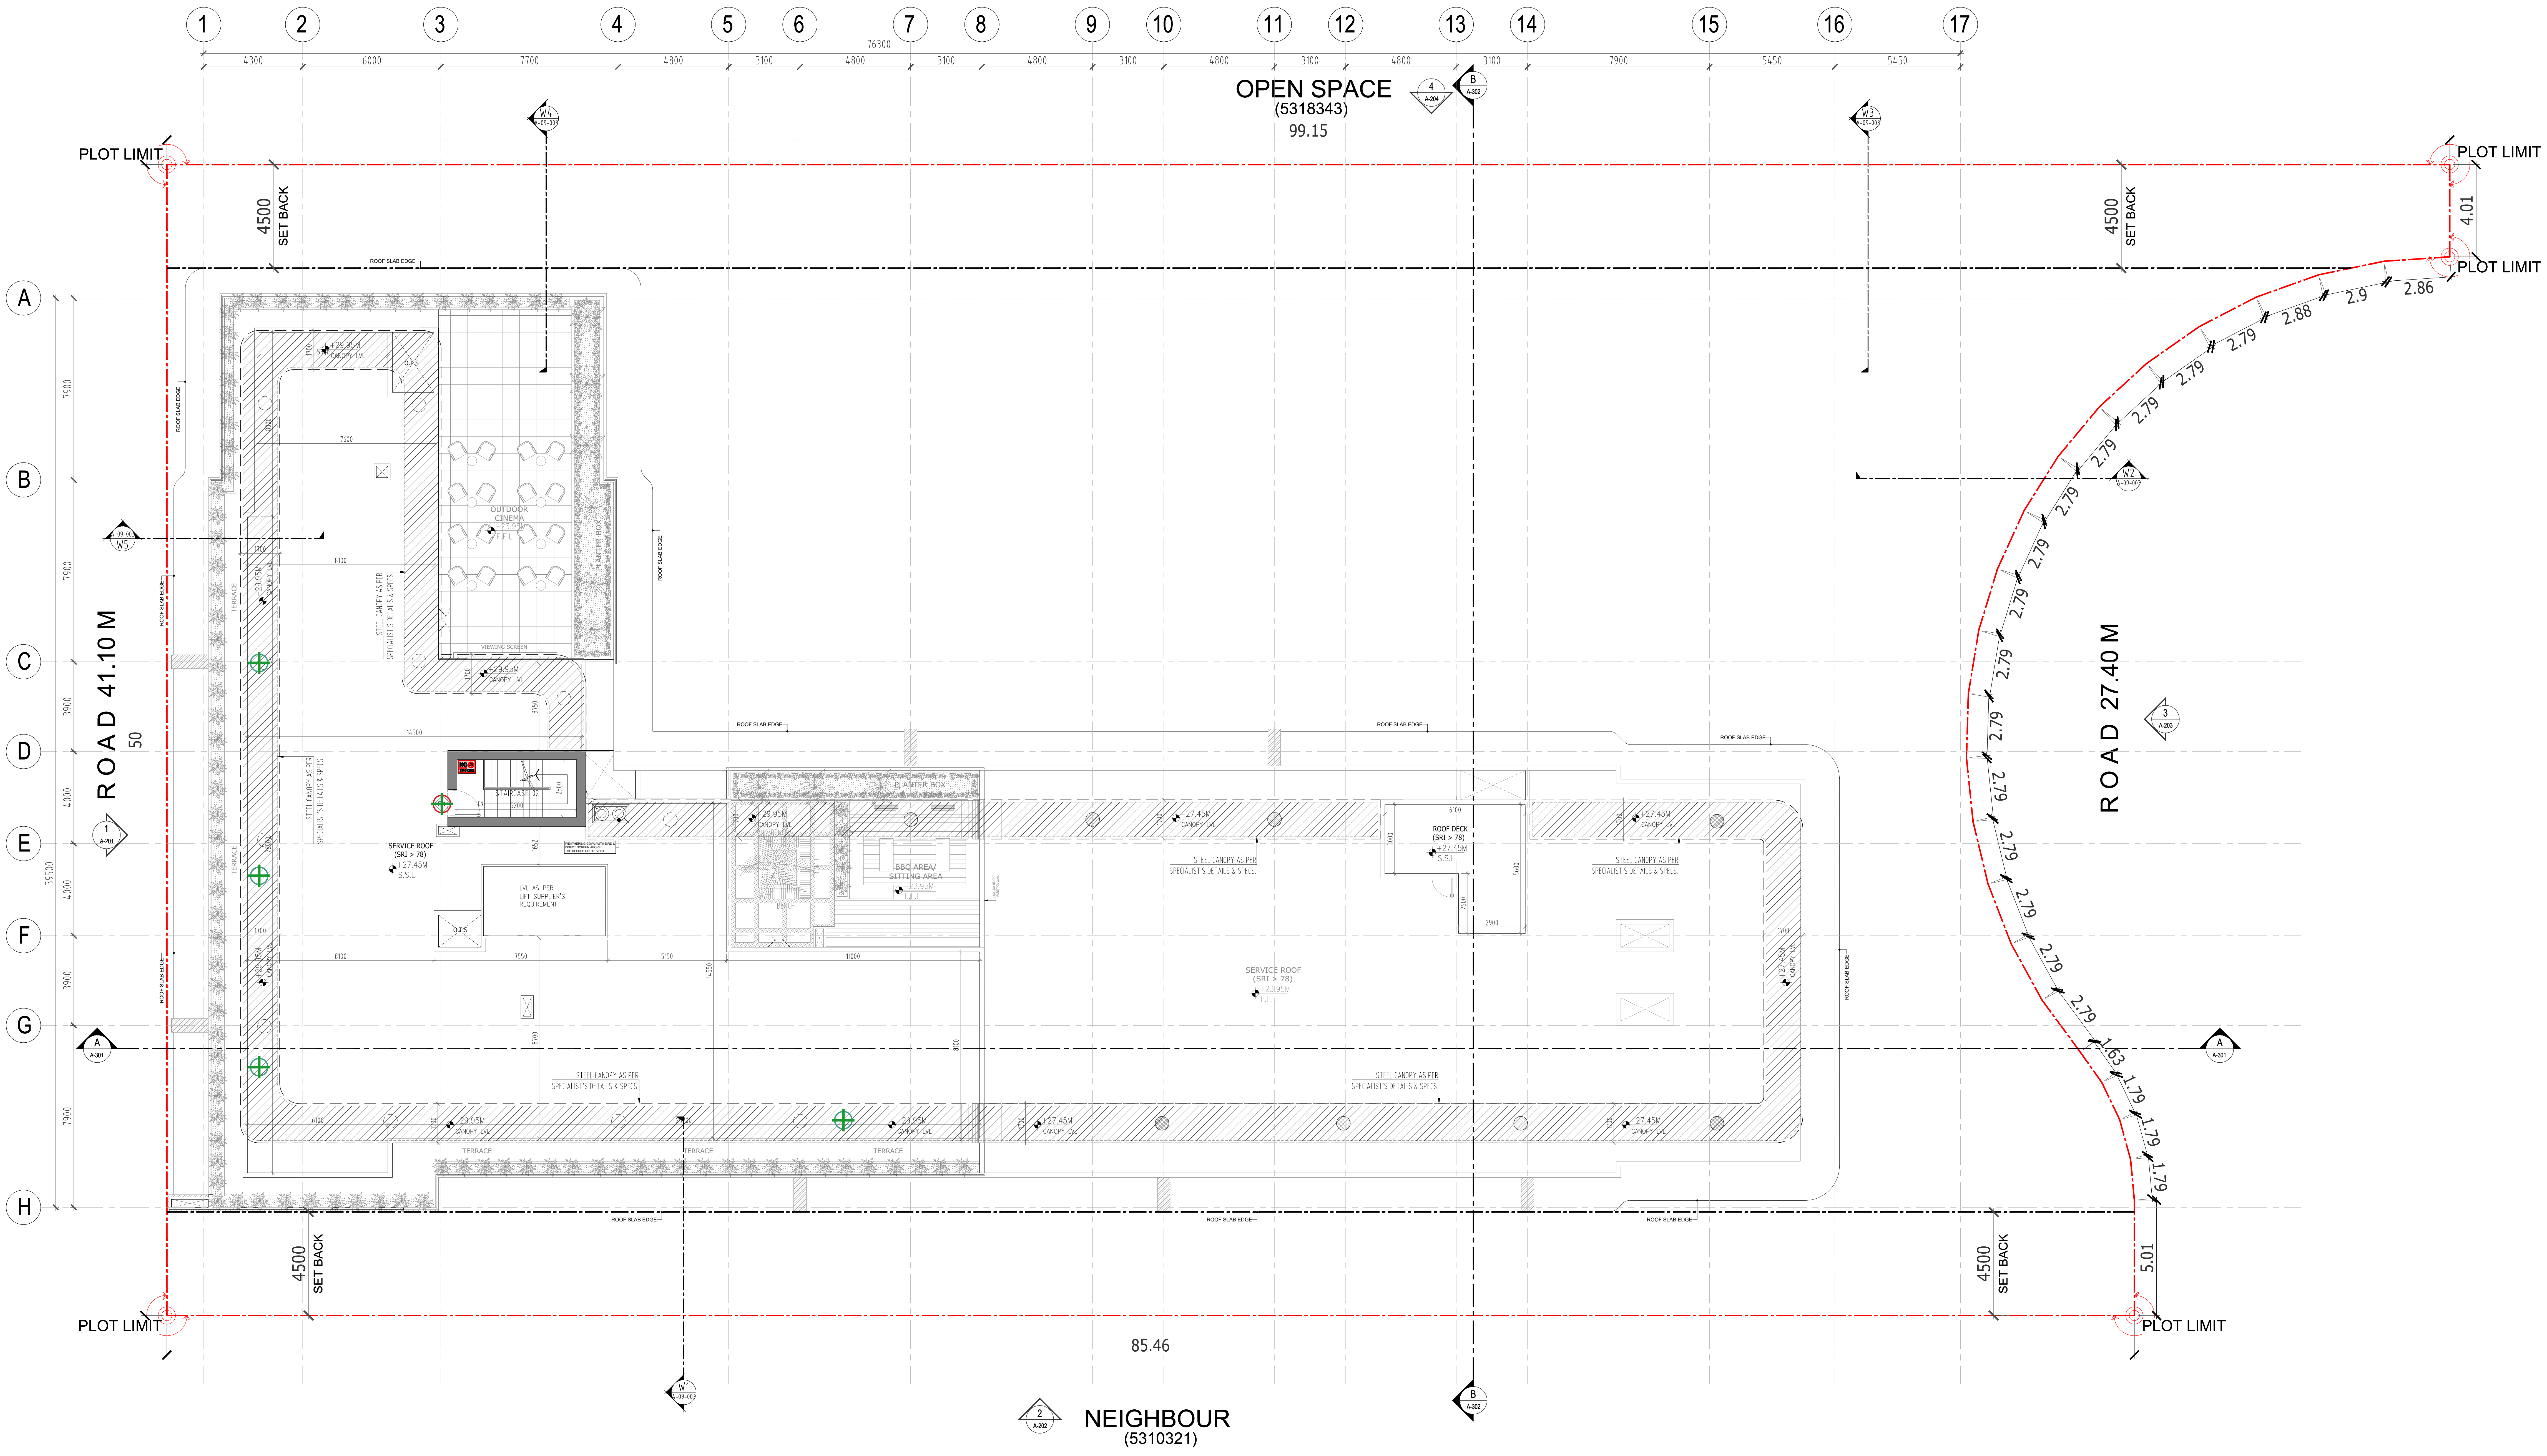

NOTES:

1. THIS DRAWING MAY NOT BE REPRODUCED BY ANY MEANS WITHOUT PRIOR APPROVAL FROM EMSQUARE.
2. DRAWINGS ARE NOT TO BE SCALED, STATED DIMENSIONS ONLY ARE TO BE TAKEN.
3. ANY INCONSISTENCY OR DISCRIPANCY IS TO BE BROUGHT TO THE ATTENTION OF & RESOLVED BY THE ARCHITECT/ENGINEER BEFORE THE WORK IS PUT IN HAND.

| DATE | DESCRIPTION | BY |
|---|---|---|

CONSULTANT :

**EMSQUARE**
ENGINEERING CONSULTANTS
ARCHITECTS-CIVIL ENGINEERS-INTERIORS
P.O. Box 181903, Tel: +971 4 2729009, Fax: +971 4 2729334
Email: emsquare@emirates.net.ae

OWNER :

**G F S REAL ESTATE L.L.C**

JOB TITLE :

PROPOSED RESIDENTIAL BUILDING
(B+G+5+ROOF)

| PLOT NO. / PARCEL ID | BLOCK / COMMUNITY |
|---|---|
| 5310319 | SAIH SHUAIB 2 |

DRAWING TITLE :

UPPER ROOF PLAN

| ARCHITECT : | STRUCTURAL ENGR. : | DRAWN : |
|---|---|---|
| **SMITHA** | | **SHAFI** |
| SCALE : | DATE : | CHECKED BY : |
| 1:150 | **JUN-2025** | **BABU** |
| JOB NO : | DRAWING NO. : | REVISION NO. : |
| — | A-07-009 | -- |

: D:\ANJU PROJECTS 2023\PROJECTS\GFS\08. 5310319 - COVENTRY RESIDENCE 3 - G F S REAL ESTATE L.L.C\FINAL SUBMISSION\FINAL AUTHORITY SUB\ARCH\CAD\A-07-009 UPPER ROOF PLAN.dwg