A-08-001 ELEVATION - finishes measured by colour. 8 storey dimensions on this sheet agree within 1%, and 7 grid bays matched to the plans agree; effective scale

FINISHES MEASURED ON THIS ELEVATION (by colour)

🟥	F1 106.67 m2 - J-U To external walls, brick cladding
🟦	F2 658.91 m2 - glazing - billed from the schedules

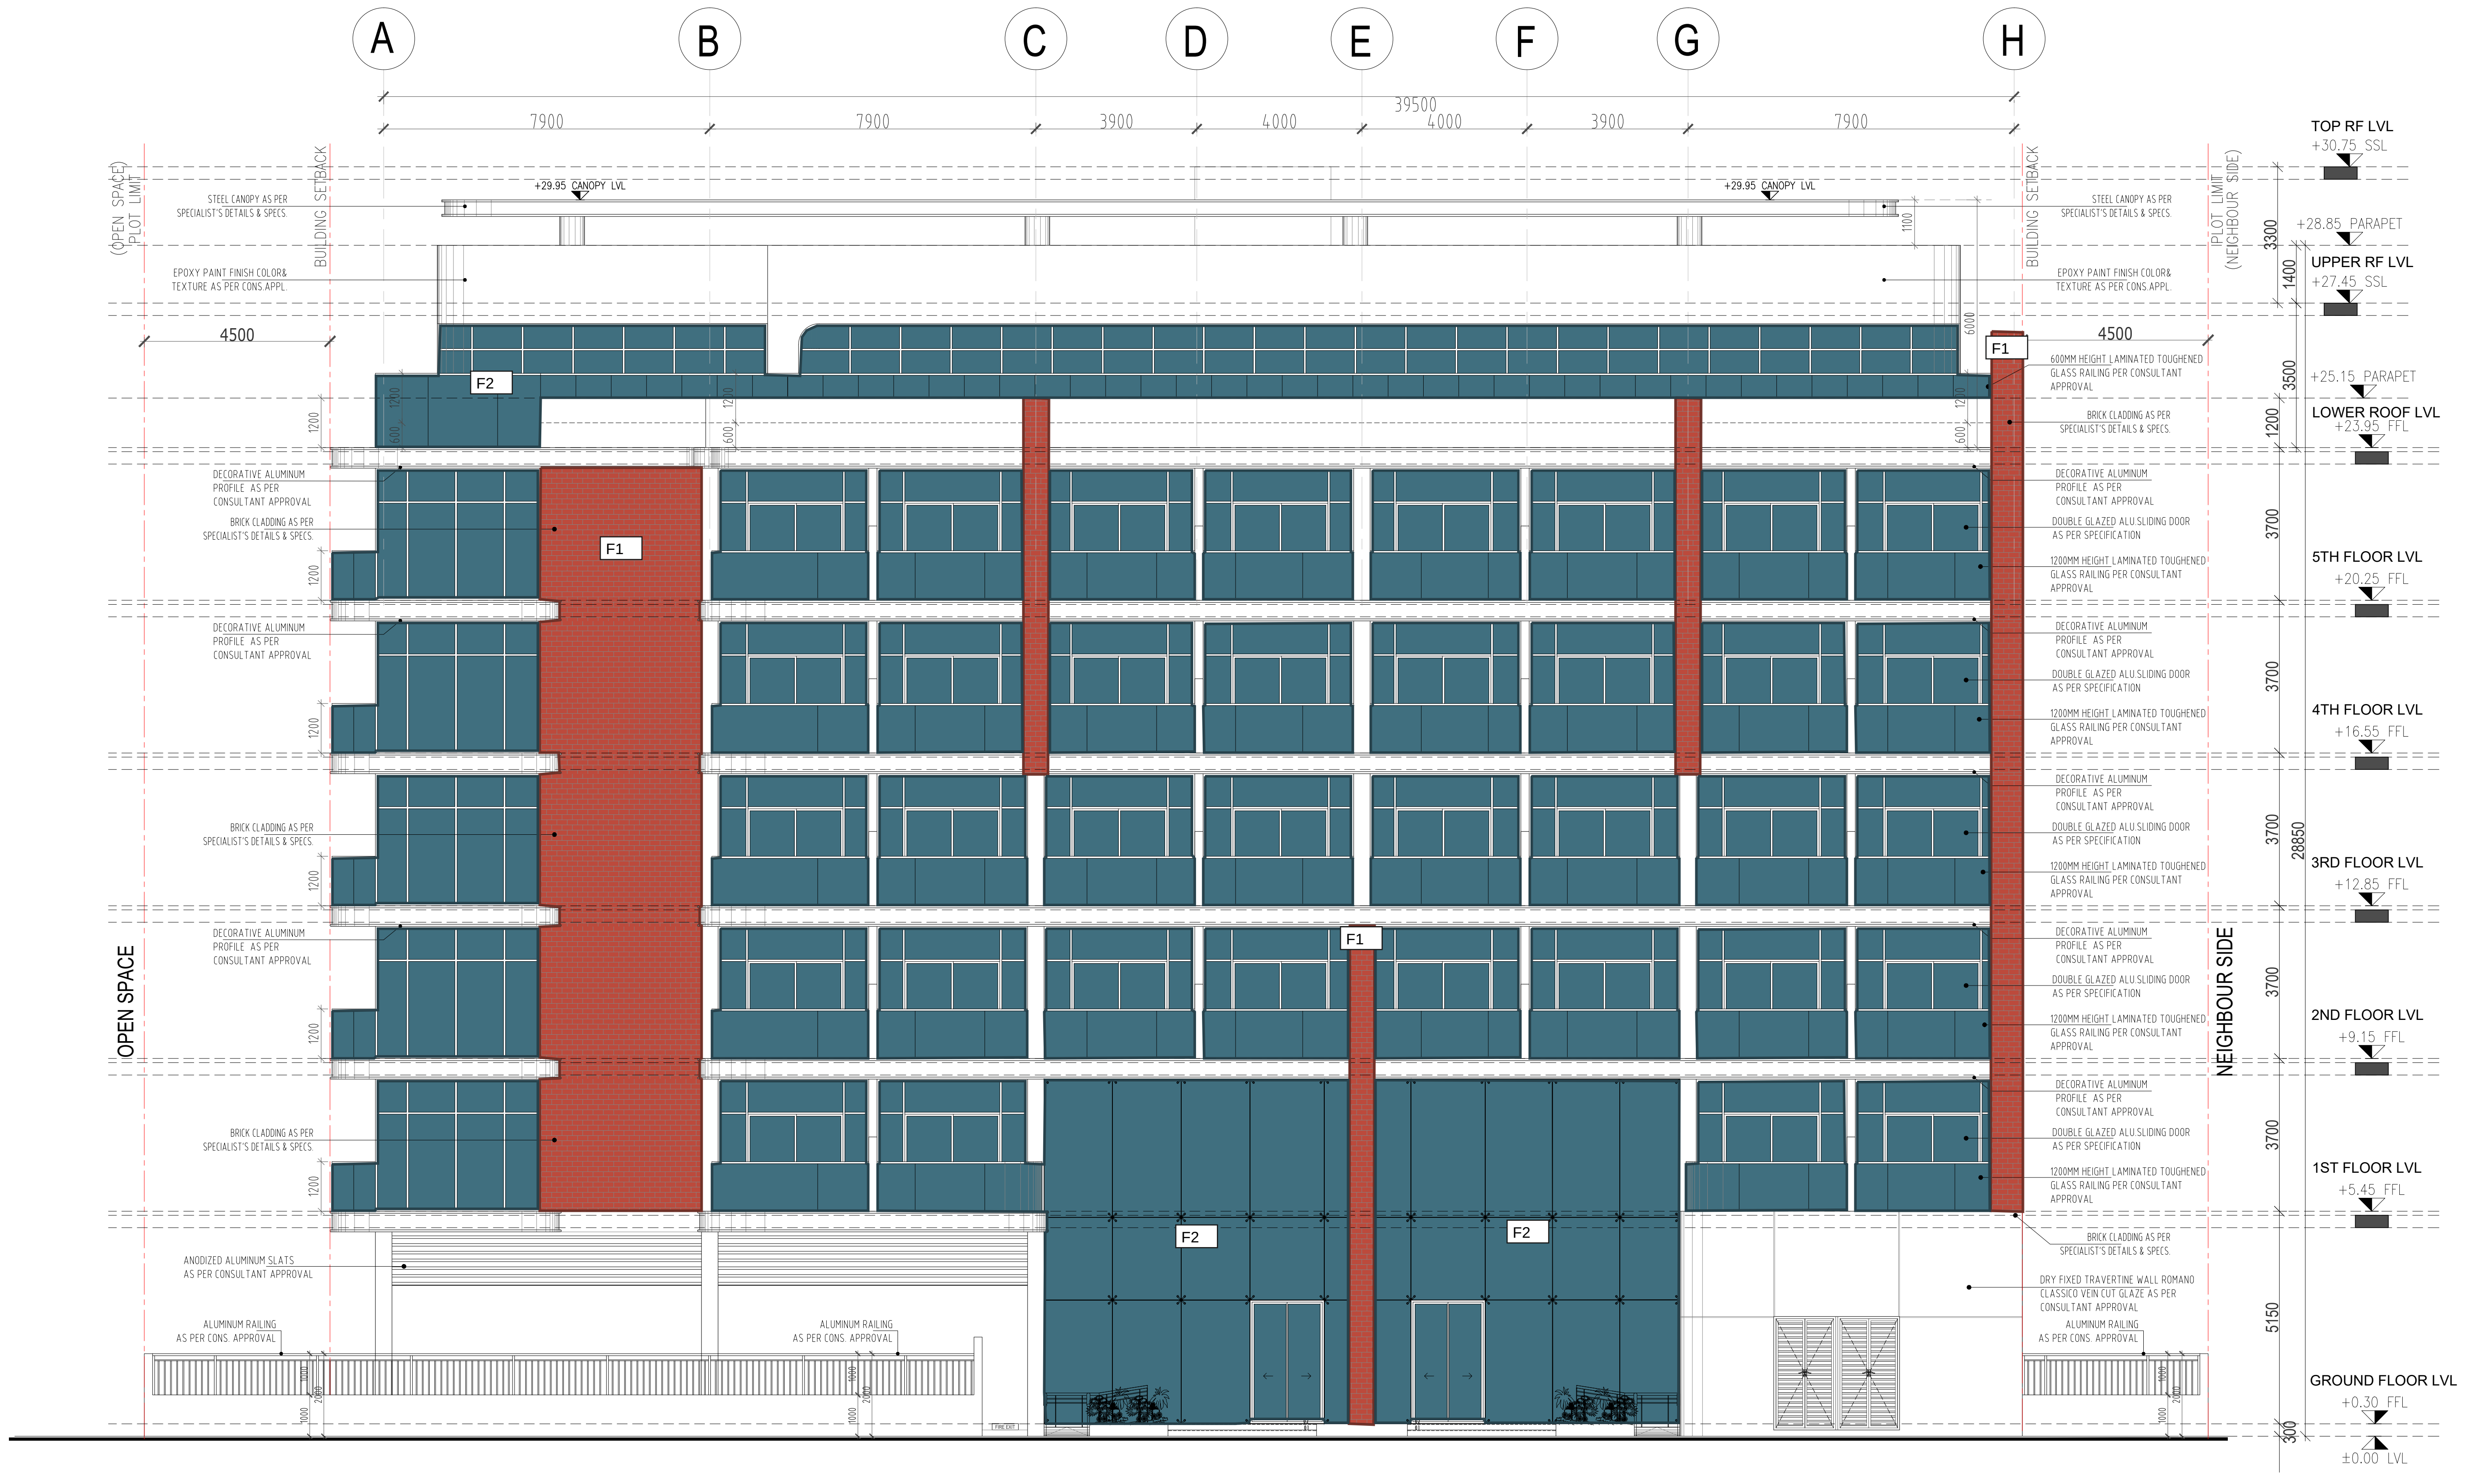
A
B
C
D
E
F
G
H
39500
7900
7900
3900
4000
4000
3900
7900
4500
4500
(OPEN SPACE) PLOT LIMIT
BUILDING SETBACK
PLOT LIMIT (NEIGHBOUR SIDE)
OPEN SPACE
NEIGHBOUR SIDE
+29.95 CANOPY LVL
STEEL CANOPY AS PER SPECIALIST'S DETAILS & SPECS.
EPOXY PAINT FINISH COLOR& TEXTURE AS PER CONS.APPL.
1200MM HEIGHT LAMINATED TOUGHENED GLASS RAILING PER CONSULTANT APPROVAL
BRICK CLADDING AS PER SPECIALIST'S DETAILS & SPECS.
DECORATIVE ALUMINUM PROFILE AS PER CONSULTANT APPROVAL
DOUBLE GLAZED ALU.SLIDING DOOR AS PER SPECIFICATION
ANODIZED ALUMINUM SLATS AS PER CONSULTANT APPROVAL
ALUMINUM RAILING AS PER CONS. APPROVAL
DRY FIXED TRAVERTINE WALL ROMANO CLASSICO VEIN CUT GLAZE AS PER CONSULTANT APPROVAL
F1
F2
TOP RF LVL
+30.75 SSL
+28.85 PARAPET
UPPER RF LVL
+27.45 SSL
+25.15 PARAPET
LOWER ROOF LVL
+23.95 FFL
5TH FLOOR LVL
+20.25 FFL
4TH FLOOR LVL
+16.55 FFL
3RD FLOOR LVL
+12.85 FFL
2ND FLOOR LVL
+9.15 FFL
1ST FLOOR LVL
+5.45 FFL
GROUND FLOOR LVL
+0.30 FFL
±0.00 LVL
3300
1400
3500
1200
3700
3700
3700
3700
3700
5150
300
28850

ELEVATION -1

1

NOTES:

1. THIS DRAWING MAY NOT BE REPRODUCED BY ANY MEANS WITHOUT PRIOR APPROVAL FROM EMSQUARE
2. DRAWINGS ARE NOT TO BE SCALED, STATED DIMENSIONS ONLY ARE TO BE TAKEN.
3. ANY INCONSISTENCY OR DISCRIPANCY IS TO BE BROUGHT TO THE ATTENTION OF & RESOLVED BY THE ARCHITECT/ENGINEER BEFORE THE WORK IS PUT IN HAND.

DATE	DESCRIPTION	BY

CONSULTANT :

EMSQUARE
ENGINEERING CONSULTANTS
ARCHITECTS-CIVIL ENGINEERS-INTERIORS
P.O. Box 181903, Tel: +971 4 2729009, Fax: +971 4 2729334
Email: emsquare@emirates.net.ae

OWNER :

G F S REAL ESTATE L.L.C

JOB TITLE :

PROPOSED RESIDENTIAL BUILDING
(B+G+5+ROOF)

PLOT NO. / PARCEL ID	BLOCK / COMMUNITY
5310319	SAIH SHUAIB 2

DRAWING TITLE :

ELEVATION -1

ARCHITECT :	STRUCTURAL ENGR. :	DRAWN :
SMITHA		**SHAFI**
SCALE :	DATE :	CHECKED BY :
1:125	**JUN-2025**	**BABU**
JOB NO :	DRAWING NO. :	REVISION NO. :
—	A-08-001	--

: D:\ANJU PROJECTS 2023\PROJECTS\GFS\08. 5310319 - COVENTRY RESIDENCE 3 - G F S REAL ESTATE L.L.C\FINAL SUBMISSION\FINAL AUTHORITY SUB\ARCH\CAD\A-08-001 ELEVATIONS.DWG