A-08-003 ELEVATION - finishes measured by colour. 8 storey dimensions on this sheet agree within 1%, and 7 grid bays matched to the plans agree; effective scale 1:127.8

FINISHES MEASURED ON THIS ELEVATION (by colour)

- 🟥 F1 137.07 m2 - J-U To external walls, brick cladding
- 🟦 F2 139.97 m2 - glazing - billed from the schedules

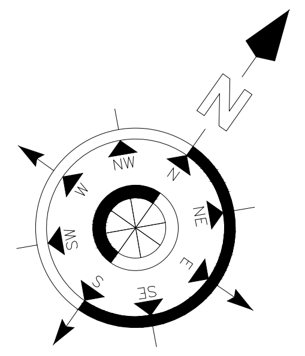

NOTES:

1. THIS DRAWING MAY NOT BE REPRODUCED BY ANY MEANS WITHOUT PRIOR APPROVAL FROM EMSQUARE
2. DRAWINGS ARE NOT TO BE SCALED, STATED DIMENSIONS ONLY ARE TO BE TAKEN.
3. ANY INCONSISTENCY OR DISCRIPANCY IS TO BE BROUGHT TO THE ATTENTION OF & RESOLVED BY THE ARCHITECT/ENGINEER BEFORE THE WORK IS PUT IN HAND.

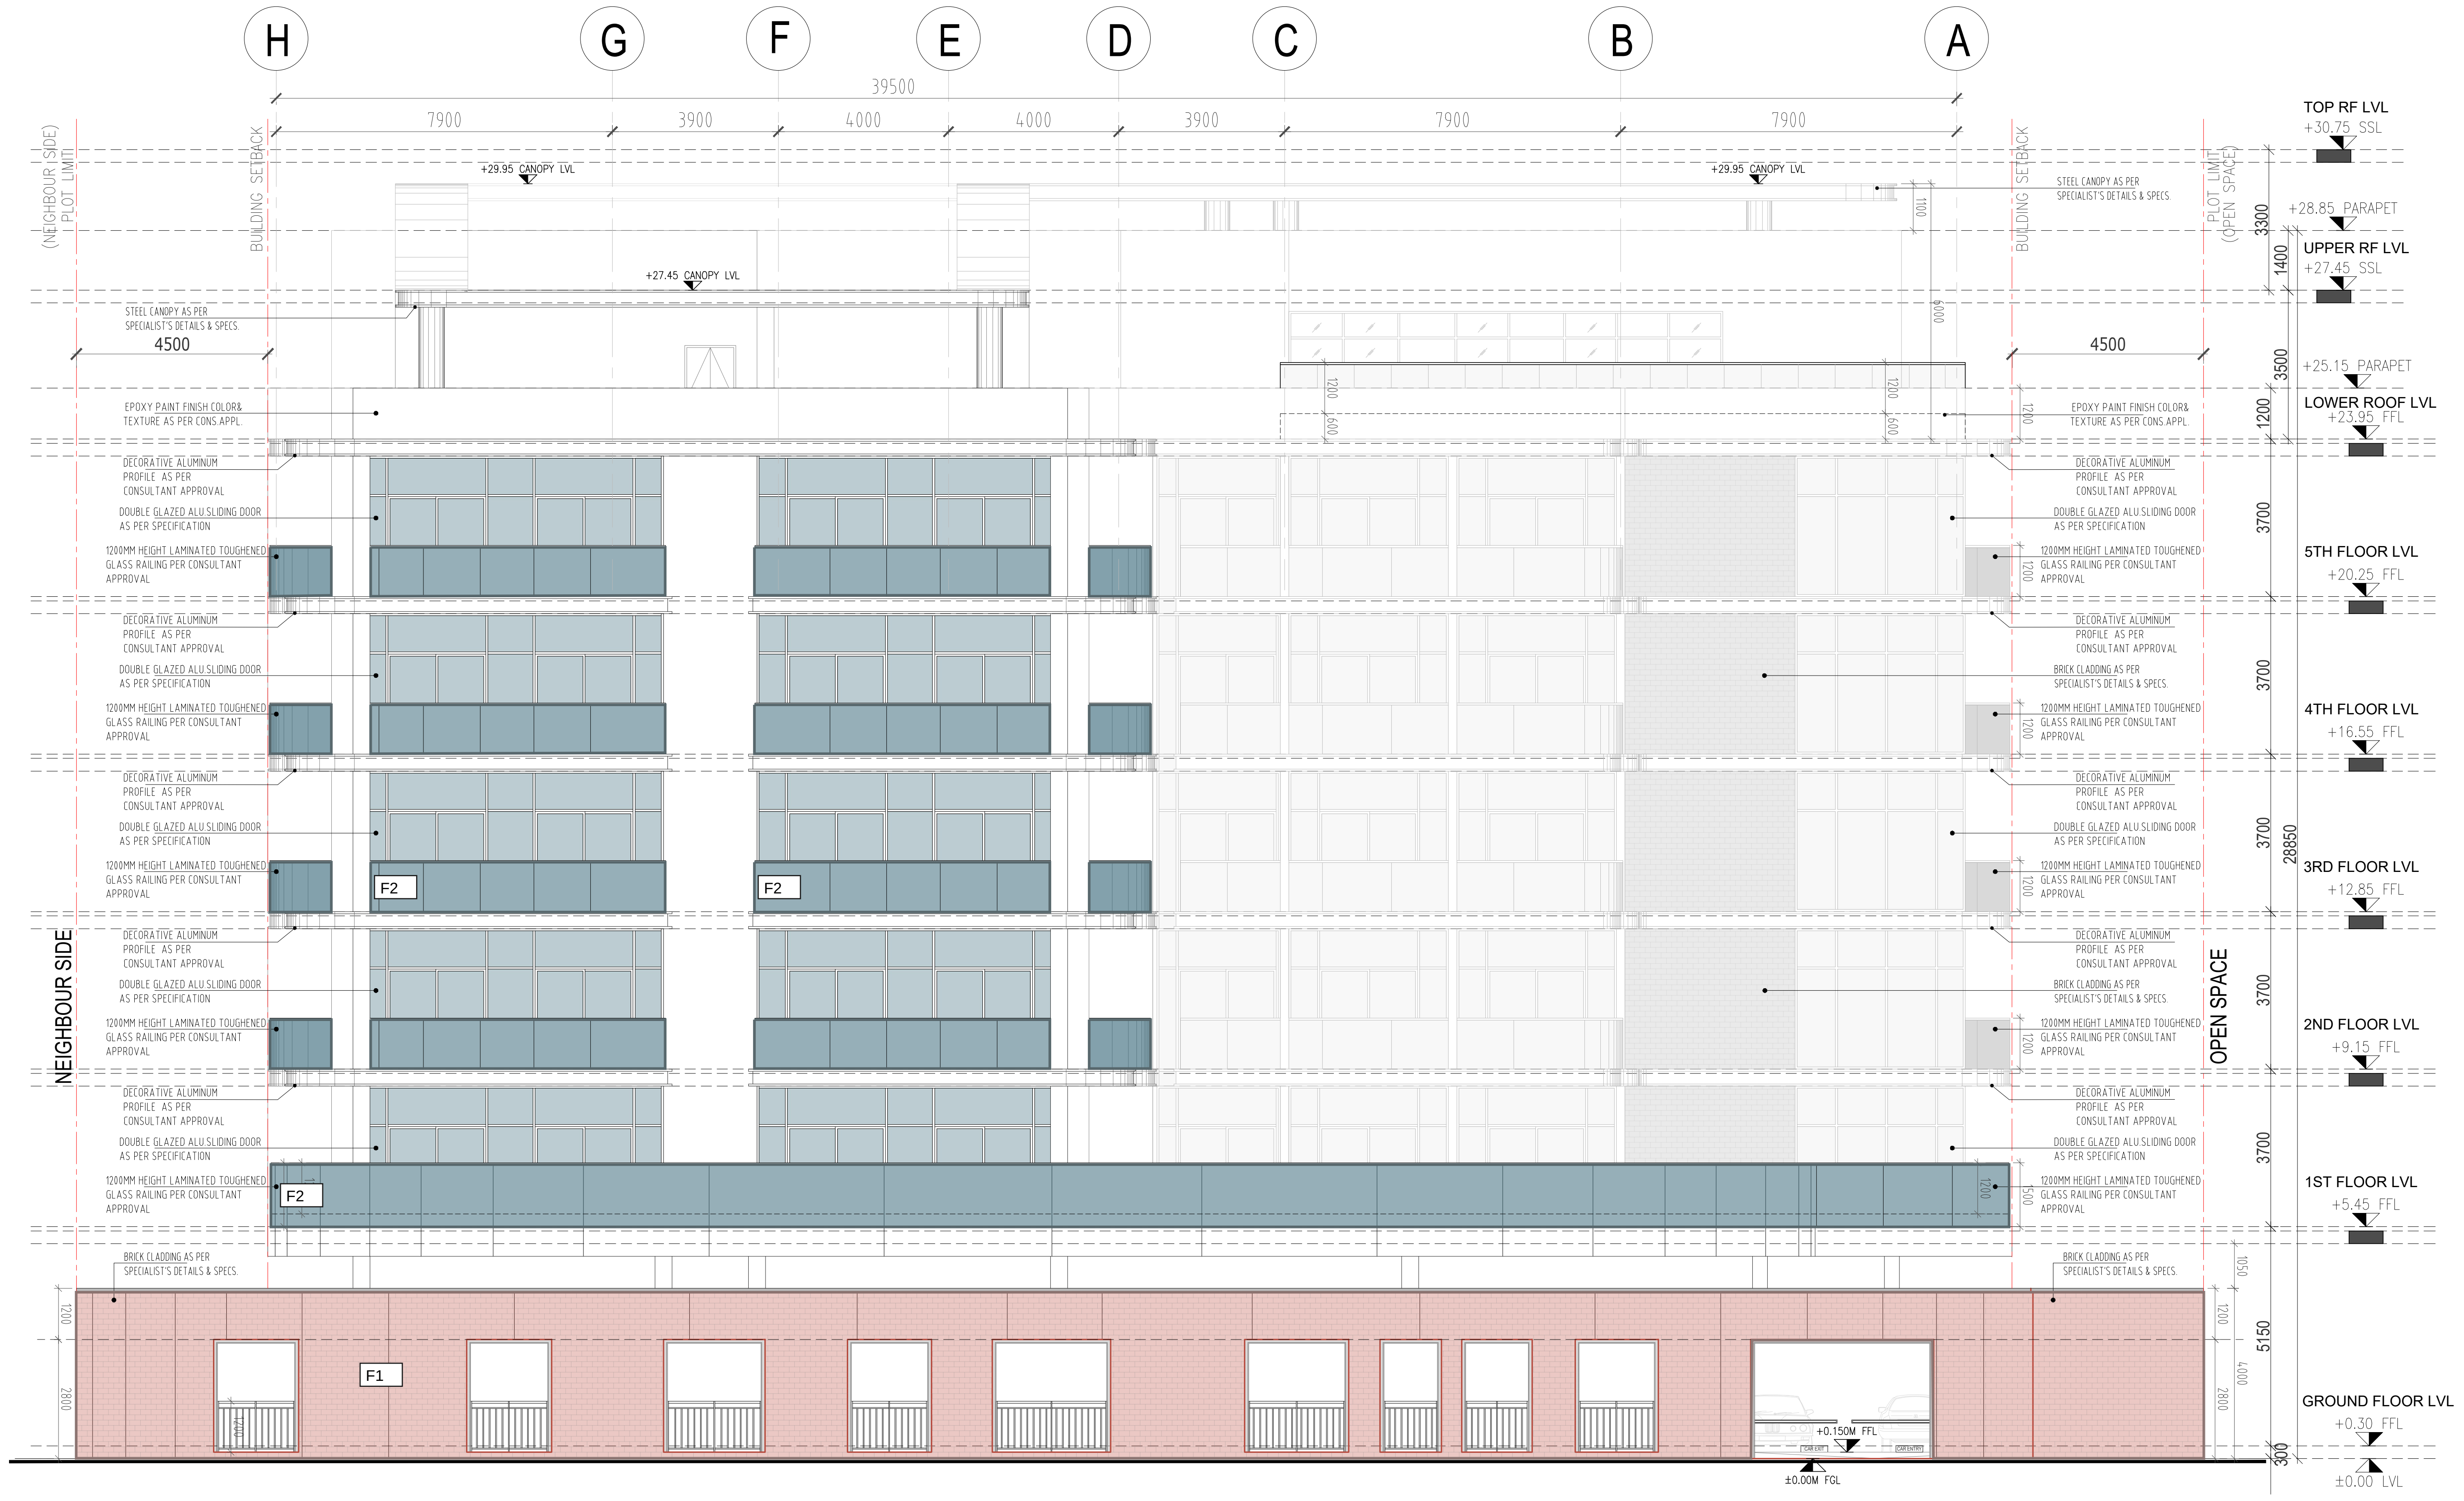
H
G
F
E
D
C
B
A
39500
7900
3900
4000
4000
3900
7900
7900
(NEIGHBOUR SIDE) PLOT LIMIT
BUILDING SETBACK
PLOT LIMIT (OPEN SPACE)
+29.95 CANOPY LVL
+27.45 CANOPY LVL
STEEL CANOPY AS PER SPECIALIST'S DETAILS & SPECS.
4500
EPOXY PAINT FINISH COLOR& TEXTURE AS PER CONS.APPL.
DECORATIVE ALUMINUM PROFILE AS PER CONSULTANT APPROVAL
DOUBLE GLAZED ALU.SLIDING DOOR AS PER SPECIFICATION
1200MM HEIGHT LAMINATED TOUGHENED GLASS RAILING PER CONSULTANT APPROVAL
BRICK CLADDING AS PER SPECIALIST'S DETAILS & SPECS.
F2
F1
NEIGHBOUR SIDE
OPEN SPACE
1100
6000
1200
600
1500
1050
4000
2800
TOP RF LVL
+30.75 SSL
+28.85 PARAPET
UPPER RF LVL
+27.45 SSL
+25.15 PARAPET
LOWER ROOF LVL
+23.95 FFL
5TH FLOOR LVL
+20.25 FFL
4TH FLOOR LVL
+16.55 FFL
3RD FLOOR LVL
+12.85 FFL
2ND FLOOR LVL
+9.15 FFL
1ST FLOOR LVL
+5.45 FFL
GROUND FLOOR LVL
+0.30 FFL
±0.00 LVL
+0.150M FFL
±0.00M FGL
CAR ENTRY
3300
1400
3500
1200
3700
3700
3700
3700
3700
28850
5150
300

ELEVATION -3

1

DATE	DESCRIPTION	BY

CONSULTANT :

EMSQUARE
ENGINEERING CONSULTANTS
ARCHITECTS-CIVIL ENGINEERS-INTERIORS
P.O. Box 181903, Tel: +971 4 2729009, Fax: +971 4 2729334
Email: emsquare@emirates.net.ae

OWNER :

G F S REAL ESTATE L.L.C

JOB TITLE :

PROPOSED RESIDENTIAL BUILDING
(B+G+5+ROOF)

PLOT NO. / PARCEL ID	BLOCK / COMMUNITY
5310319	SAIH SHUAIB 2

DRAWING TITLE :

ELEVATION -3

ARCHITECT :	STRUCTURAL ENGR. :	DRAWN :
SMITHA		**SHAFI**
SCALE :	DATE :	CHECKED BY :
1:125	**JUN-2025**	**BABU**
JOB NO :	DRAWING NO. :	REVISION NO. :
—	A-08-003	--

: D:\ANJU PROJECTS 2023\PROJECTS\GFS\08. 5310319 - COVENTRY RESIDENCE 3 - G F S REAL ESTATE L.L.C\FINAL SUBMISSION\FINAL AUTHORITY SUB\ARCH\CAD\A-08-001 ELEVATIONS.DWG