SECTION D - Masonry

Project: PROPOSED RESIDENTIAL BUILDING (B+G+5+ROOF)
Building: None

Drawing: A-07-003
Filename: Architecture/A1/A-07-003 GROUND FLOOR PLAN.pdf

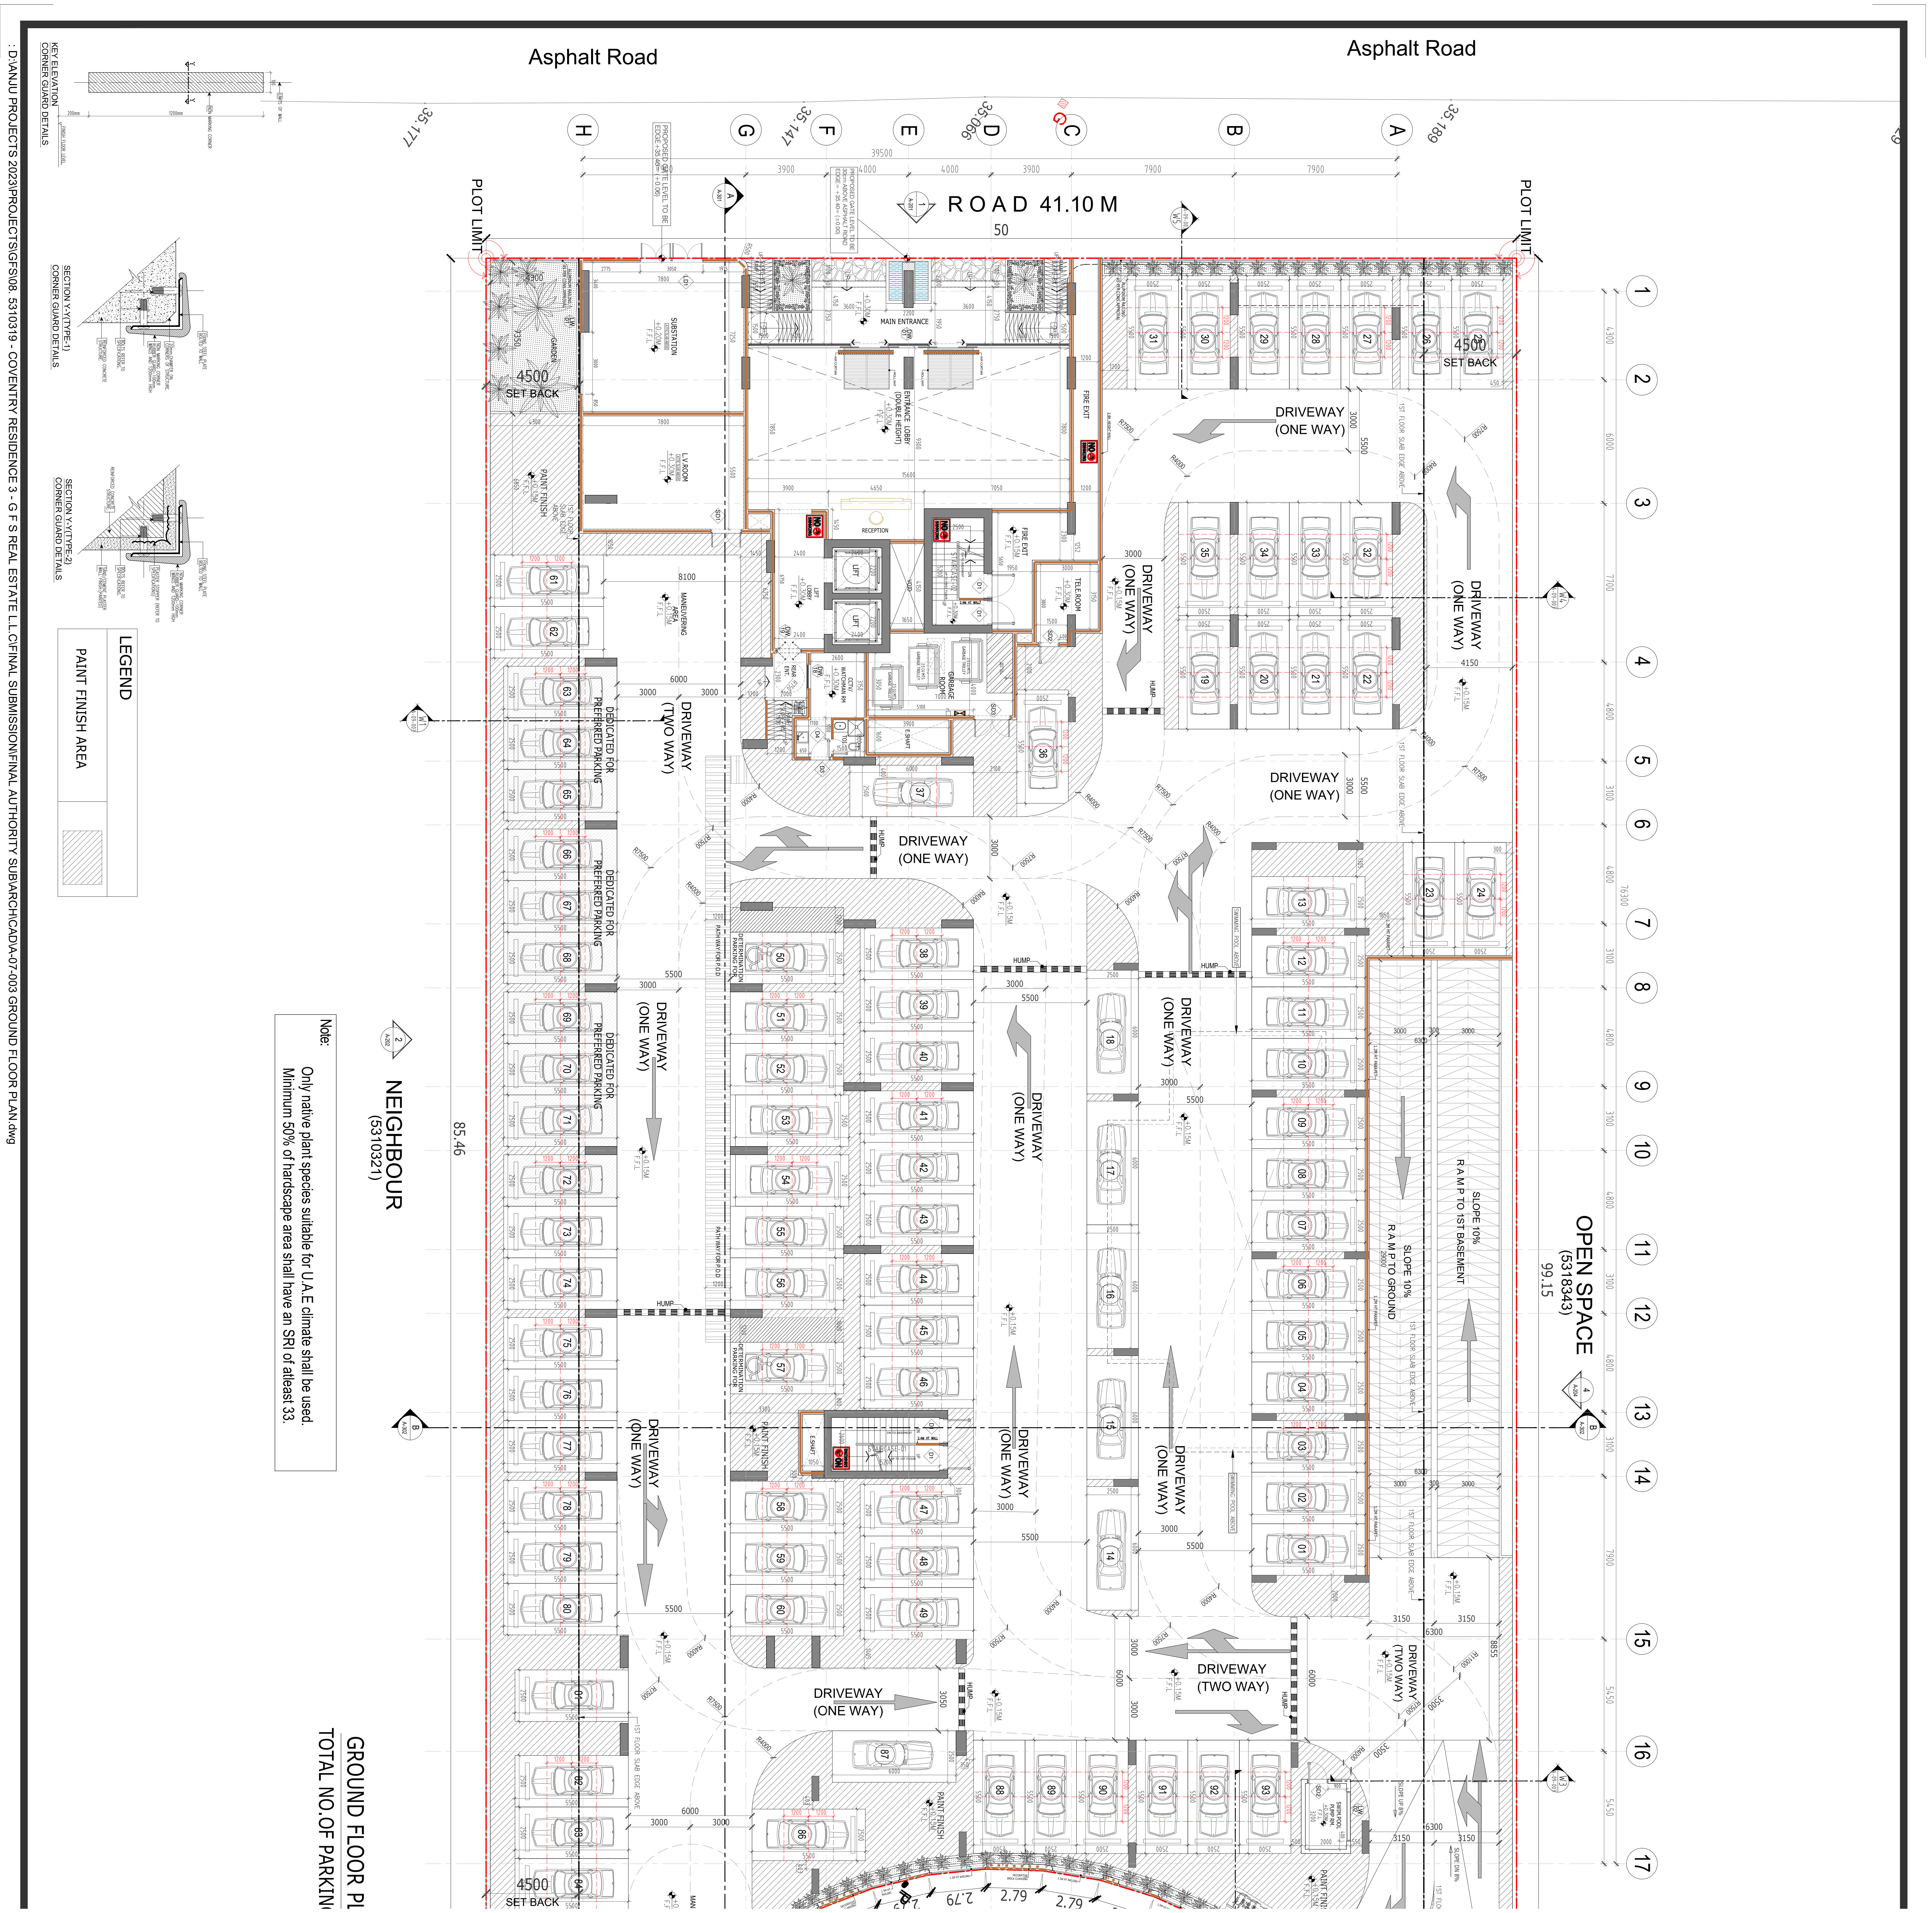

Asphalt Road
Asphalt Road
ROAD 41.10 M
50
PLOT LIMIT
PLOT LIMIT
H
G
F
E
D
C
B
A
1
2
3
4
5
6
7
8
9
10
11
12
13
14
15
16
17
MAIN ENTRANCE
RECEPTION
SUBSTATION
L.V. ROOM
FIRE EXIT
4500
SET BACK
4500
SET BACK
4500
SET BACK
DRIVEWAY
(ONE WAY)
DRIVEWAY
(TWO WAY)
HUMP
DEDICATED FOR PREFERRED PARKING
RAMP TO GROUND
SLOPE 10%
RAMP TO 1ST BASEMENT
SLOPE 10%
NEIGHBOUR
(5310321)
OPEN SPACE
(5318343)
85.46
99.15
LEGEND
PAINT FINISH AREA
Note:
Only native plant species suitable for U.A.E climate shall be used.
Minimum 50% of hardscape area shall have an SRI of atleast 33.
GROUND FLOOR PL
TOTAL NO.OF PARKIN
KEY ELEVATION CORNER GUARD DETAILS
SECTION Y-Y(TYPE-1) CORNER GUARD DETAILS
SECTION X-X(TYPE-2) CORNER GUARD DETAILS
: D:\ANJU PROJECTS 2023\PROJECTS\GFS\08. 5310319 - COVENTRY RESIDENCE 3 - G F S REAL ESTATE L.L.C\FINAL SUBMISSION\FINAL AUTHORITY SUB\ARCH\CAD\A-07-003 GROUND FLOOR PLAN.dwg

Legend

Masonry

■	D-A	113.42 m2
■	D-B	8.65 m2
■	D-C	1,031.00 m2

SECTION G - Thermal and Moisture Protection

Project: PROPOSED RESIDENTIAL BUILDING (B+G+5+ROOF)
Building: None

Drawing: A-07-003
Filename: Architecture/A1/A-07-003 GROUND FLOOR PLAN.pdf

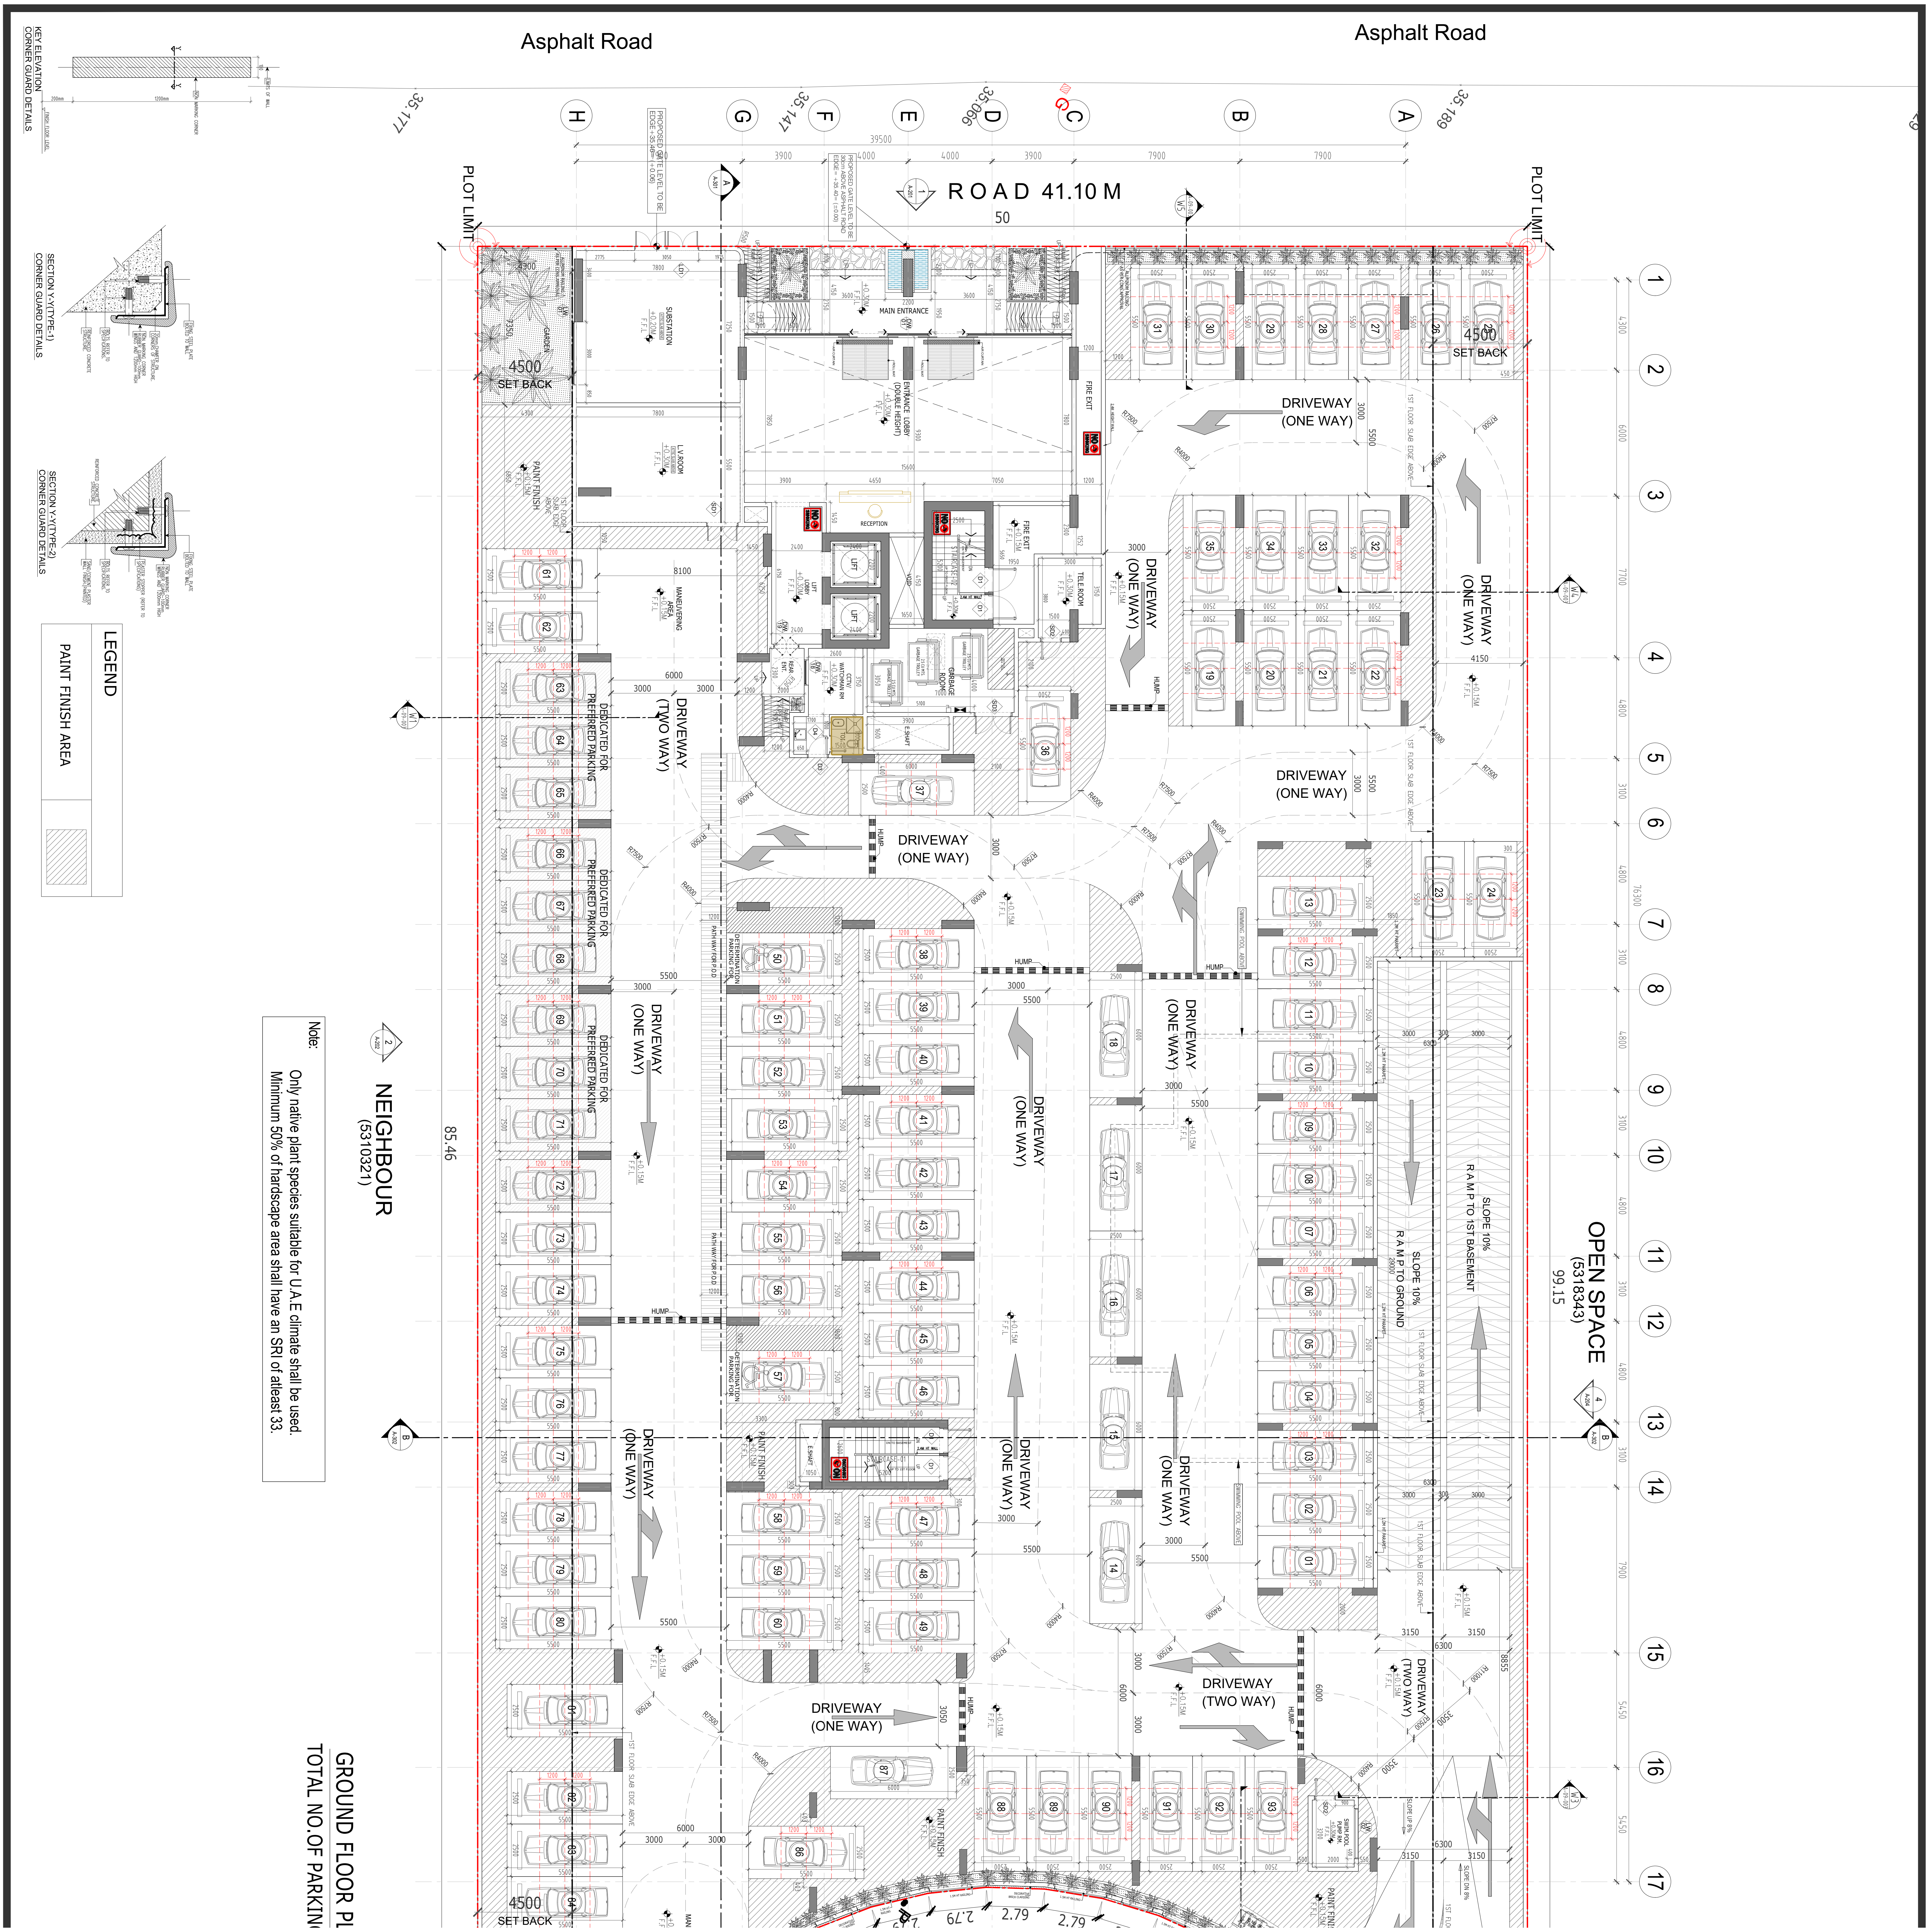
Asphalt Road
Asphalt Road
ROAD 41.10 M
50
PLOT LIMIT
PLOT LIMIT
H
G
F
E
D
C
B
A
4500
SET BACK
4500
SET BACK
MAIN ENTRANCE
ENTRANCE LOBBY (DOUBLE HEIGHT)
RECEPTION
LIFT
FIRE EXIT
DRIVEWAY (ONE WAY)
DRIVEWAY (TWO WAY)
DEDICATED FOR PREFERRED PARKING
HUMP
SLOPE 10% RAMP TO 1ST BASEMENT
SLOPE 10% RAMP TO GROUND
NEIGHBOUR (5310321)
85.46
OPEN SPACE (5318343)
99.15
LEGEND
PAINT FINISH AREA
KEY ELEVATION CORNER GUARD DETAILS
SECTION Y-Y(TYPE-1) CORNER GUARD DETAILS
SECTION X-X(TYPE-2) CORNER GUARD DETAILS
GROUND FLOOR PL
TOTAL NO.OF PARKIN
2.79
1
2
3
4
5
6
7
8
9
10
11
12
13
14
15
16
17
: D:\ANJU PROJECTS 2023\PROJECTS\GFS\08. 5310319 - COVENTRY RESIDENCE 3 - G F S REAL ESTATE L.L.C\FINAL SUBMISSION\FINAL AUTHORITY SUBMISSION\ARCH\CAD\A-07-003 GROUND FLOOR PLAN.dwg

Note:
Only native plant species suitable for U.A.E climate shall be used.
Minimum 50% of hardscape area shall have an SRI of atleast 33.

Legend

Thermal and Moisture Protection

▨ G-A 2.68 m2

SECTION J - Finishes

Project: PROPOSED RESIDENTIAL BUILDING (B+G+5+ROOF)
Building: None

Drawing: A-07-003
Filename: Architecture/A1/A-07-003 GROUND FLOOR PLAN.pdf

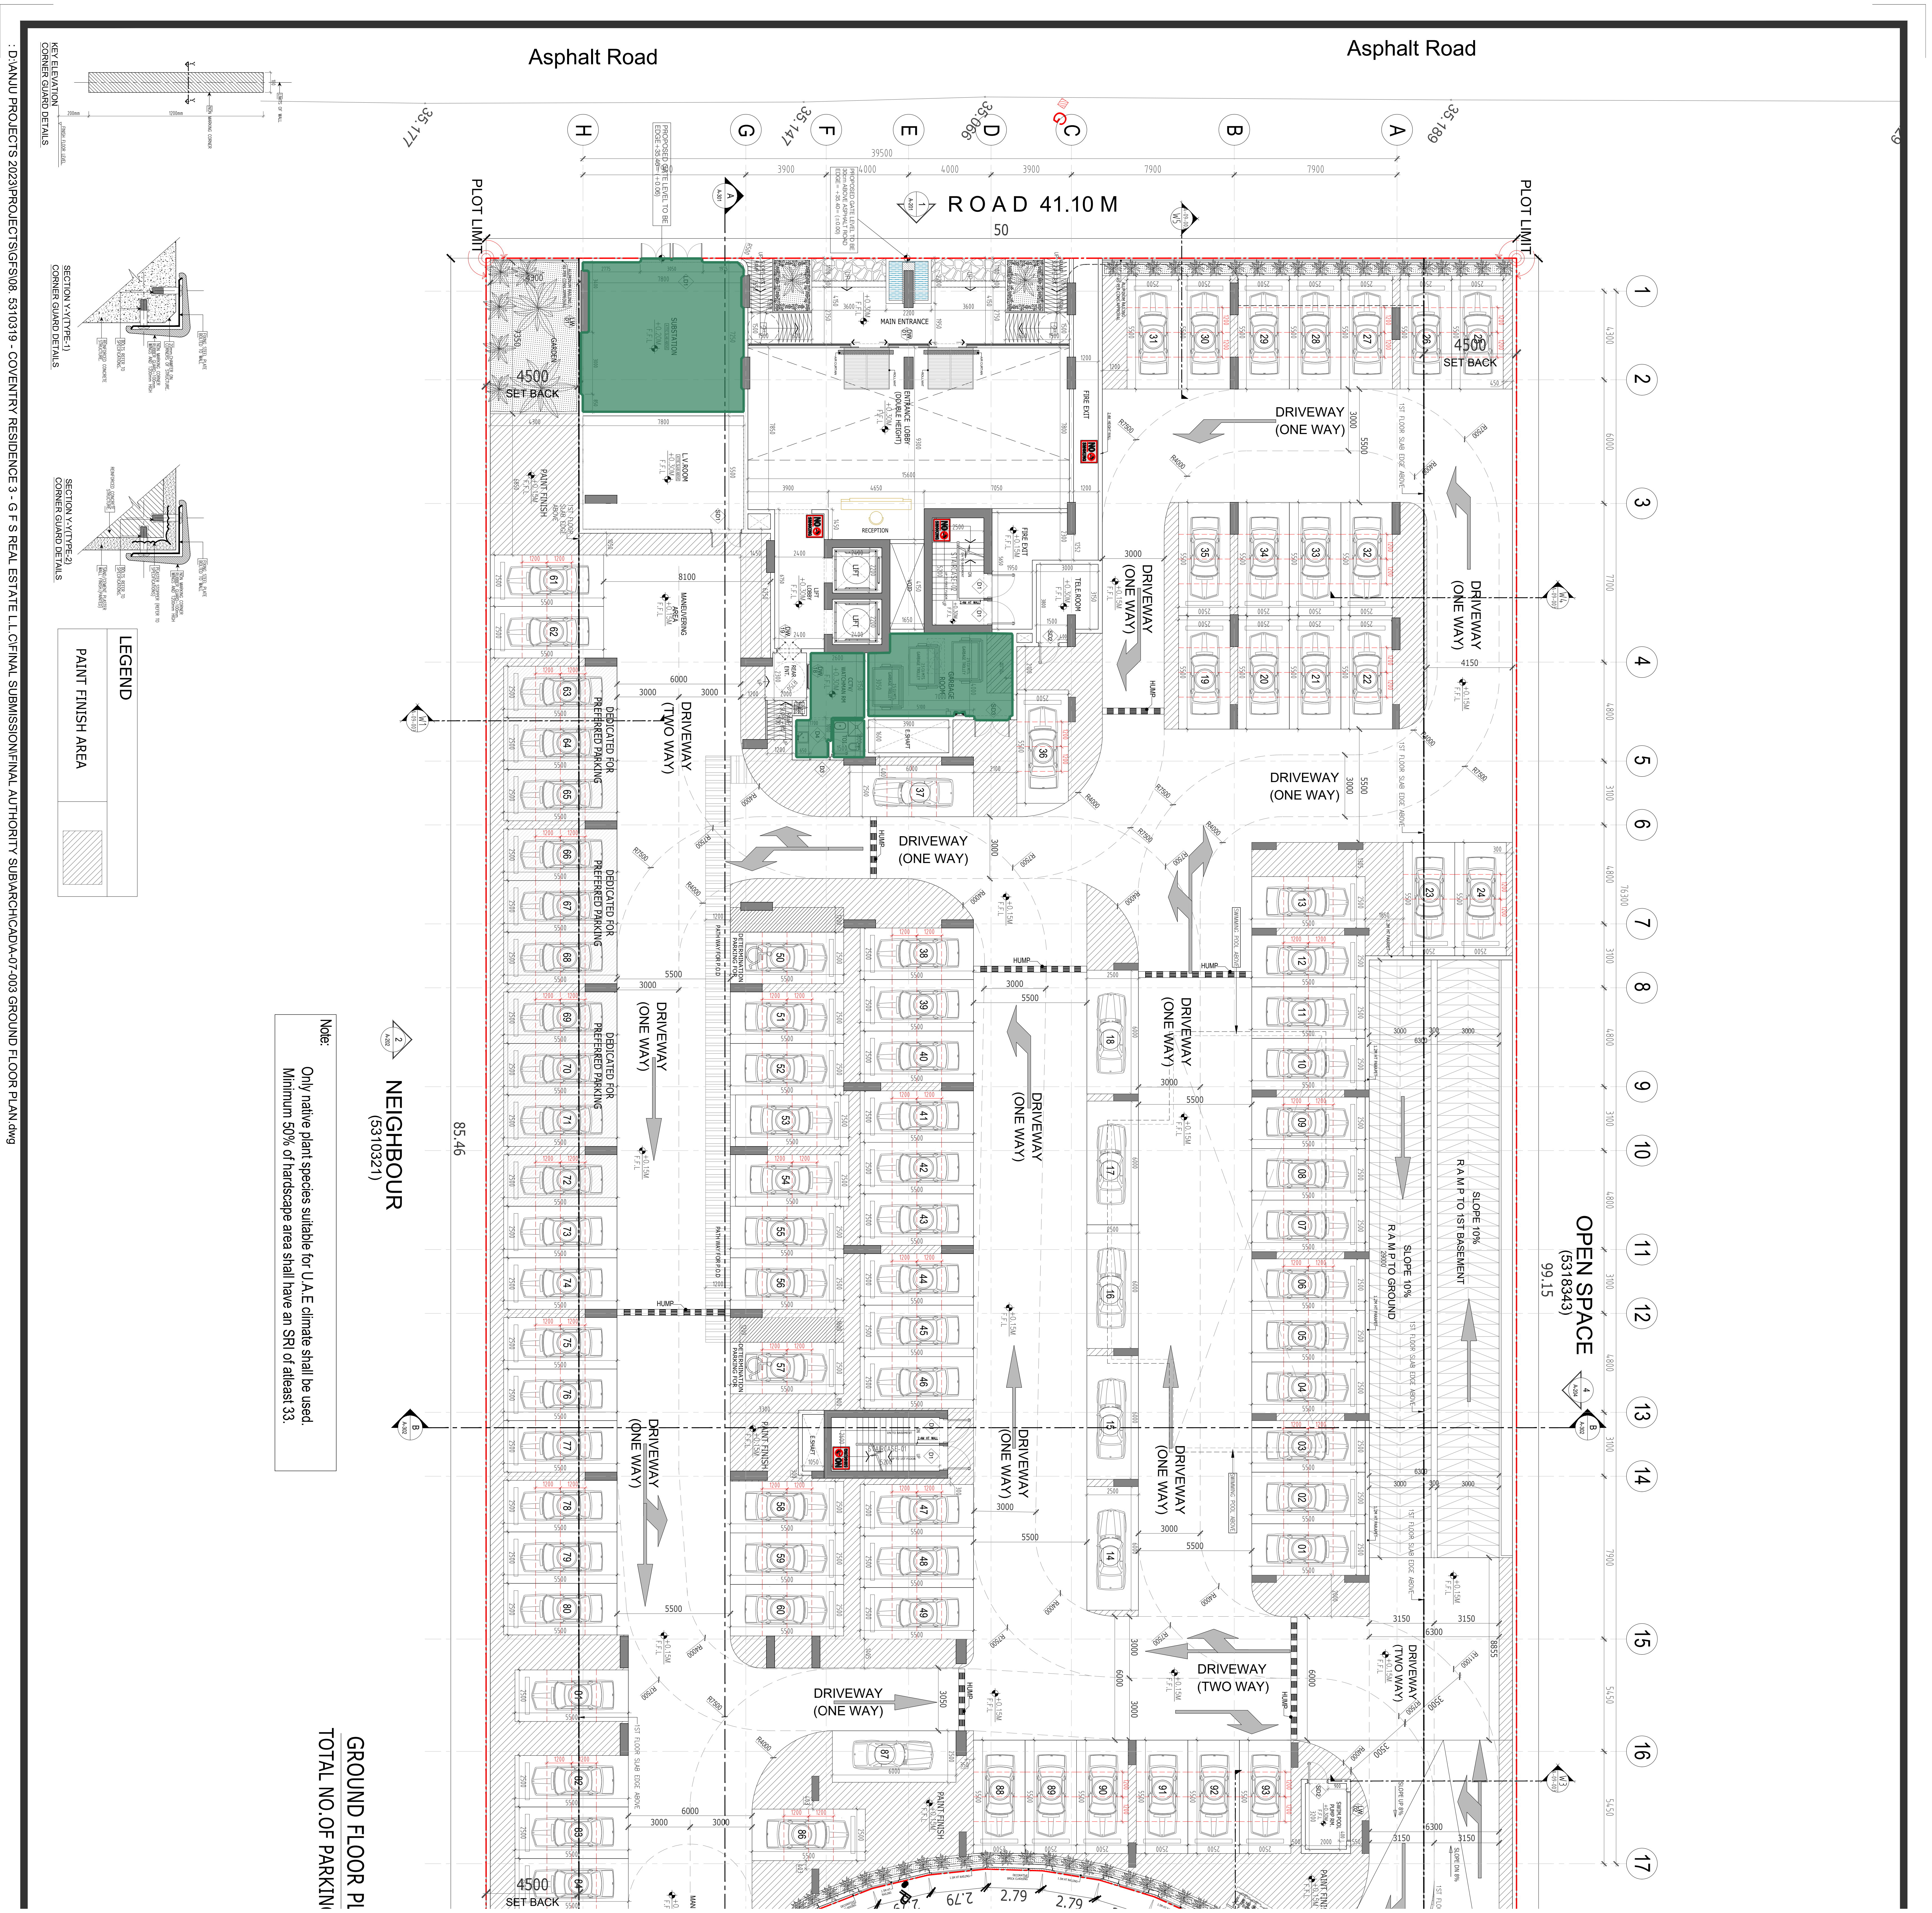

Asphalt Road
Asphalt Road
ROAD 41.10 M
50
PLOT LIMIT
PLOT LIMIT
4500 SET BACK
4500 SET BACK
4500 SET BACK
MAIN ENTRANCE
DRIVEWAY (ONE WAY)
DRIVEWAY (TWO WAY)
DRIVEWAY (ONE WAY)
DRIVEWAY (ONE WAY)
DRIVEWAY (ONE WAY)
DRIVEWAY (TWO WAY)
DRIVEWAY (ONE WAY)
DEDICATED FOR PREFERRED PARKING
SLOPE 10% R.A.M.P TO 1ST BASEMENT
SLOPE 10% R.A.M.P TO GROUND
NEIGHBOUR (5310321)
85.46
OPEN SPACE (5318343)
99.15
Note:
Only native plant species suitable for U.A.E climate shall be used.
Minimum 50% of hardscape area shall have an SRI of atleast 33.
LEGEND
PAINT FINISH AREA
GROUND FLOOR PL
TOTAL NO.OF PARKIN
KEY ELEVATION CORNER GUARD DETAILS
SECTION Y-Y(TYPE-1) CORNER GUARD DETAILS
SECTION X-X(TYPE-2) CORNER GUARD DETAILS
: D:\ANJU PROJECTS 2023\PROJECTS\GFS\08. 5310319 - COVENTRY RESIDENCE 3 - G F S REAL ESTATE L.L.C\FINAL SUBMISSION\FINAL AUTHORITY SUB\ARCH\CAD\A-07-003 GROUND FLOOR PLAN.dwg

Legend

Finishes

- 🟩 J-A 94.60 m2
- 🟩 J-B 2.68 m2
- 🟩 J-C 94.60 m2
- 🟩 J-D 2.68 m2
- 🟩 J-E 332.95 m2
- 🟩 J-F 30.53 m2
- 🟩 J-G 64.03 m
- 🟩 J-H 5.59 m