SECTION D - Masonry

Project: PROPOSED RESIDENTIAL BUILDING (B+G+5+ROOF)
Building: None

Drawing: A-07-008
Filename: Architecture/A1/A-07-008 LOWER ROOF PLAN.pdf

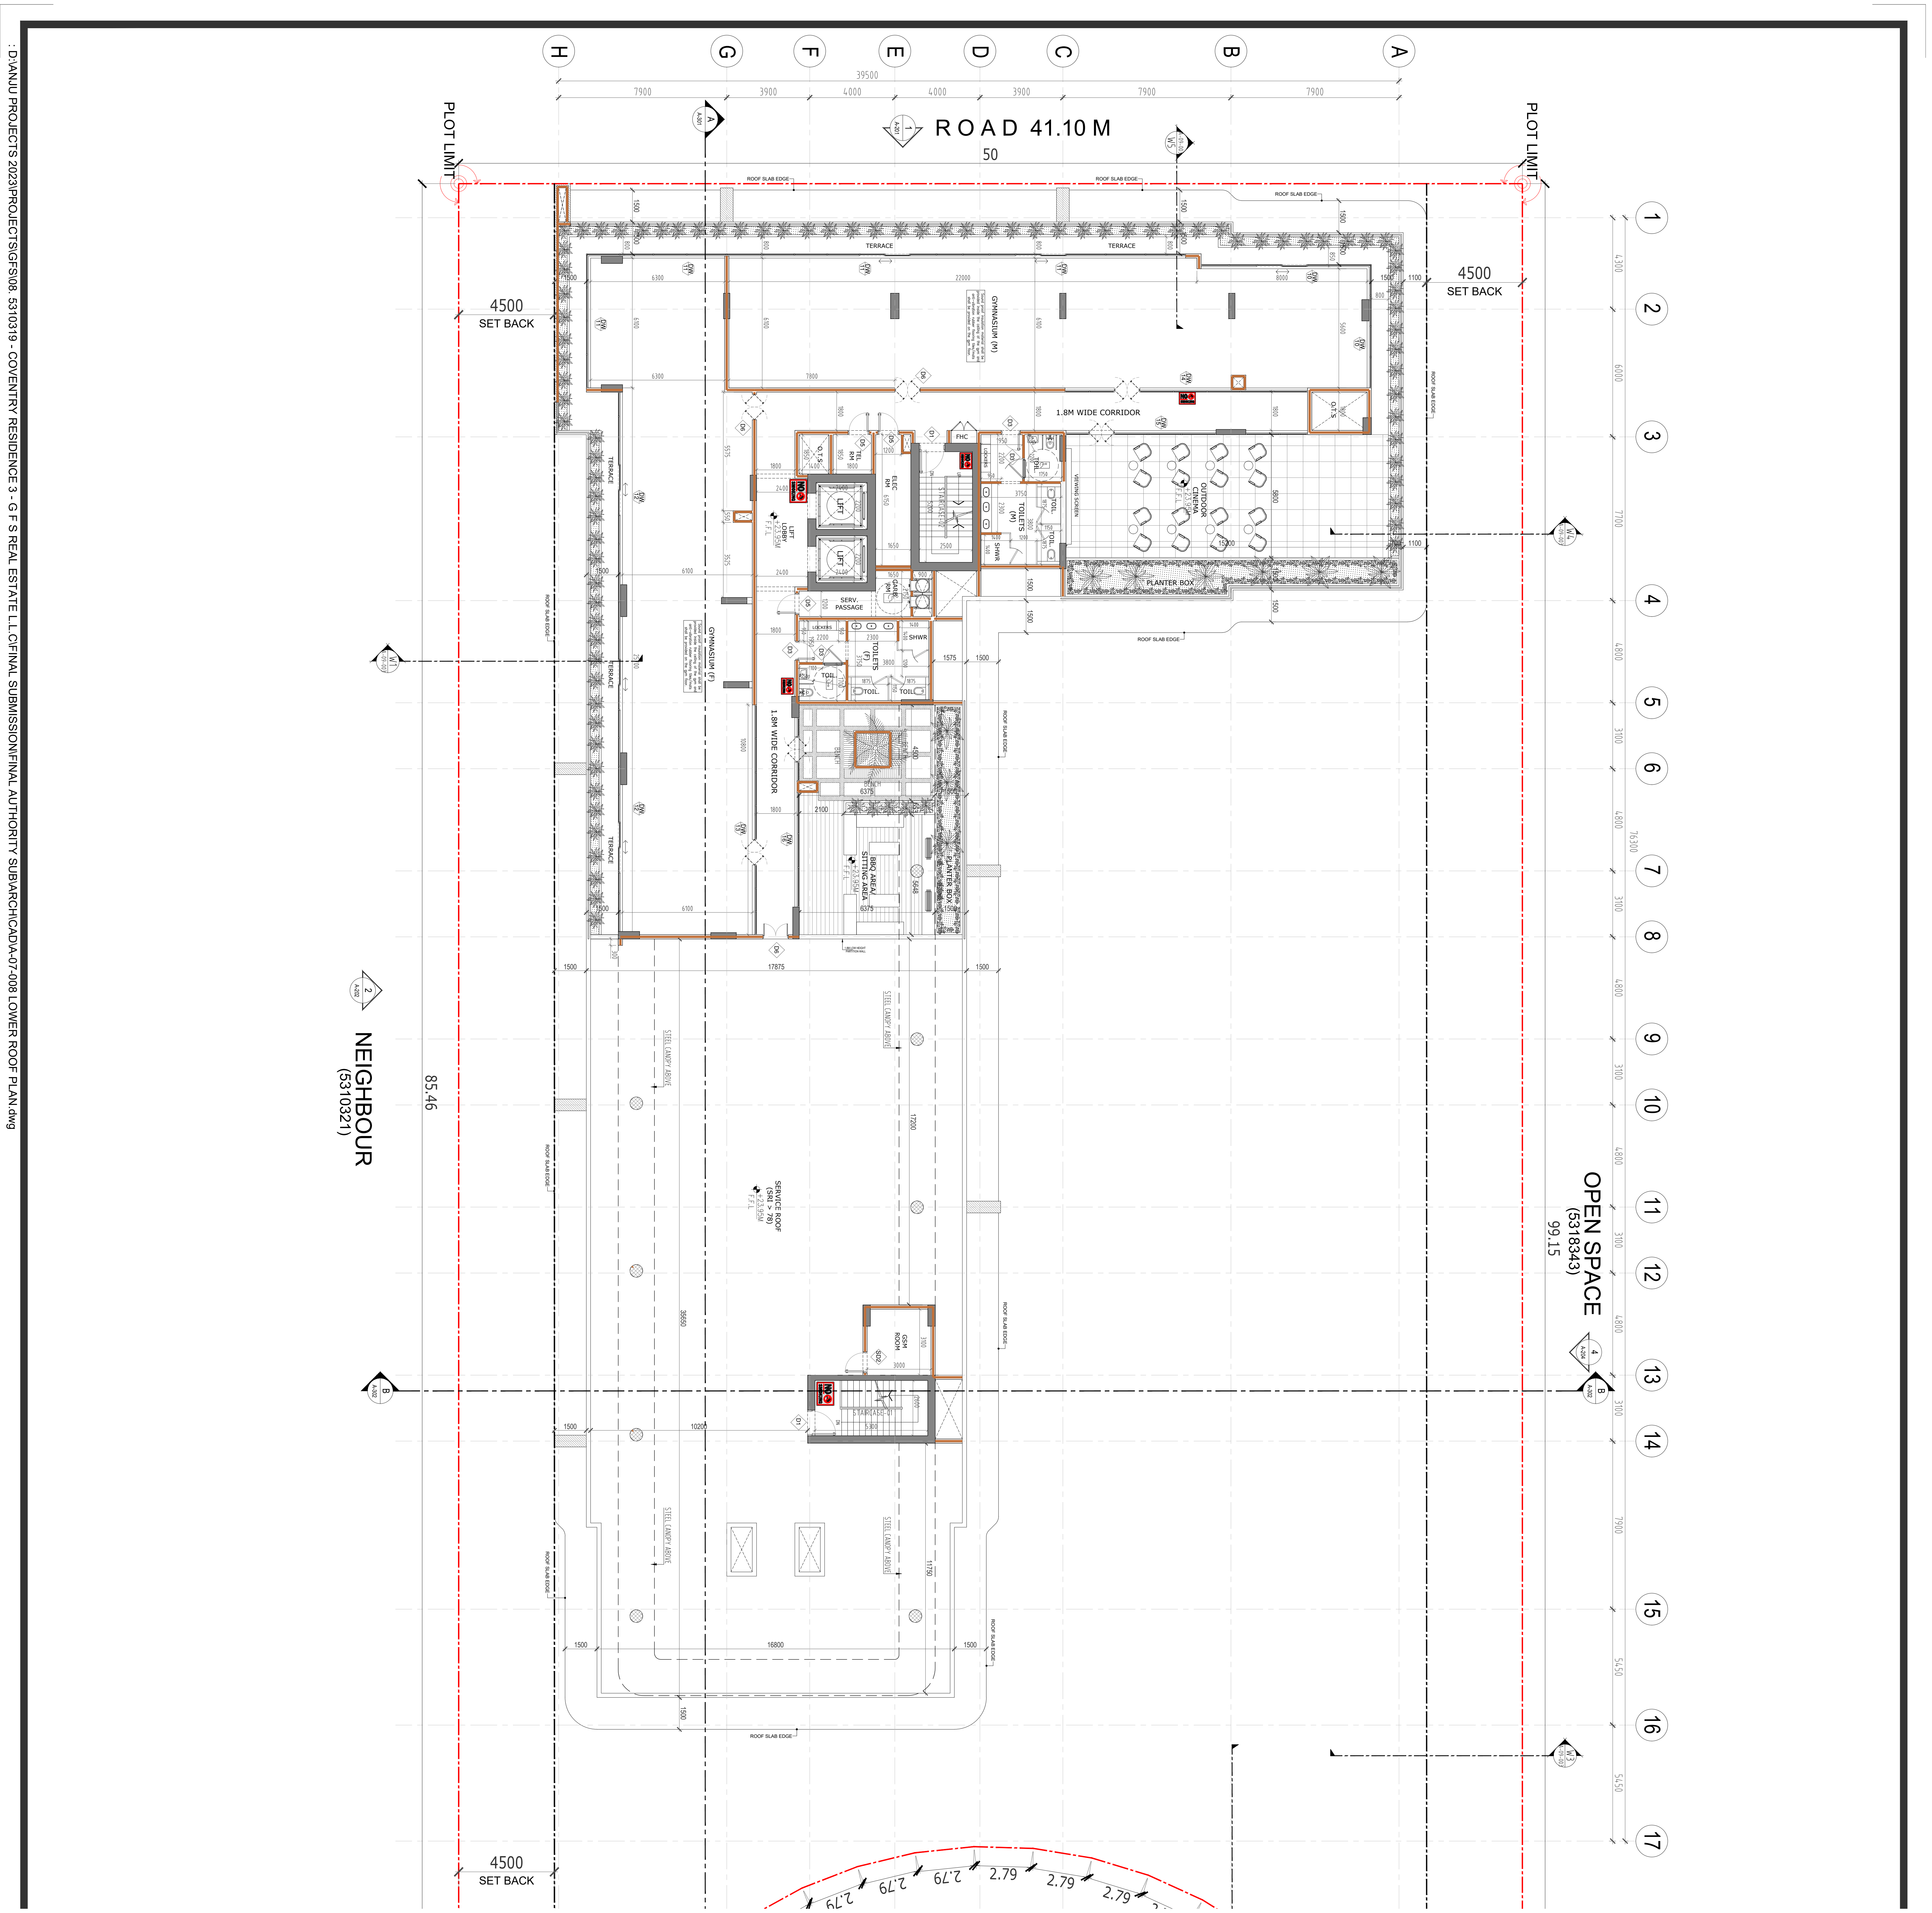

H
G
F
E
D
C
B
A
ROAD 41.10 M
50
PLOT LIMIT
PLOT LIMIT
4500
SET BACK
4500
SET BACK
4500
SET BACK
1
2
3
4
5
6
7
8
9
10
11
12
13
14
15
16
17
TERRACE
GYMNASIUM (M)
GYMNASIUM (F)
1.8M WIDE CORRIDOR
LIFT
LIFT
TOILETS
SERV. PASSAGE
PLANTER BOX
OUTDOOR CINEMA
SERVICE ROOF
85.46
NEIGHBOUR
(5310321)
OPEN SPACE
(5318343)
99.15
2.79
D:\ANJU PROJECTS 2023\PROJECTS\GFS\08. 5310319 - COVENTRY RESIDENCE 3 - G F S REAL ESTATE L.L.C\FINAL SUBMISSION\FINAL AUTHORITY SUBMISSION\ARCH\CAD\A-07-008 LOWER ROOF PLAN.dwg

Legend

Masonry

🟫 D-A 120.90 m2
🟫 D-B 22.11 m2
🟫 D-C 416.67 m2

SECTION G - Thermal and Moisture Protection

Project: PROPOSED RESIDENTIAL BUILDING (B+G+5+ROOF)
Building: None

Drawing: A-07-008
Filename: Architecture/A1/A-07-008 LOWER ROOF PLAN.pdf

: D:\ANJU PROJECTS 2023\PROJECTS\GFS\08. 5310319 - COVENTRY RESIDENCE 3 - G F S REAL ESTATE L.L.C\FINAL SUBMISSION\FINAL AUTHORITY SUB\ARCH\CAD\A-07-008 LOWER ROOF PLAN.dwg

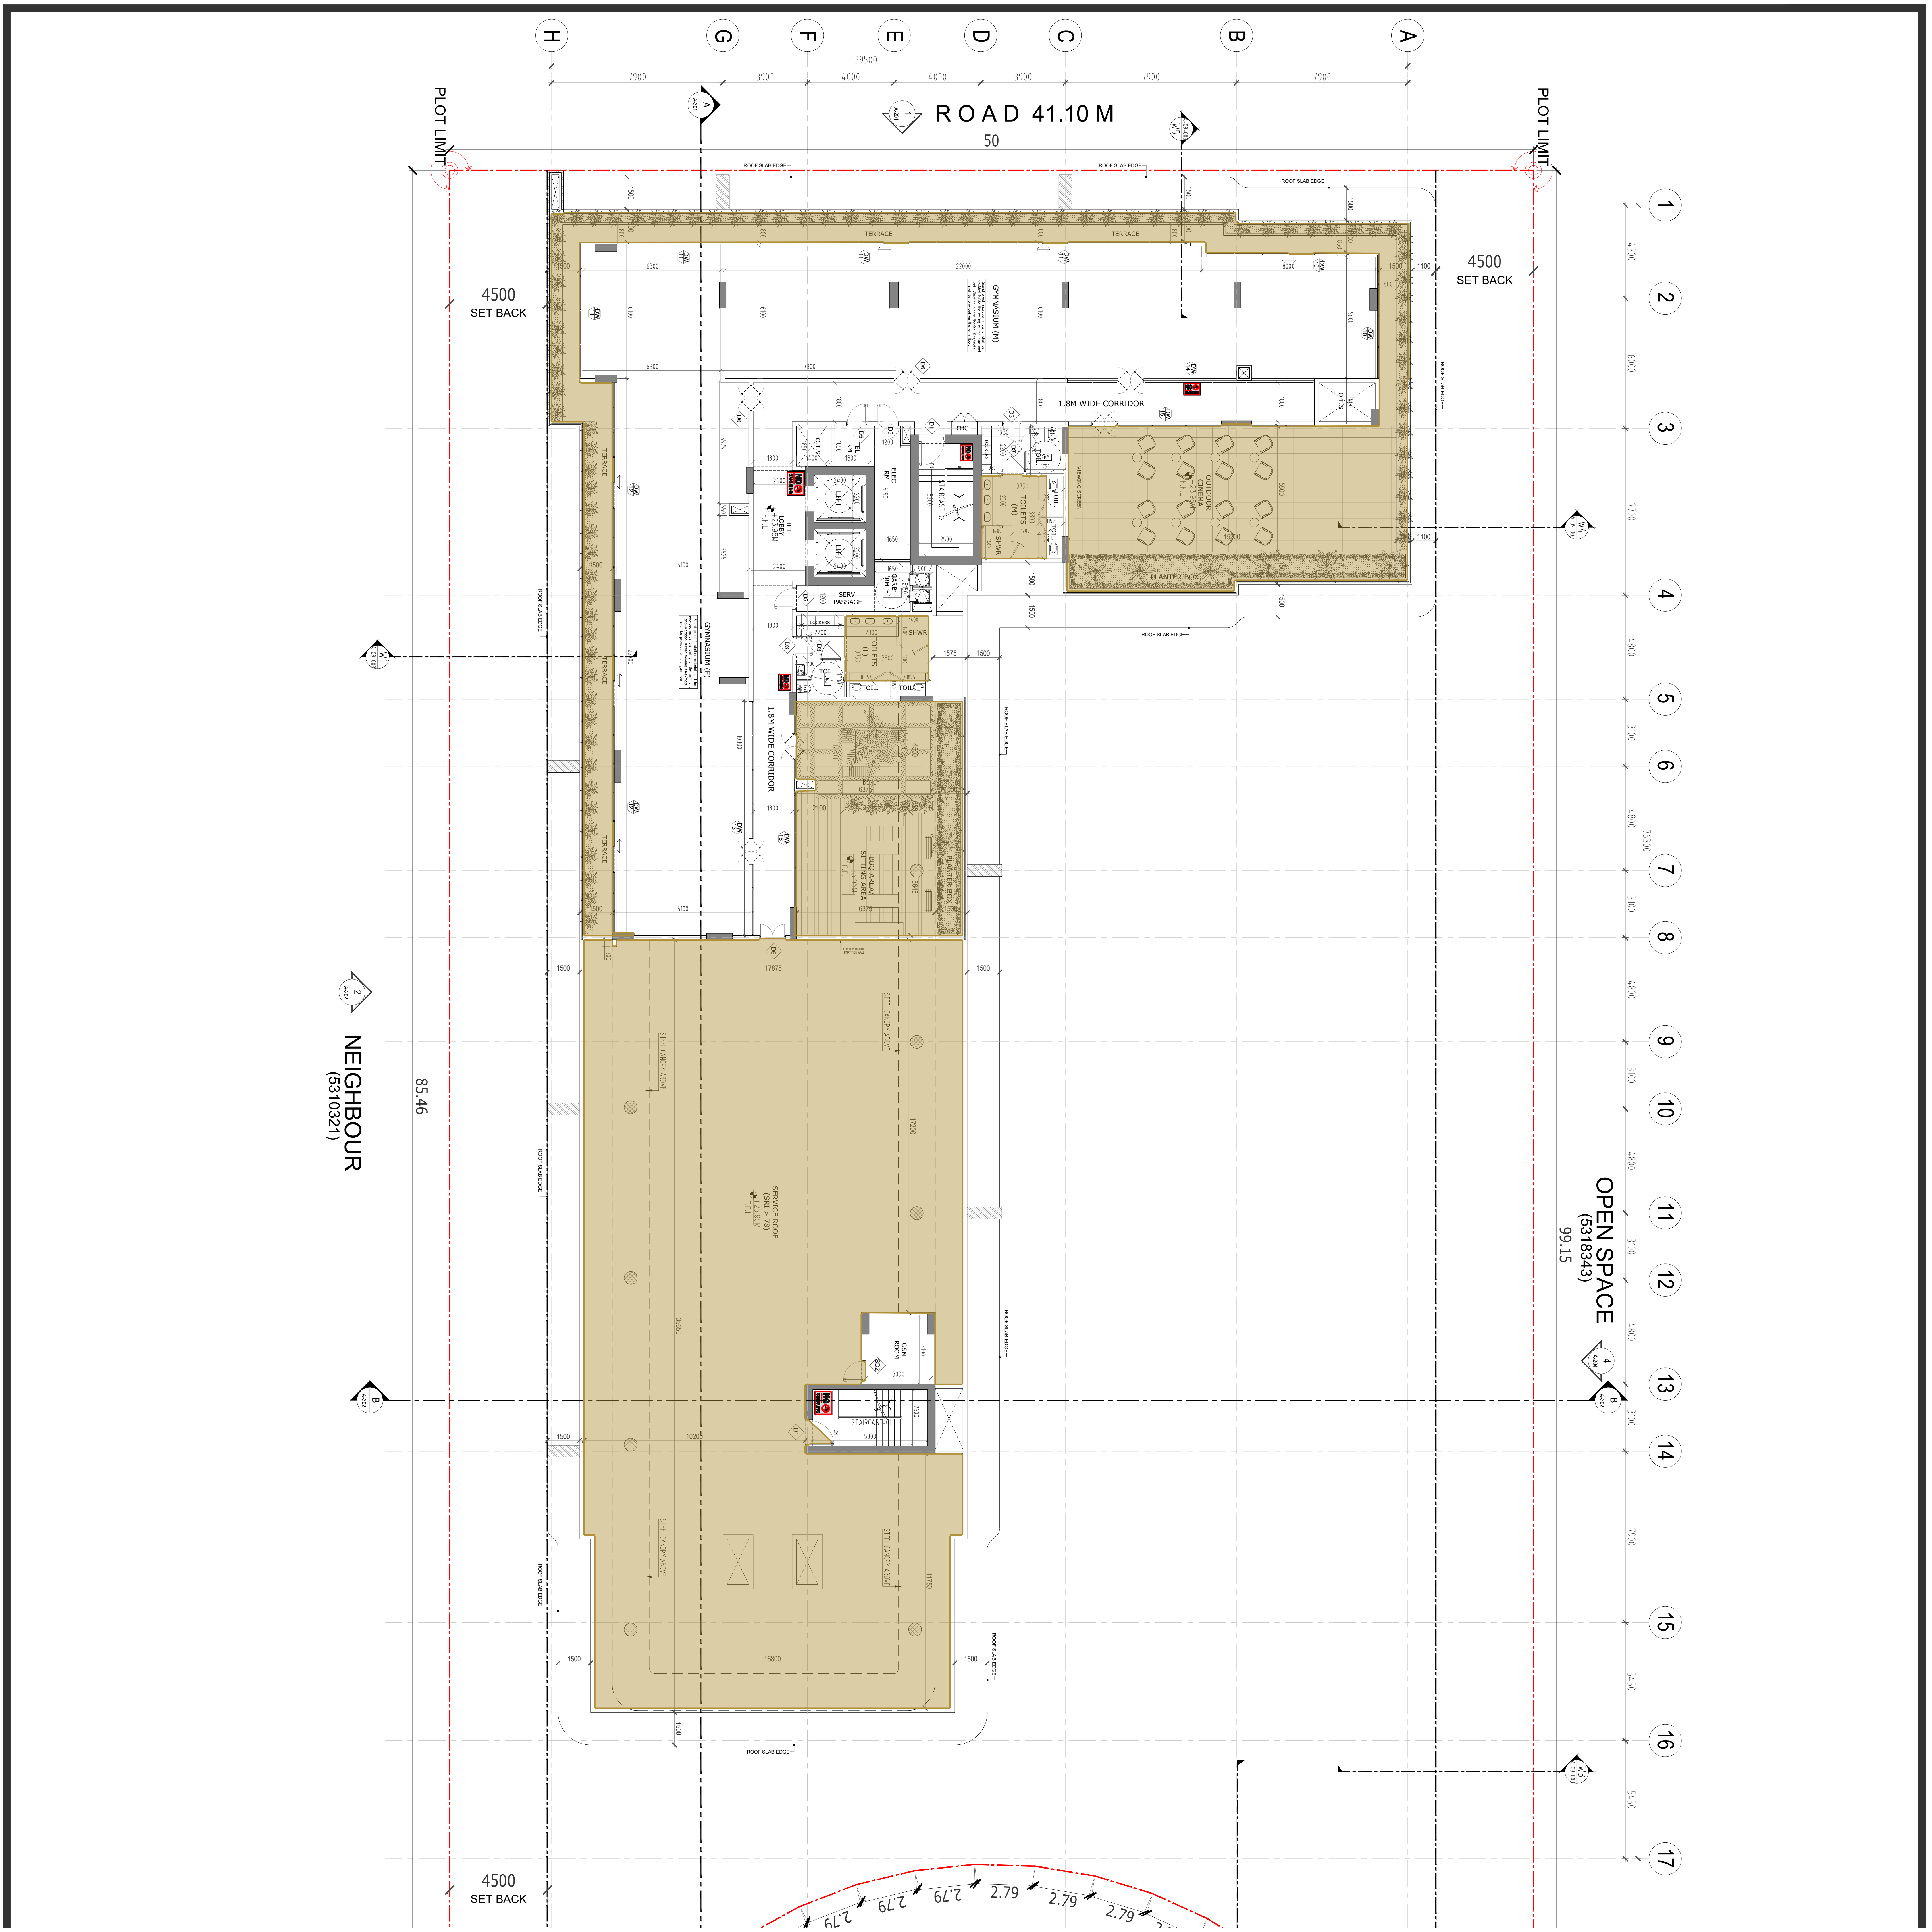
H
G
F
E
D
C
B
A
39500
7900
3900
4000
4000
3900
7900
7900
ROAD 41.10 M
50
PLOT LIMIT
PLOT LIMIT
4500
SET BACK
4500
SET BACK
4500
SET BACK
TERRACE
GYMNASIUM (M)
1.8M WIDE CORRIDOR
LIFT
LIFT
TOILETS
OUTDOOR CINEMA
PLANTER BOX
SERV. PASSAGE
GYMNASIUM (F)
1.8M WIDE CORRIDOR
BBQ AREA/ SITTING AREA
PLANTER BOX
SERVICE ROOF
GEN ROOM
1
2
3
4
5
6
7
8
9
10
11
12
13
14
15
16
17
NEIGHBOUR
(5310321)
85.46
OPEN SPACE
(5318343)
99.15
2.79
2.79
2.79
2.79
2.79
2.79
2.79

Legend

Thermal and Moisture Protection

- ▨ G-A 22.85 m2
- ▨ G-B 878.40 m2

CostX

SECTION J - Finishes

Project: PROPOSED RESIDENTIAL BUILDING (B+G+5+ROOF)
Building: None

Drawing: A-07-008
Filename: Architecture/A1/A-07-008 LOWER ROOF PLAN.pdf

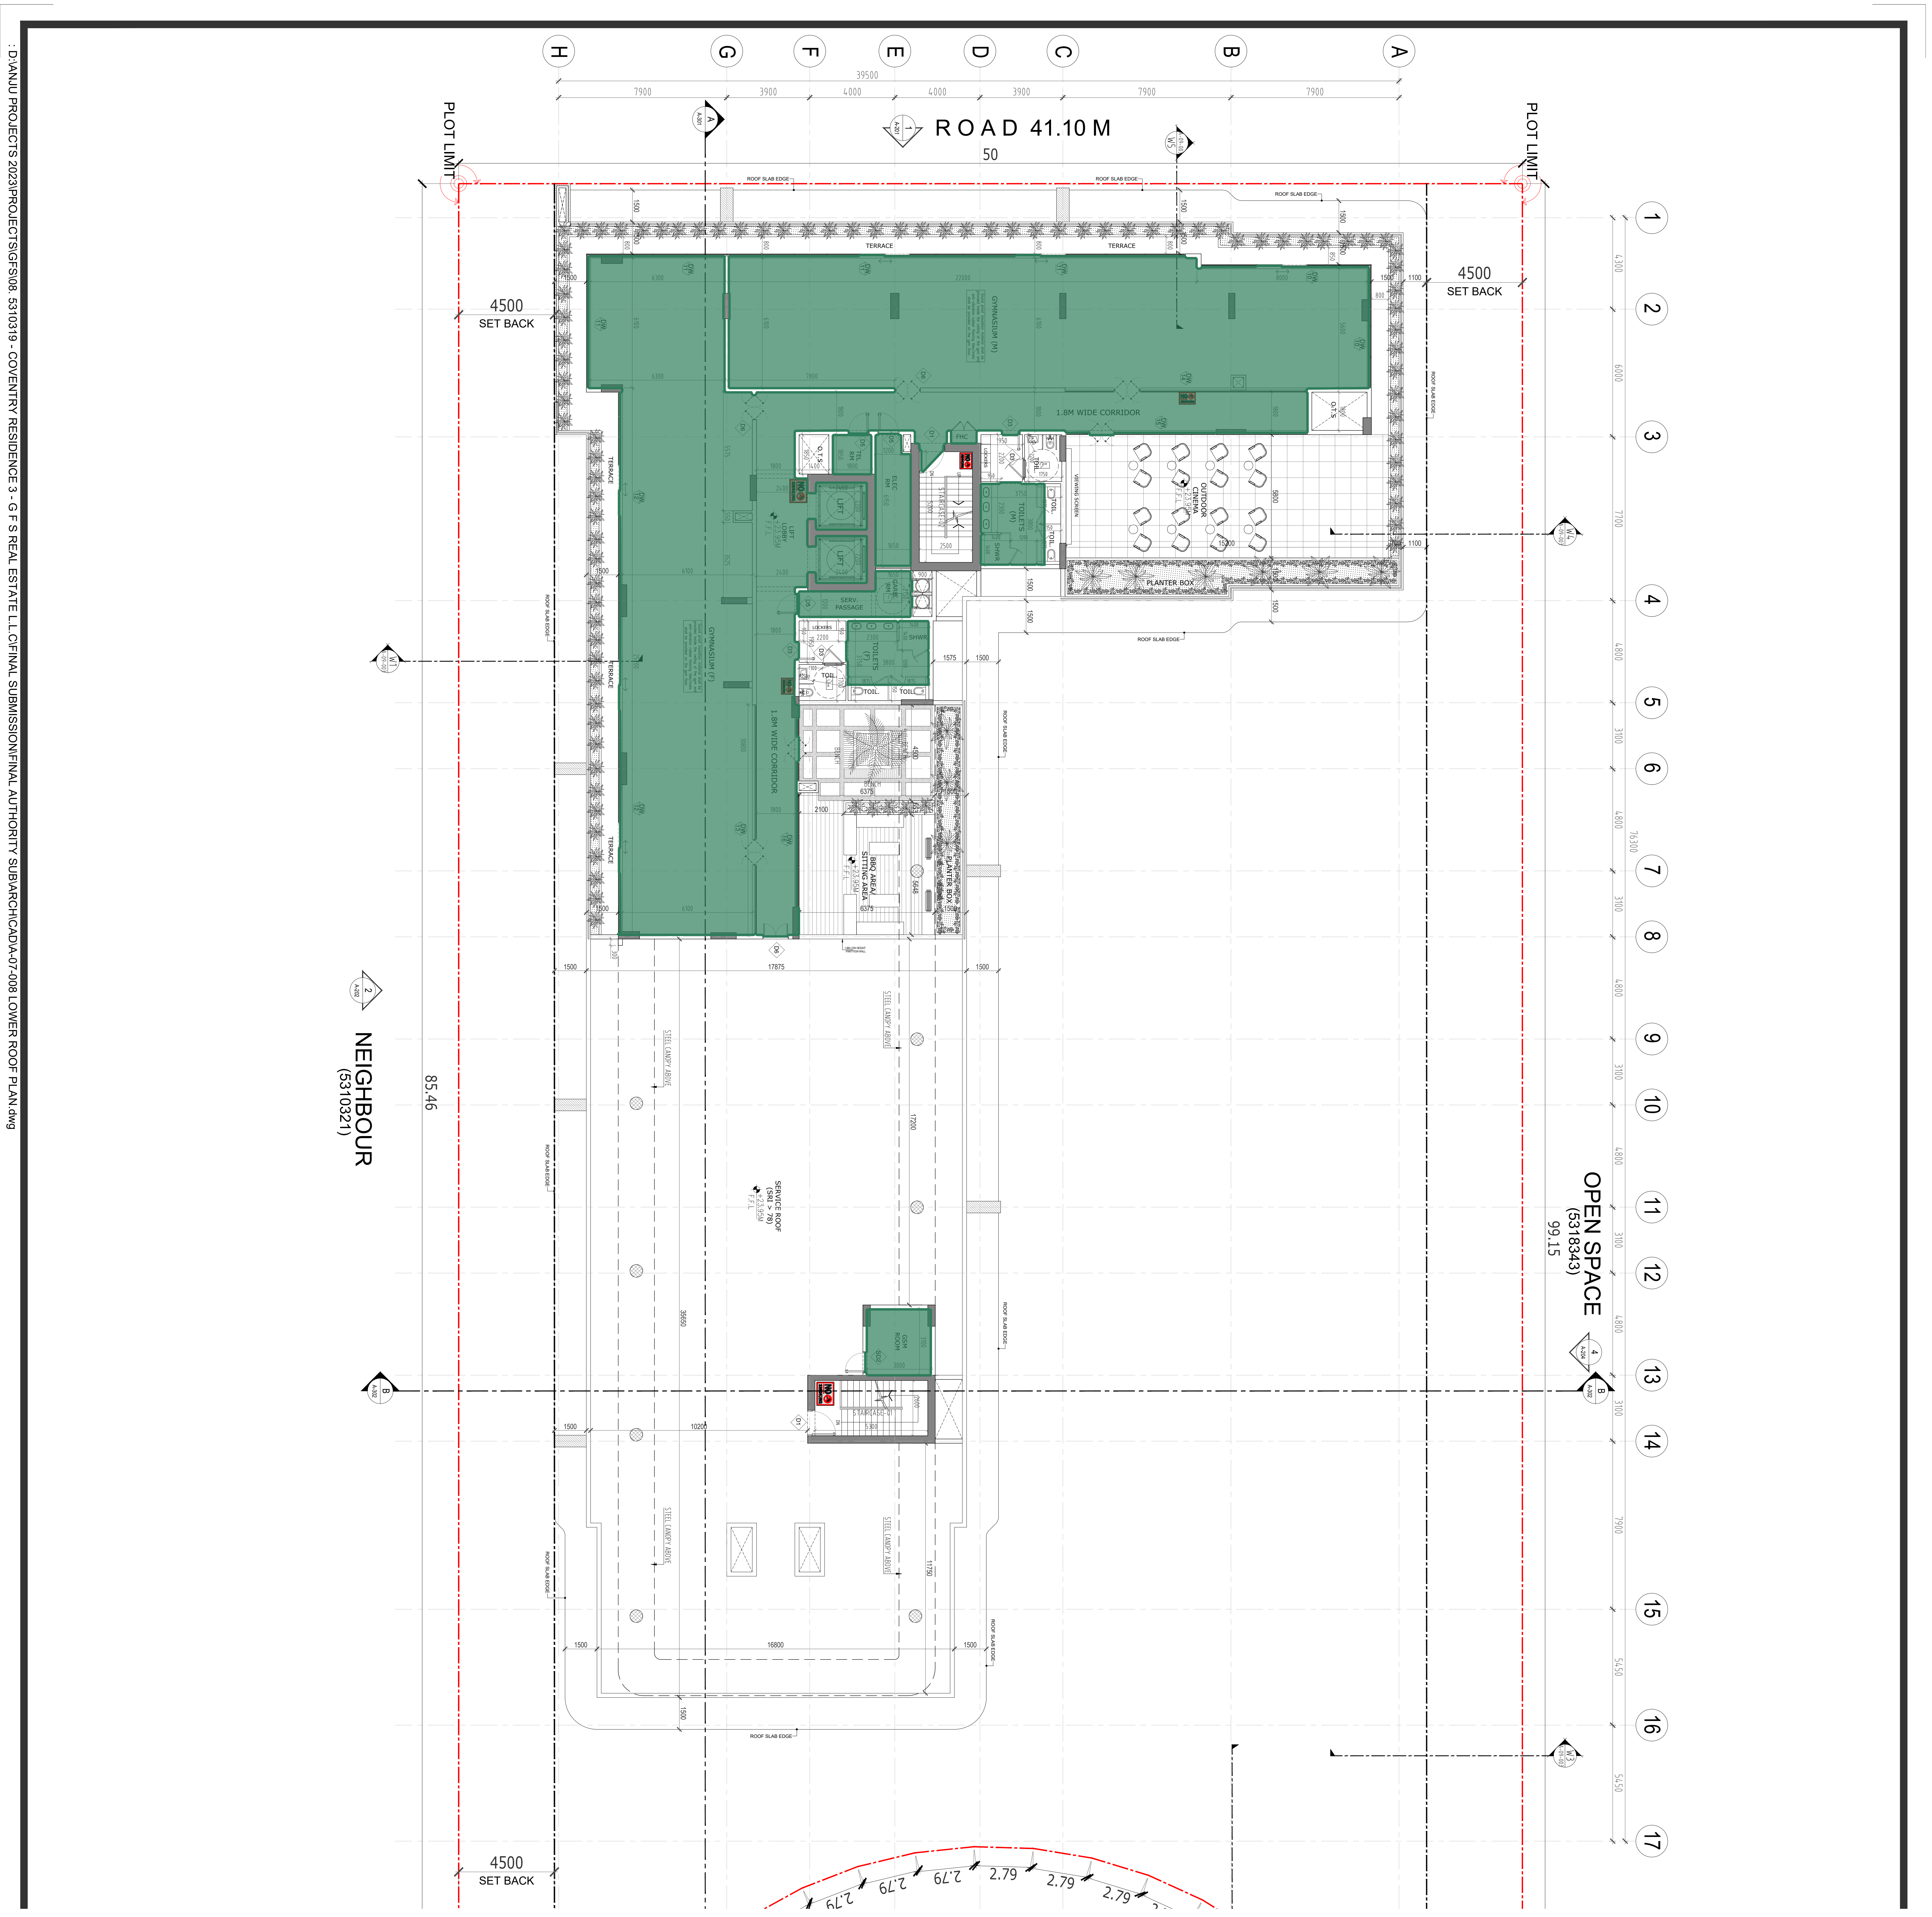

: D:\ANJU PROJECTS 2023\PROJECTS\GFS\08. 5310319 - COVENTRY RESIDENCE 3 - G F S REAL ESTATE L.L.C\FINAL SUBMISSION\FINAL AUTHORITY SUB\ARCH\CAD\A-07-008 LOWER ROOF PLAN.dwg
H
G
F
E
D
C
B
A
39500
7900
3900
4000
4000
3900
7900
7900
ROAD 41.10 M
50
PLOT LIMIT
PLOT LIMIT
4500
SET BACK
4500
SET BACK
4500
SET BACK
TERRACE
TERRACE
1.8M WIDE CORRIDOR
1.8M WIDE CORRIDOR
PLANTER BOX
PLANTER BOX
LIFT
LIFT
TOILETS
SERVICE ROOF
NEIGHBOUR
(5310321)
85.46
OPEN SPACE
(5318343)
99.15
1
2
3
4
5
6
7
8
9
10
11
12
13
14
15
16
17
2.79
2.79
2.79
2.79
2.79
2.79

Legend

Finishes

🟩	J-A 518.77 m2
🟩	J-B 22.85 m2
🟩	J-C 518.77 m2
🟩	J-D 22.85 m2
🟩	J-E 767.62 m2
🟩	J-F 91.89 m2
🟩	J-G 224.69 m
🟩	J-H 27.43 m