SECTION D - Masonry

Project: PROPOSED RESIDENTIAL BUILDING (B+G+5+ROOF)
Building: None

Drawing: A-07-004
Filename: Architecture/A1/A-07-004 FIRST FLOOR PLAN.pdf

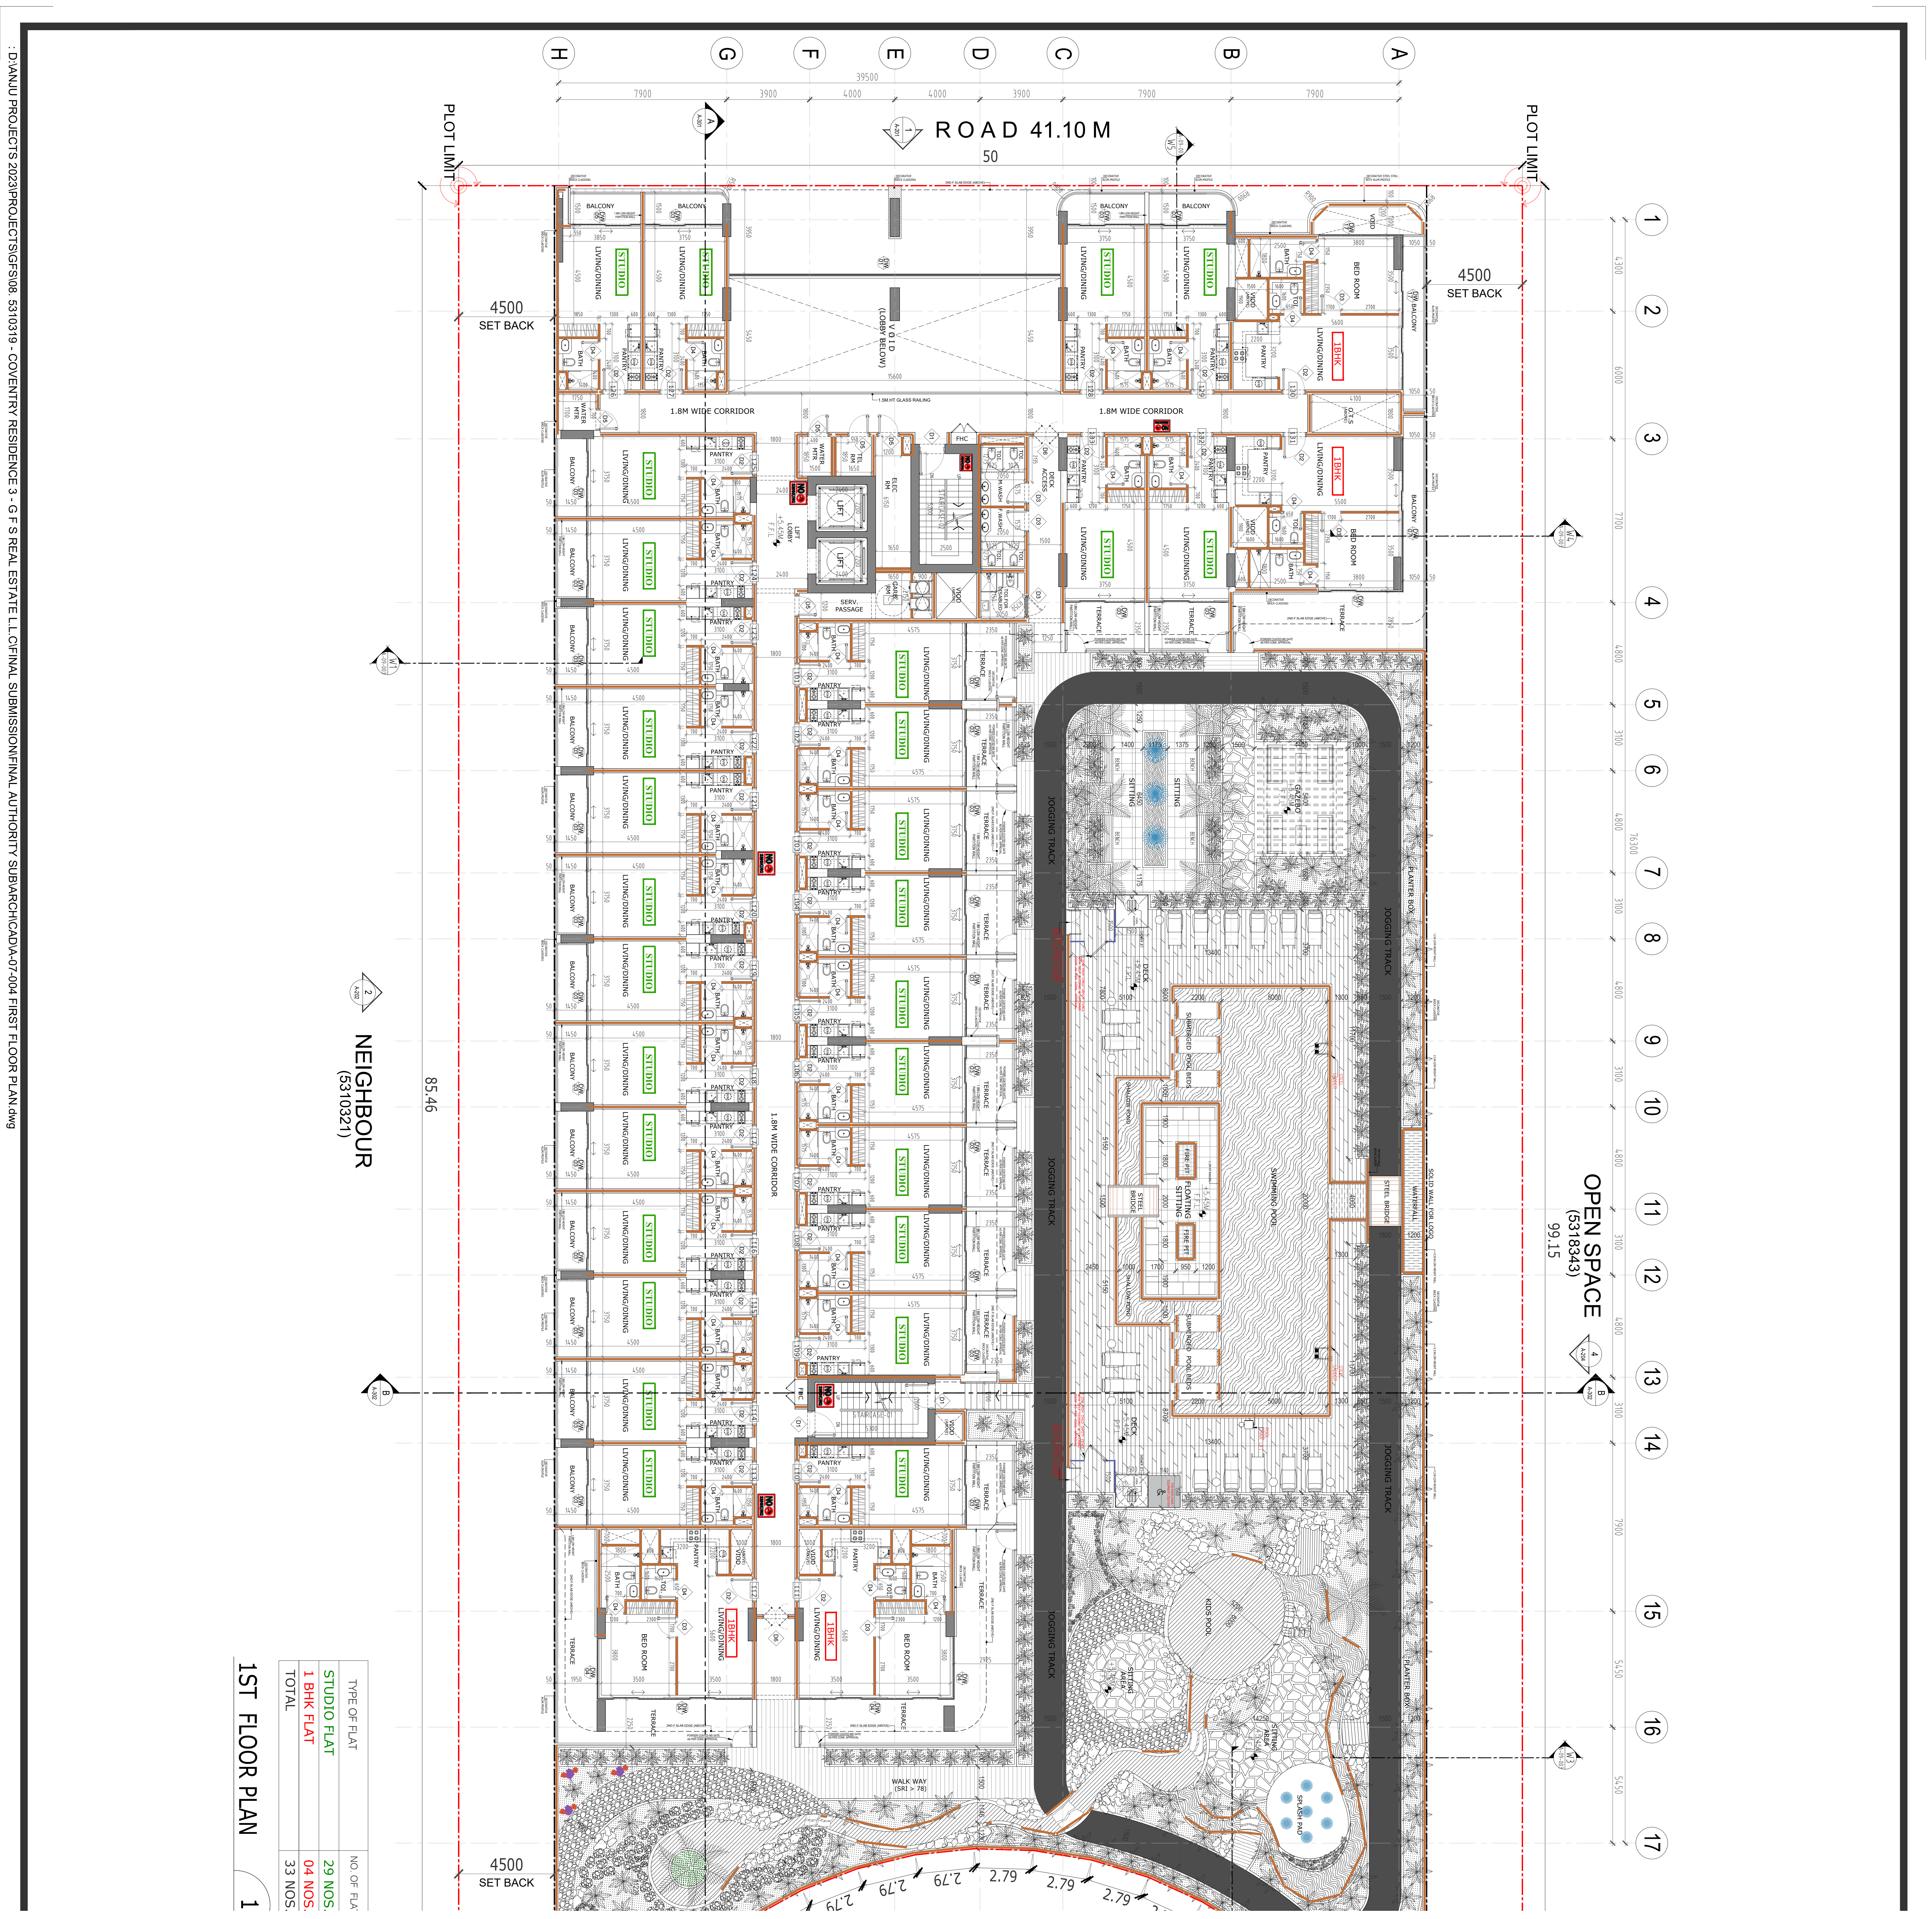
: D:\ANJU PROJECTS 2023\PROJECTS\GFS\08. 5310319 - COVENTRY RESIDENCE 3 - G F S REAL ESTATE L.L.C\FINAL SUBMISSION\FINAL AUTHORITY SUBM\ARCHICAD\A-07-004 FIRST FLOOR PLAN.dwg
H
G
F
E
D
C
B
A
39500
7900
3900
4000
4000
3900
7900
7900
ROAD 41.10 M
50
PLOT LIMIT
PLOT LIMIT
4500
SET BACK
4500
SET BACK
4500
SET BACK
1
2
3
4
5
6
7
8
9
10
11
12
13
14
15
16
17
BALCONY
LIVING/DINING
STUDIO
1BHK
BED ROOM
PANTRY
BATH
TERRACE
VOID (LOBBY BELOW)
1.8M WIDE CORRIDOR
LIFT
SERV. PASSAGE
JOGGING TRACK
PLANTER BOX
SWIMMING POOL
FLOATING SEATING
KIDS POOL
SPLASH PAD
WALK WAY
NEIGHBOUR (5310321)
85.46
OPEN SPACE (5318343)
99.15
2.79
TYPE OF FLAT
NO. OF FLA
STUDIO FLAT
29 NOS.
1 BHK FLAT
04 NOS.
TOTAL
33 NOS.
1ST FLOOR PLAN

Legend

Masonry

🟫	D-A	1,200.21 m2
🟫	D-B	172.81 m2
🟫	D-C	2,245.09 m2

CostX

SECTION G - Thermal and Moisture Protection

Project: PROPOSED RESIDENTIAL BUILDING (B+G+5+ROOF)
Building: None

Drawing: A-07-004
Filename: Architecture/A1/A-07-004 FIRST FLOOR PLAN.pdf

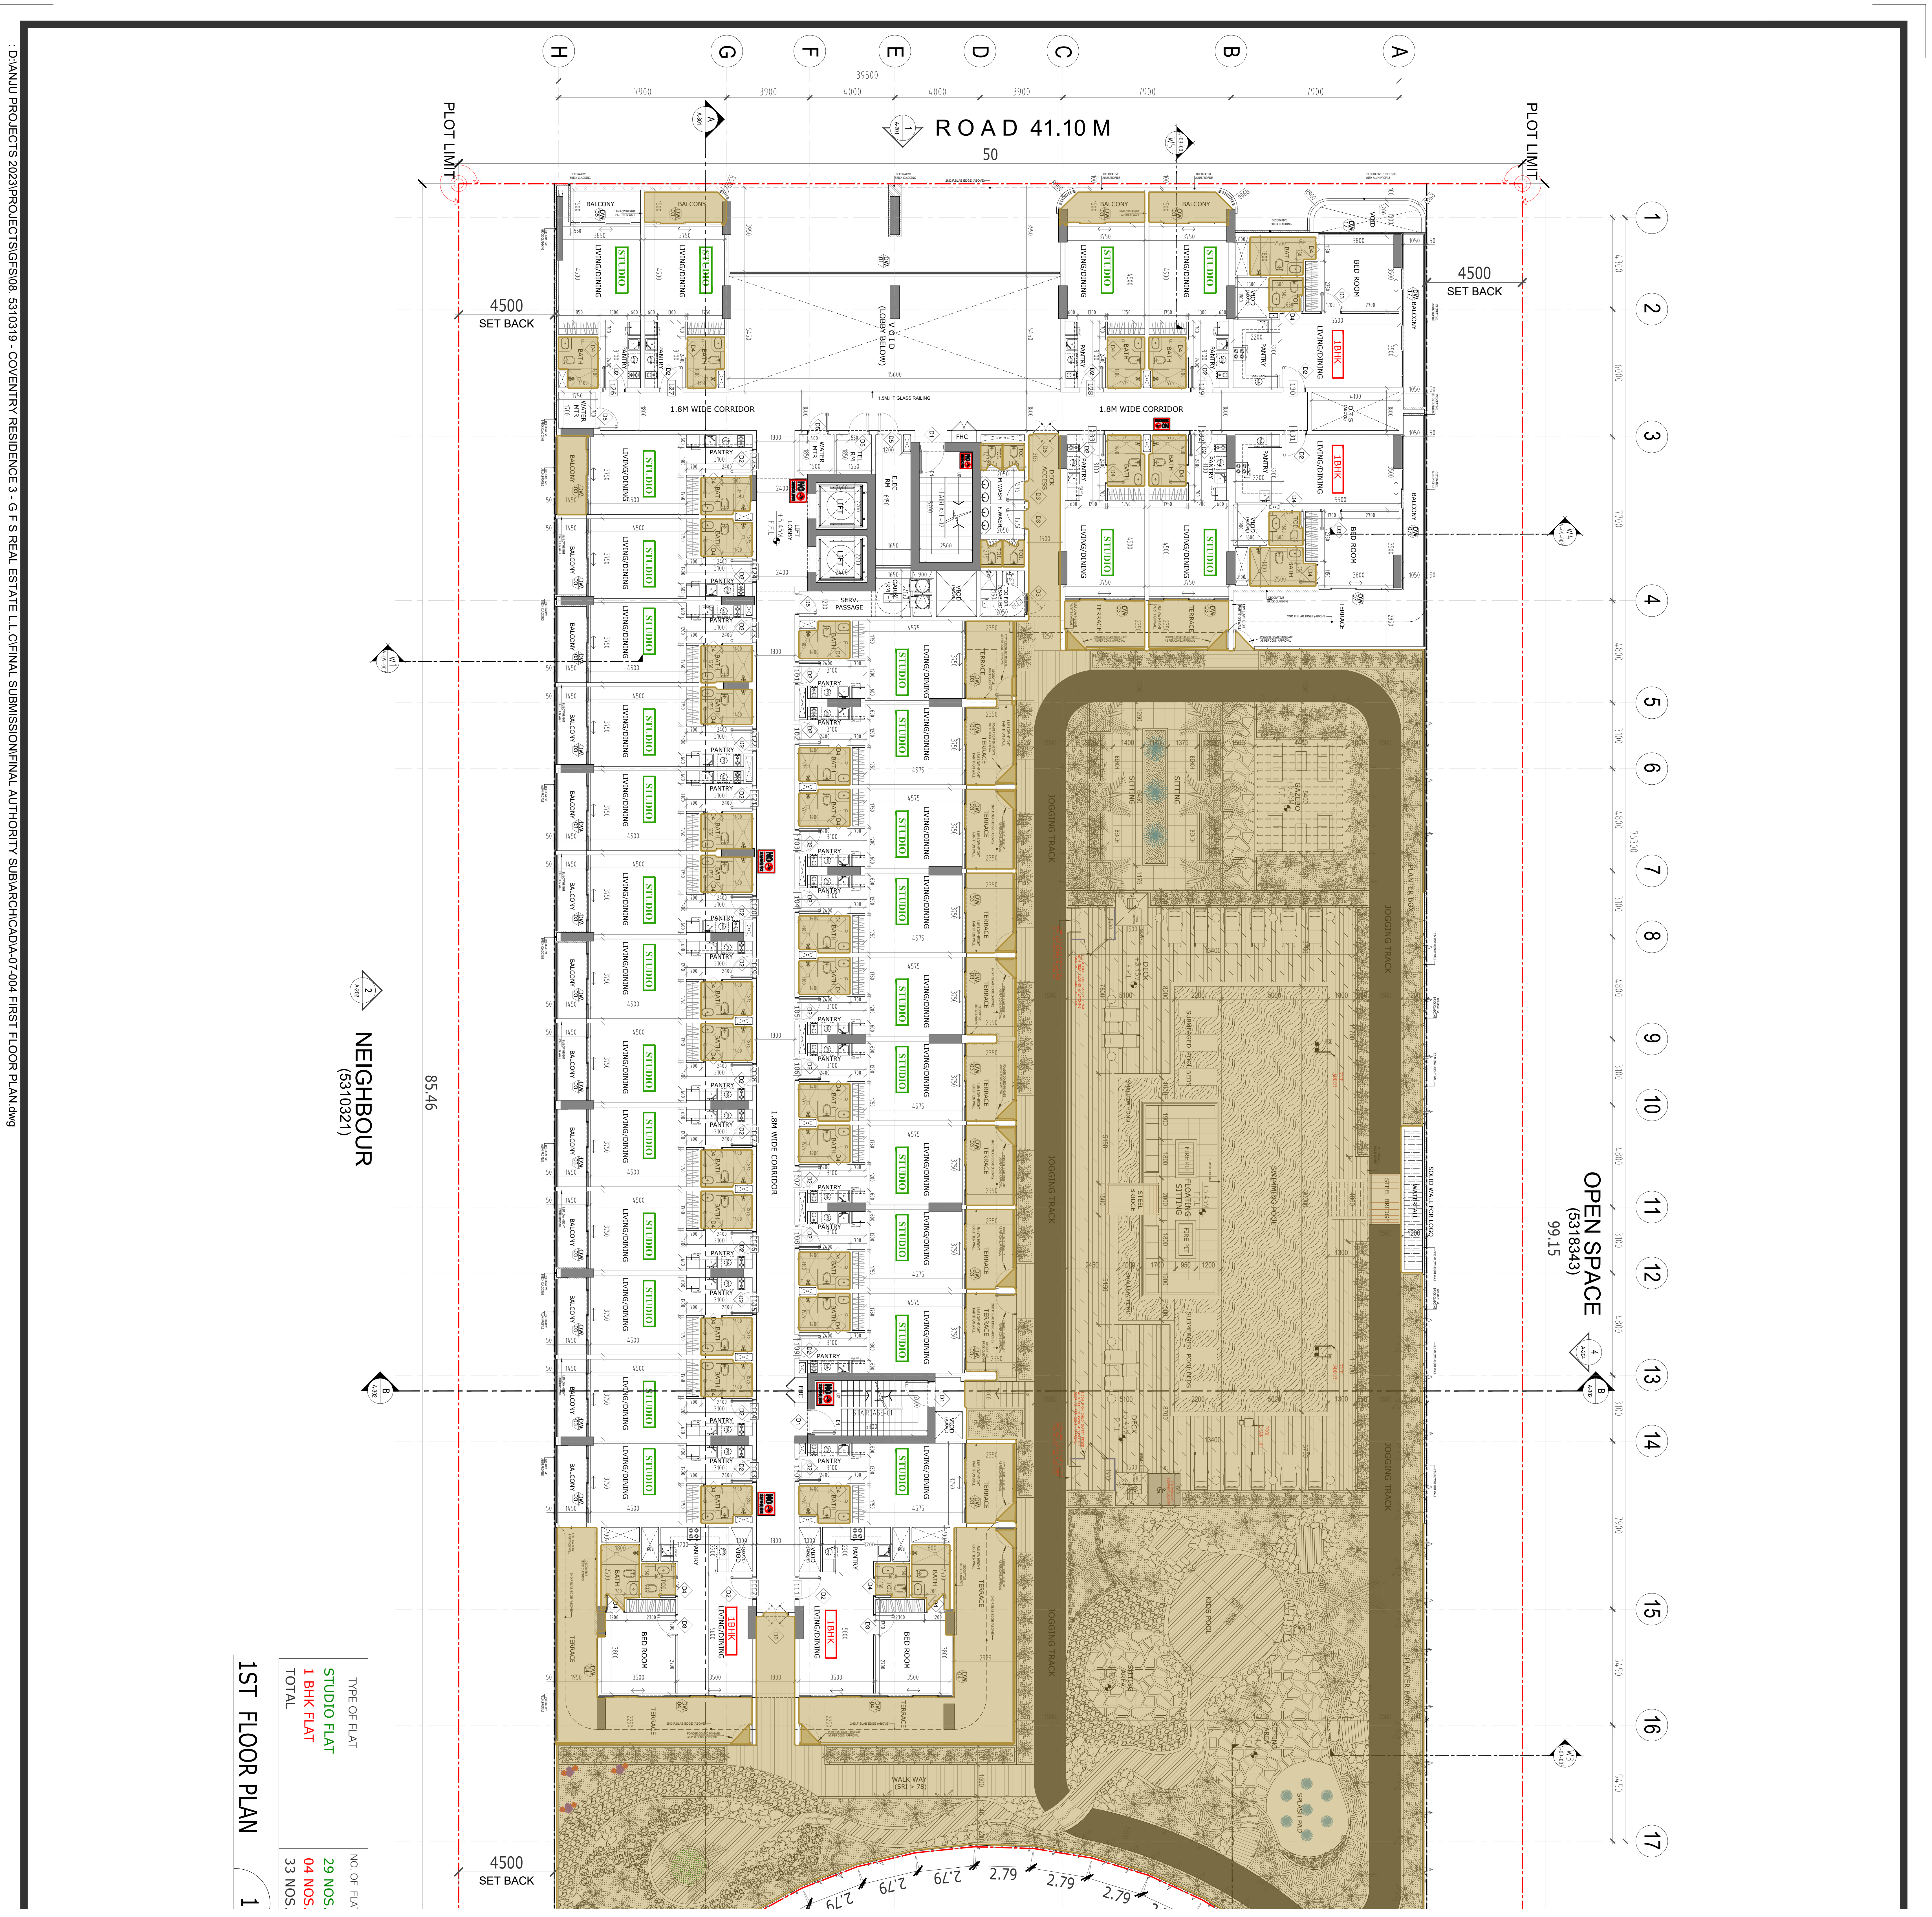
: D:\ANJU PROJECTS 2023\PROJECTS\GFS\08. 5310319 - COVENTRY RESIDENCE 3 - G F S REAL ESTATE L.L.C\FINAL SUBMISSION\FINAL AUTHORITY SUBM\ARCHICAD\A-07-004 FIRST FLOOR PLAN.dwg
H
G
F
E
D
C
B
A
39500
7900
3900
4000
4000
3900
7900
7900
ROAD 41.10 M
50
PLOT LIMIT
PLOT LIMIT
4500
SET BACK
4500
SET BACK
4500
SET BACK
1
2
3
4
5
6
7
8
9
10
11
12
13
14
15
16
17
BALCONY
STUDIO
LIVING/DINING
PANTRY
BATH
BED ROOM
1BHK
TERRACE
1.8M WIDE CORRIDOR
V O I D (LOBBY BELOW)
LIFT
SERV. PASSAGE
JOGGING TRACK
WALK WAY
NEIGHBOUR (5310321)
85.46
OPEN SPACE (5318343)
99.15
2.79
TYPE OF FLAT
STUDIO FLAT
1 BHK FLAT
TOTAL
NO. OF FLA
29 NOS.
04 NOS.
33 NOS.
1ST FLOOR PLAN
1

Legend

Thermal and Moisture Protection

▨ G-A 150.47 m2

▨ G-B 1,302.95 m2

SECTION J - Finishes

Project: PROPOSED RESIDENTIAL BUILDING (B+G+5+ROOF)
Building: None

Drawing: A-07-004
Filename: Architecture/A1/A-07-004 FIRST FLOOR PLAN.pdf

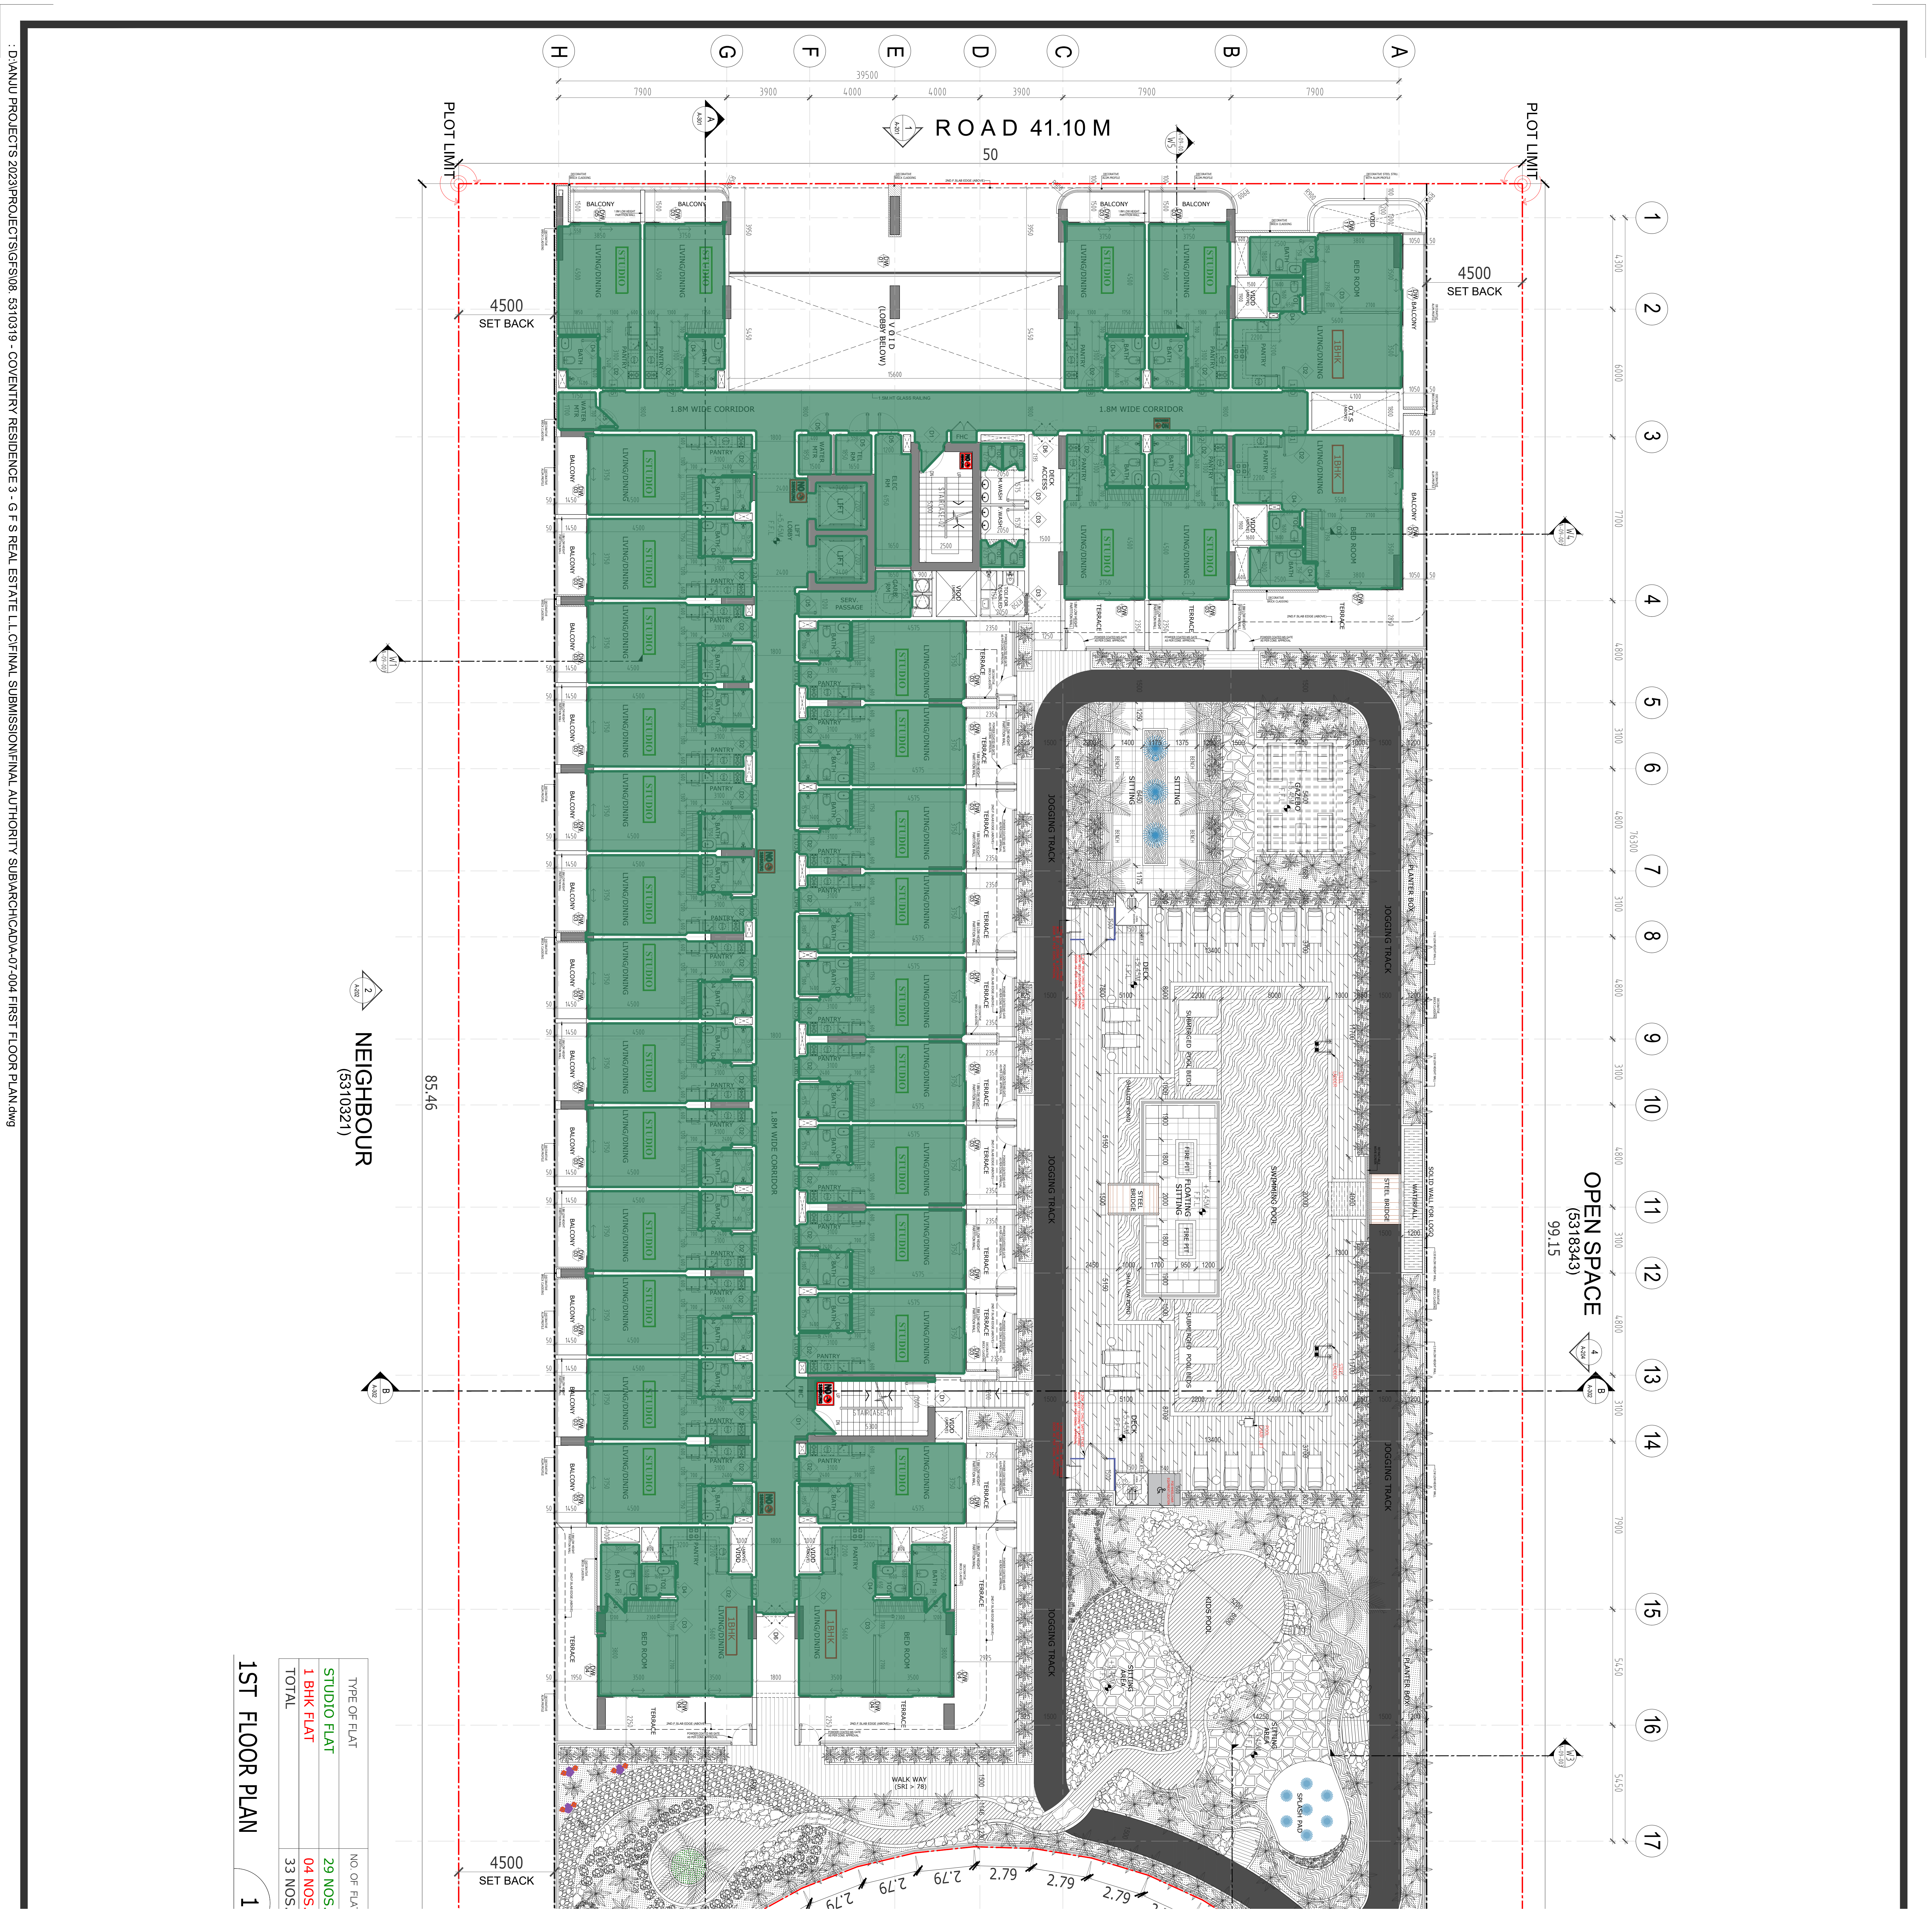

: D:\ANJU PROJECTS 2023\PROJECTS\GFS\08. 5310319 - COVENTRY RESIDENCE 3 - G F S REAL ESTATE L.L.C\FINAL SUBMISSION\FINAL AUTHORITY SUBM\ARCHICAD\A-07-004 FIRST FLOOR PLAN.dwg
H
G
F
E
D
C
B
A
39500
7900
3900
4000
4000
3900
7900
7900
ROAD 41.10 M
50
PLOT LIMIT
PLOT LIMIT
4500
SET BACK
4500
SET BACK
4500
SET BACK
1.8M WIDE CORRIDOR
1.8M WIDE CORRIDOR
1.8M WIDE CORRIDOR
VOID
(LOBBY BELOW)
STUDIO
LIVING/DINING
BALCONY
TERRACE
PANTRY
BED ROOM
JOGGING TRACK
PLANTER BOX
SWIMMING POOL
KIDS POOL
SPLASH PAD
WALK WAY
NEIGHBOUR
(5310321)
85.46
OPEN SPACE
(5318343)
99.15
1
2
3
4
5
6
7
8
9
10
11
12
13
14
15
16
17
2.79
1ST FLOOR PLAN
TYPE OF FLAT
NO. OF FLATS
STUDIO FLAT
29 NOS.
1 BHK FLAT
04 NOS.
TOTAL
33 NOS.

Legend

Finishes

- 🟩 J-A 1,077.31 m2
- 🟩 J-B 150.47 m2
- 🟩 J-C 1,077.31 m2
- 🟩 J-D 150.47 m2
- 🟩 J-E 3,585.89 m2
- 🟩 J-F 1,055.10 m2
- 🟩 J-G 979.54 m
- 🟩 J-H 282.00 m