
SECTION D - Masonry

Project: PROPOSED RESIDENTIAL BUILDING (B+G+5+ROOF)
Building: None

Drawing: A-07-005
Filename: Architecture/A1/A-07-005 2ND FLOOR PLAN.pdf

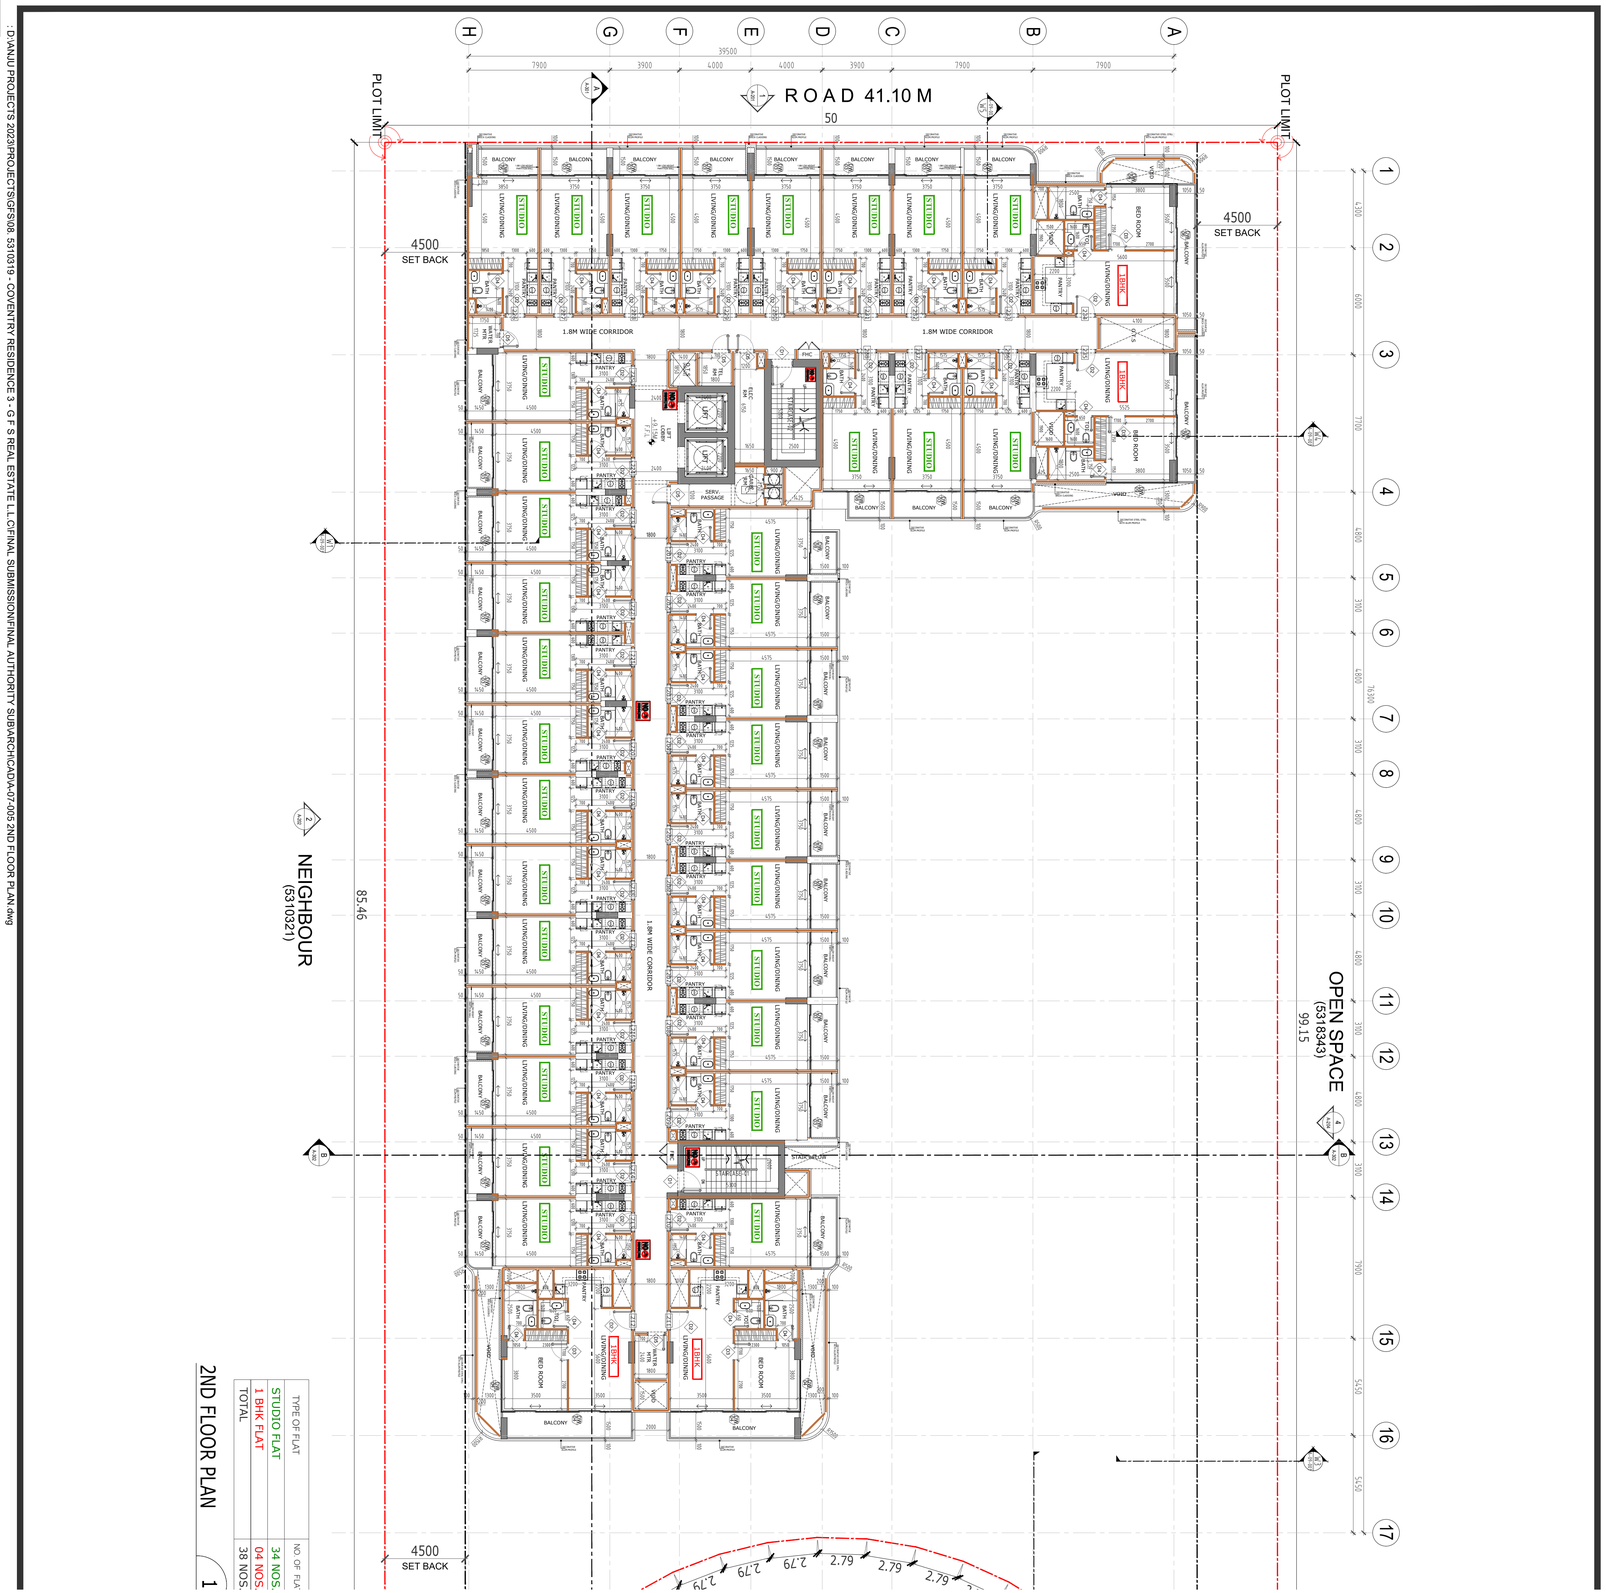

TYPE OF FLAT	NO. OF FLA
STUDIO FLAT	34 NOS
1 BHK FLAT	04 NOS
TOTAL	38 NOS

2ND FLOOR PLAN

1

Legend

Masonry


- D-A 1,083.28 m2
- D-B 25.52 m2
- D-C 1,671.14 m2

: D:\ANJU PROJECTS 2023\PROJECTS\GF\SO8 5310319 - COVENTRY RESIDENCE 3 - G F S REAL ESTATE L.L.C\FINAL SUBMISSION\FINAL AUTHORITY SUB\ARCH\CAD\A-07-005 2ND FLOOR PLAN.dwg

CostX

Project: PROPOSED RESIDENTIAL BUILDING (B+G+5+ROOF)
Building: None

Drawing: A-07-005
Filename: Architecture/A1/A-07-005 2ND FLOOR PLAN.pdf

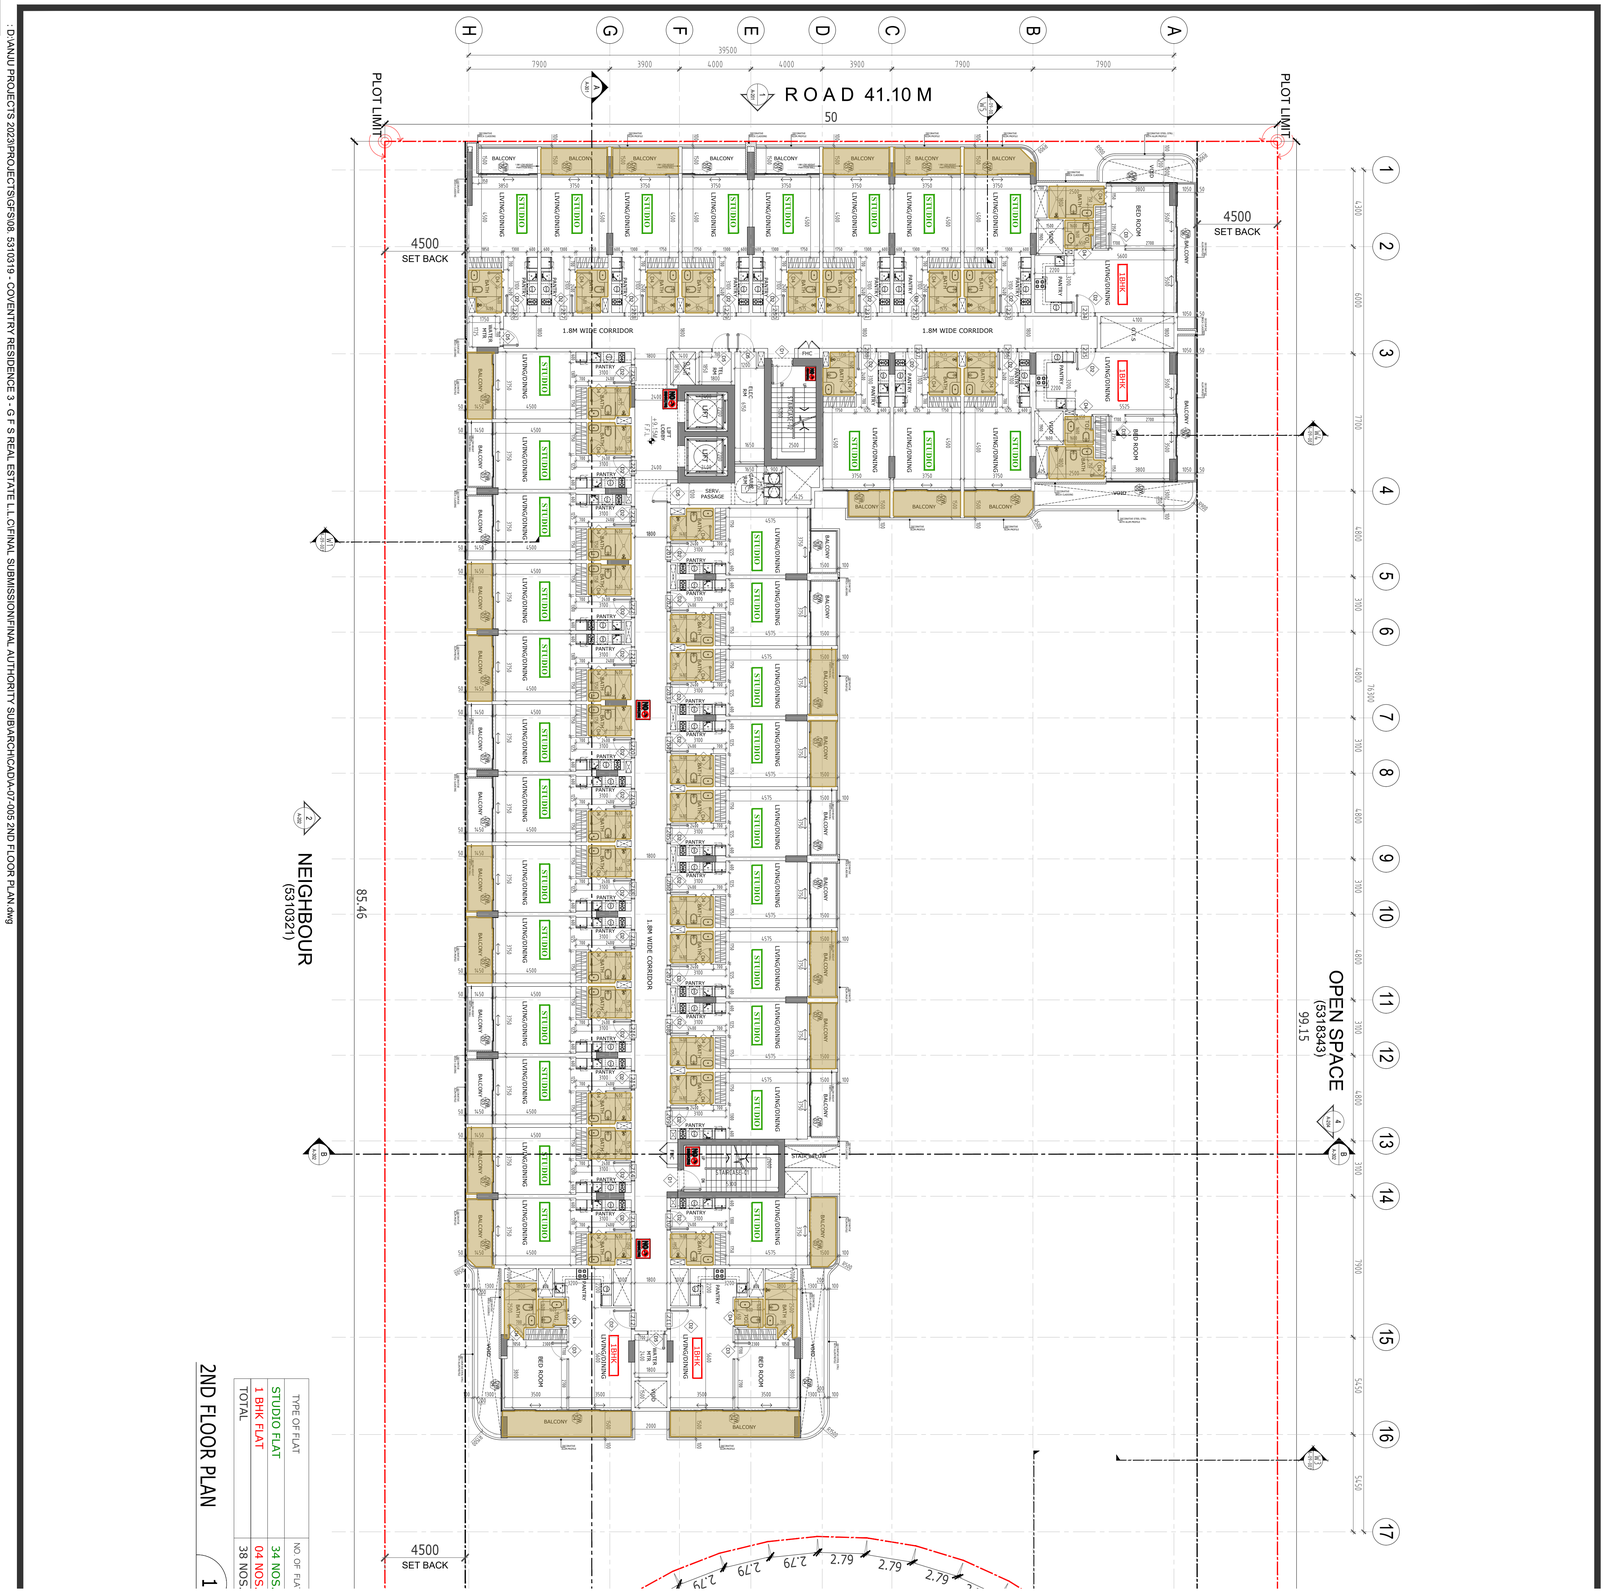

TYPE OF FLAT	NO. OF FLA
STUDIO FLAT	34 NOS.
1 BHK FLAT	04 NOS.
TOTAL	38 NOS.

2ND FLOOR PLAN

Legend

Thermal and Moisture Protection


- G-A 166.13 m2
- G-B 123.48 m2

: D:\ANJU PROJECTS 2023\PROJECTS\GF5\08 5310319 - COVENTRY RESIDENCE 3 - G F 5 REAL ESTATE L.L.C\FINAL SUBMISSION\FINAL AUTHORITY SUBARCH\CADA\A-07-005 2ND FLOOR PLAN.dwg

SECTION J - Finishes

Project: PROPOSED RESIDENTIAL BUILDING (B+G+5+ROOF)
Building: None

Drawing: A-07-005
Filename: Architecture/A1/A-07-005 2ND FLOOR PLAN.pdf

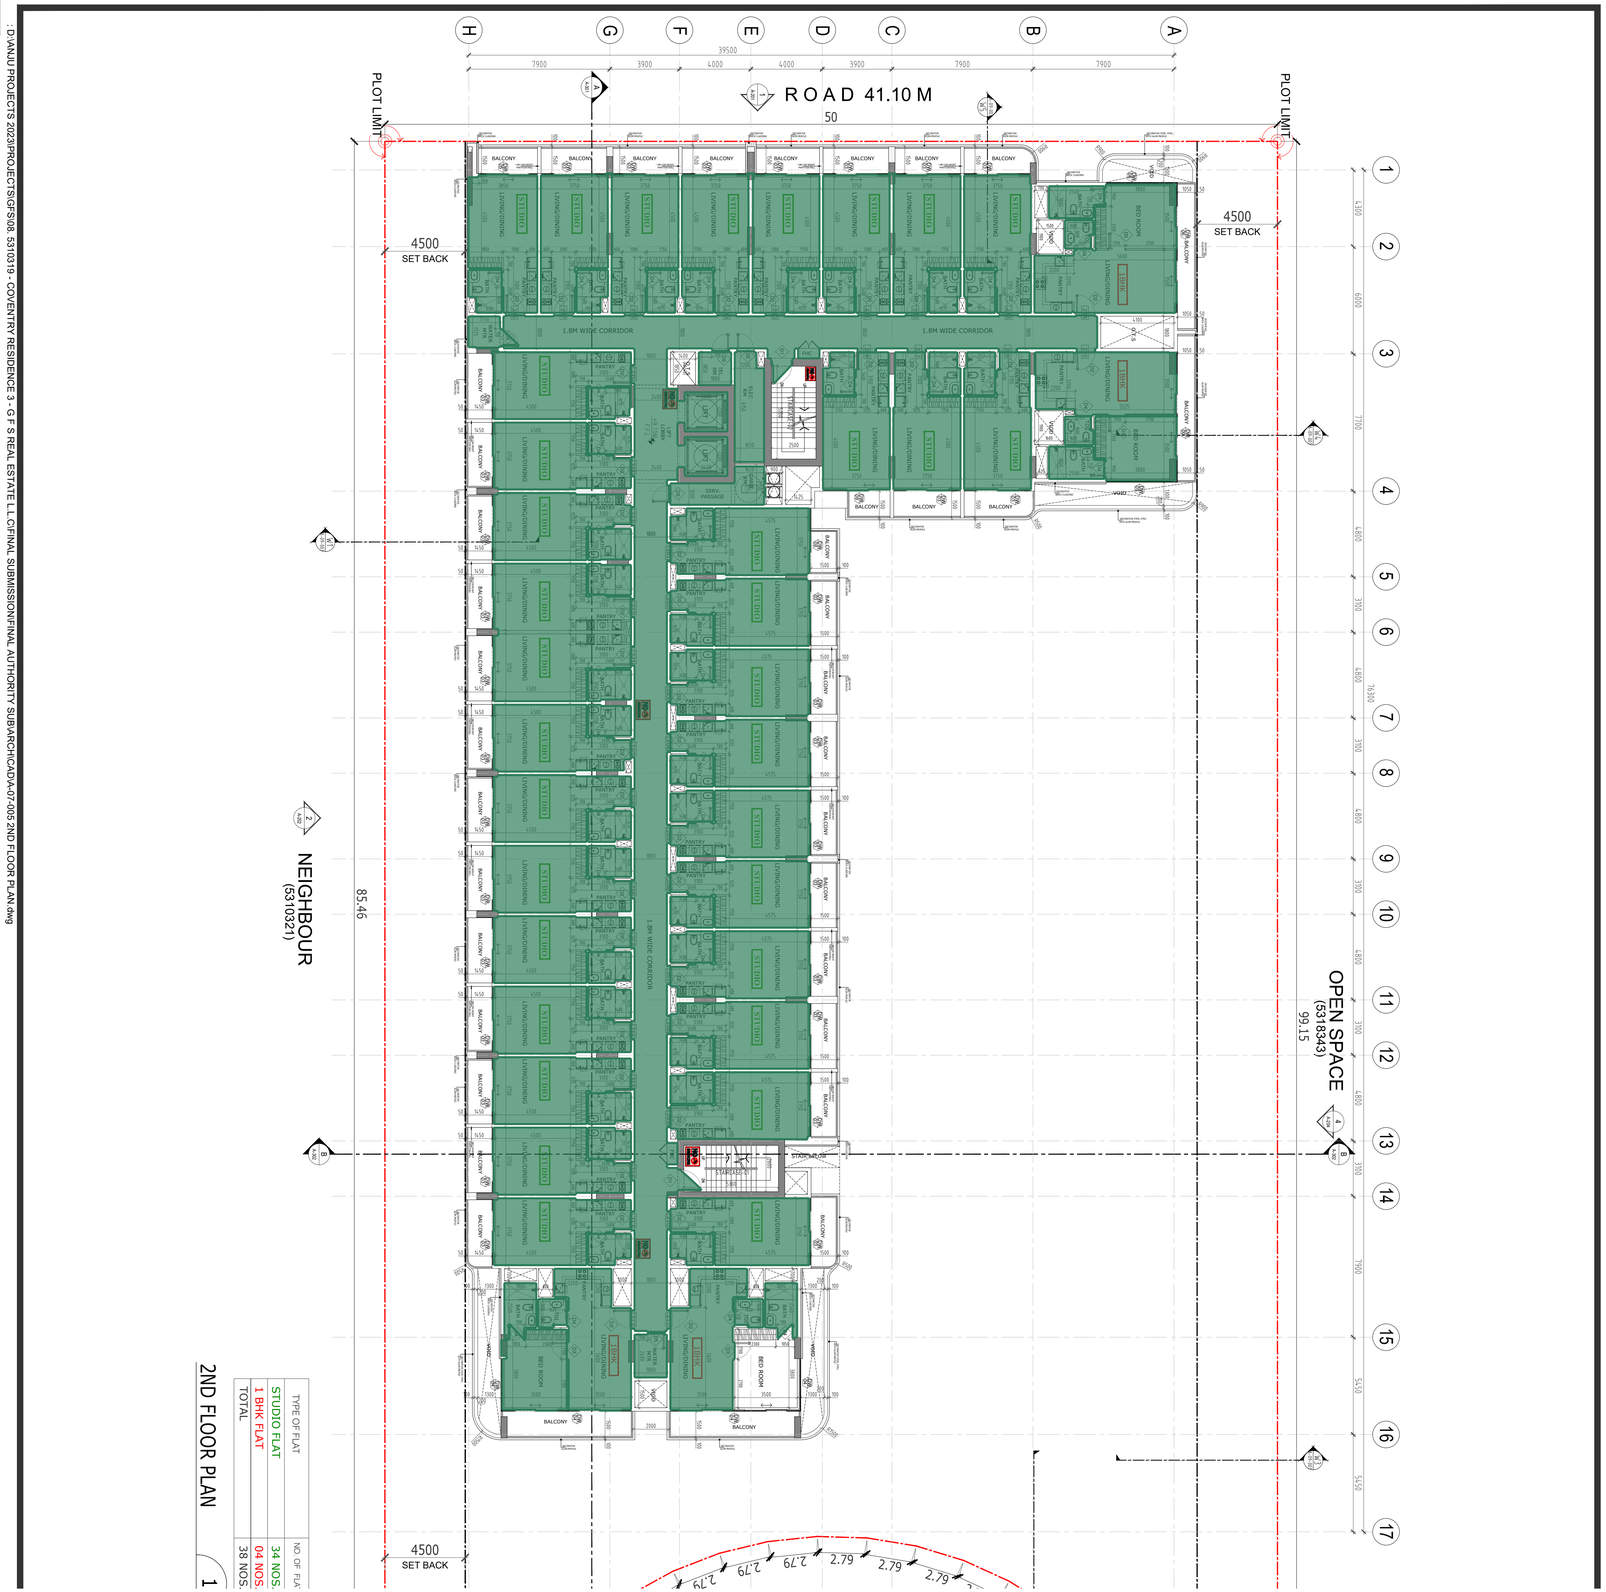

2ND FLOOR PLAN

TYPE OF FLAT	NO. OF FLA
STUDIO FLAT	34 NOS.
1 BHK FLAT	04 NOS.
TOTAL	38 NOS.

Legend

Finishes

- J-A 1,183.59 m2
- J-B 166.13 m2
- J-C 1,183.59 m2
- J-D 166.13 m2
- J-E 3,895.41 m2
- J-F 1,117.03 m2
- J-G 1,062.08 m
- J-H 296.48 m

D:\ANJU PROJECTS 2023\PROJECTS\GF\SO8 5310319 - COVENTRY RESIDENCE 3 - G F S REAL ESTATE L.L.C\FINAL SUBMISSION\FINAL AUTHORITY SUBMISSION\A-07-005 2ND FLOOR PLAN.dwg